



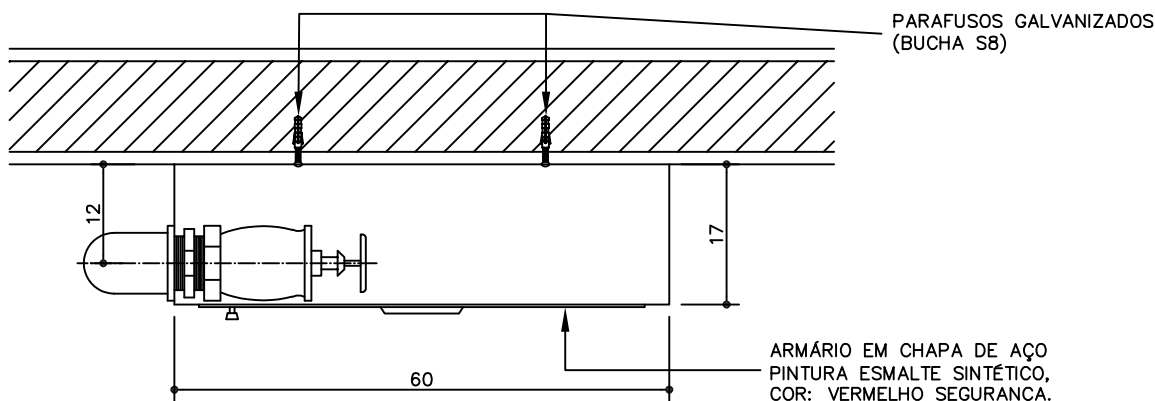

PLANTA
ESC. 1:10

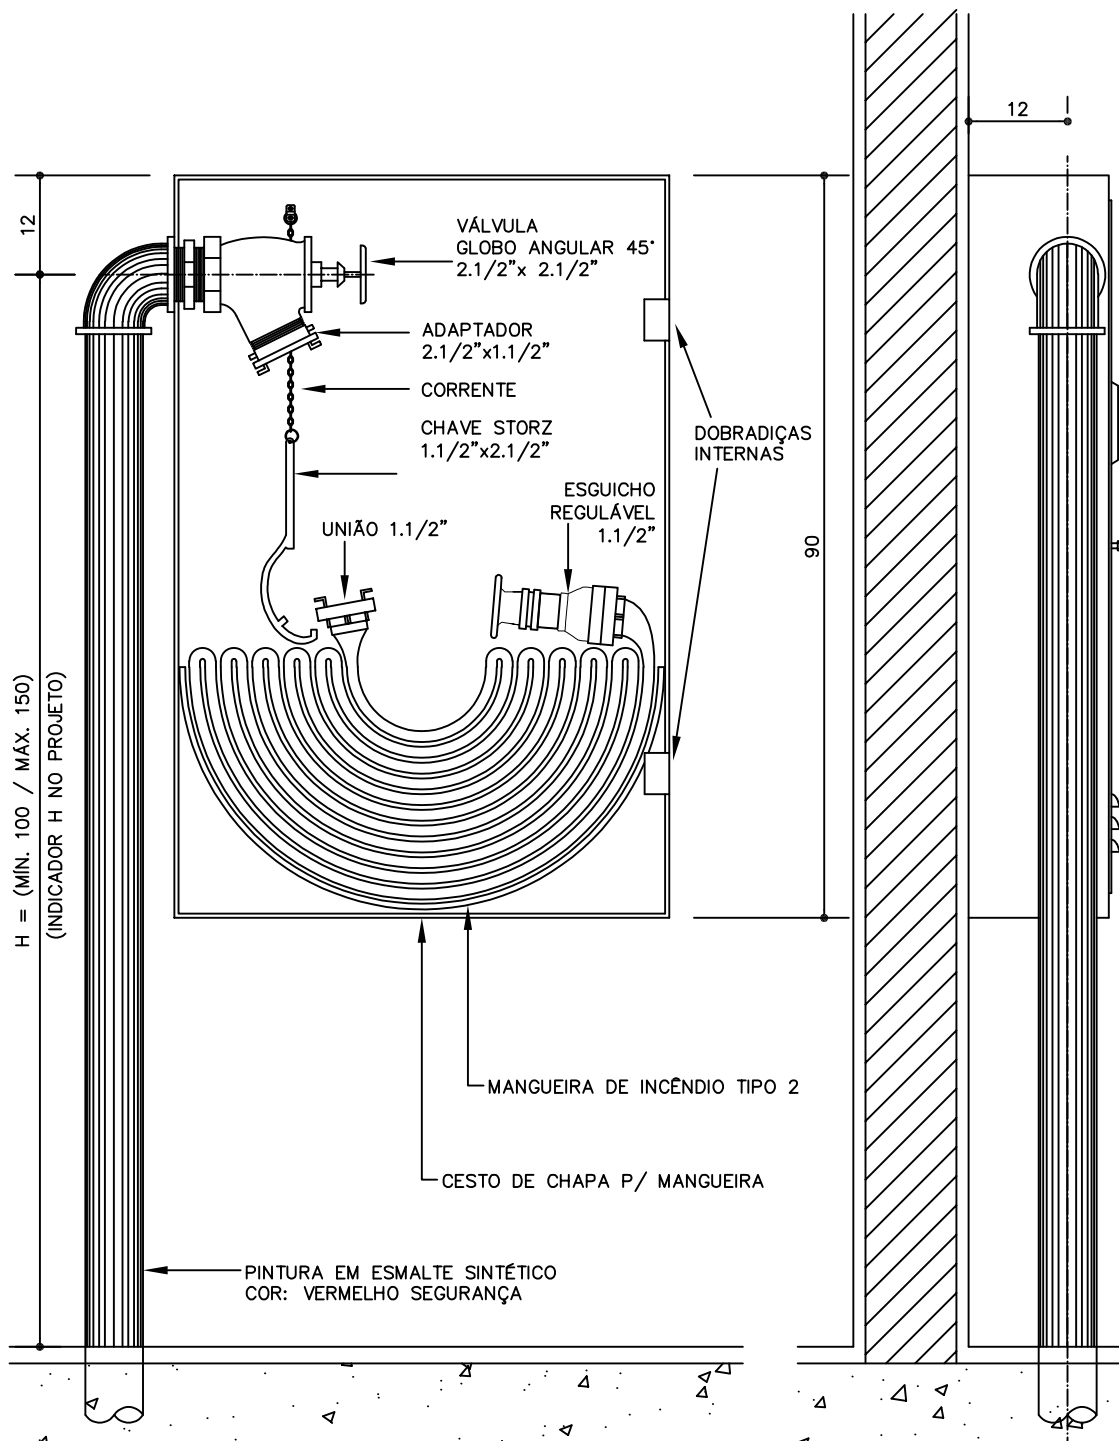

VISTA FRONTAL (INTERNA)
ESC. 1:10

VISTA LATERAL
ESC. 1:10

NOTA: PARA FIXAÇÃO EM ALVENARIA DE BLOCOS VAZADOS
(DE CONCRETO OU CERÂMICA),
UTILIZAR GRAUTE OU TACOS DE MADEIRA.

Medidas em centímetros

Componentes

AH-04

Abrigo para
hidrante
com man-
gueira e
esguicho
regulável

Revisão 1
Data 29/07/22

Página
1/3

Código de listagem

0808028



Atenção

Preserve a escala
Quando for imprimir, use
folhas A4 e desabilite a
função "Fit to paper"

Respeite o Meio Ambiente.
Imprima somente o ne-
cessário

FDE FUNDAÇÃO PARA O
DESENVOLVIMENTO
DA EDUCAÇÃO

AH-04

Abrigo para
hidrante
com man-
gueira e
esguicho
regulável

Revisão 1
Data 29/07/22

Página
2/3

Código de listagem

0808028




Atenção
Preserve a escala
Quando for imprimir, use
folhas A4 e desabilite a
função "Fit to paper"

Respeite o Meio Ambiente.
Imprima somente o ne-
cessário

DESCRIÇÃO

Constituintes

- Armário de sobrepor fabricado em aço carbono, chapa 20 (1,00mm), dimensões de (90x60x17) cm, com cesto meia lua para mangueira; tratamento anti-corrosivo, pintura em esmalte sintético cor vermelho segurança, sobre fundo primer. Porta dotada de ventilação; abertura no centro com área mínima de 0,04m² fechada com visor de vidro com a inscrição "INCÊNDIO" na cor branca ou amarela em fundo vermelho; dispositivo de fechadura ou tranca com chave mestra; dobradiças internas não visíveis na parte exterior do móvel.

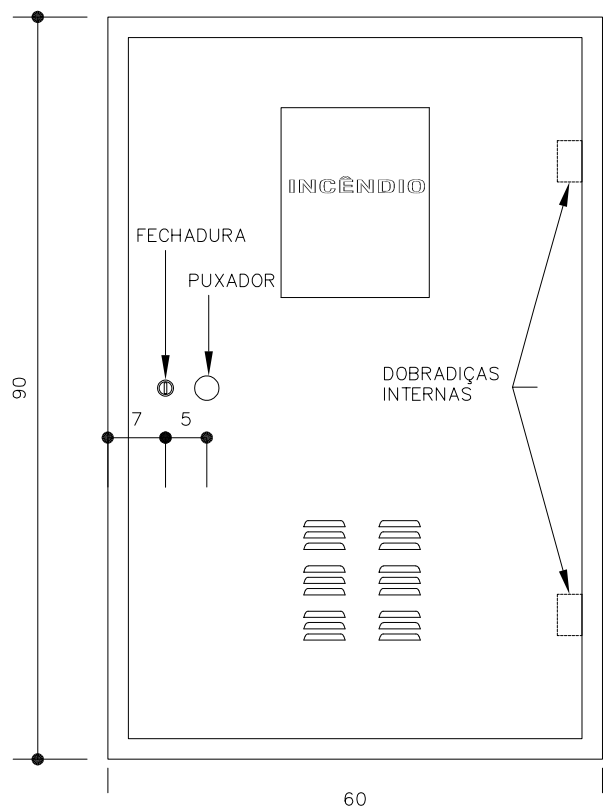

VISTA FRONTAL (ABRIGO)

ESC. 1:10

Medidas em centímetros

Observações:

- O armário deve ser entregue com suas partes montadas e protegidas para o transporte e instalação.
- O armário deve ser fornecido com os parafusos e buchas para a fixação na parede.

ATENÇÃO:

- O produto deve ser entregue acompanhado de 3 (três) chaves mestras, em consideração ao exposto no item 2.5 do Anexo D da Instrução Técnica nº 22 de 2019: "Nas edificações do Grupo E, e nas edificações F-4 e M-1, os abrigos poderão ser trancados com chaves-mestras disponíveis, respectivamente, na portaria e na secretaria escolar, e nas centrais de segurança e administração, bem como de posse dos seguranças locais".
- Deve ser assegurado que cada chave mestra acione as portas de todos os abrigos instalados na edificação.
- No fornecimento devem ser informados o nome do fabricante e o código do modelo do abrigo para preenchimento do TERMO DE RECEBIMENTO (ver ANEXO).

- Válvula globo angular 45°, em bronze ou latão, entrada Ø= 2.1/2" com rosca fêmea 11 F.p.p. (fios por polegada), saída Ø= 2.1/2" com rosca macho 5 F.p.p.
- Adaptador de engate rápido, conexão STORZ, em latão, para saída de registro, Ø=2.1/2" com rosca fêmea 5 F.p.p. x Ø = 1.1/2".
- Mangueira de incêndio tipo 2, com certificação INMETRO de conformidade à Portaria nº 148, de 13 de março de 2015, que aprova os requisitos de avaliação da conformidade para mangueiras de incêndio, atendendo aos requisitos da norma ABNT NBR 11861; diâmetro nominal de 40 mm (Ø interno =1.1/2") e comprimento =30m, com pressão de trabalho de 14kgf/cm² e pressão mínima de ruptura de 42 kgf/cm²; tubo interno de borracha sintética e revestimento externo de fibra sintética de alta resistência à ruptura e à abrasão; com união tipo engate rápido, de latão, tipo B, Ø=1.1/2" STORZ.

Observações:

- A mangueira deve possuir identificação individual, conforme ABNT NBR 12779, presa em seu corpo, próximo à união;
- Deve acompanhar certificado de inspeção, conforme ABNT NBR 12779, contendo como informações mínimas: identificação individual, fabricante, marca do duto flexível e uniões, diâmetro, comprimento, tipo, inspeção, data de execução, data da próxima inspeção e/ou manutenção, nome e assinatura do responsável pela inspeção.
- Esguicho de latão Ø=1.1/2" STORZ, regulável para emissão de jato compacto ou neblina.
- Chave de engate rápido, em latão, para conexão STORZ Ø=1.1/2" x 2.1/2", presa no fundo do armário através de corrente com elo soldado, galvanizada, espessura 3/64", comprimento 40cm, conforme desenho.

Acessórios

- Parafusos de aço galvanizado, cabeça panela, fenda philips, (5,0 x 50)mm e bucha de nylon S8 (fornecido com o abrigo).
- Fita veda-rosca de politetrafluoretileno.

Protótipo comercial:

- Armário:
 - LINTEMANI código 1-01-00085.
- Válvula globo angular:
 - BUCKA: F11 x M5 F.p.p. código 4.860.615.001;
 - KIDDE: código 934RC-00352;
 - COUTOFLEX: 210 LBS 45° código ORV 000208A.
- Adaptador:
 - BUCKA: Predial código 4.850.613.000;
 - RESIL: código 1300.61300;
 - COUTOFLEX: código RED-A.
- Mangueira tipo 2, Ø=1 1/2" com união:
 - BUCKA: PETRONYL 700 código 4.500.403.019;
 - KIDDE: SINTEX N código 934MA-00203;
 - RESIL: PLUS Tipo 2;
 - COUTOFLEX: SUPERFLEX 1.1/2".
- Esguicho regulável:
 - BUCKA: 200 código 4.350.230.003;
 - KIDDE: Mod. EBK código 934RC-00133;
 - RESIL: Elkhart código 1300 62100;
 - COUTOFLEX código OHD 000037 A.
- Chave de engate rápido:
 - BUCKA: Chave 1.1/2" x 2.1/2" Storz;
 - KIDDE: Chave E.R. dupla código 14018821;
 - RESIL código 1300.61200;
 - COUTOFLEX: Chave Storz dupla.
- Parafusos e buchas:
 - FISCHER: bucha de expansão S8 Art Nº 601952.

- FISCHER: parafuso cabeça panela rosca total Art Nº 600466.
- Corrente 3/64":
 - CORRENTES MERRINI.
 - INTER CABOS.
 - SÃO RAPHAEL METALÚRGICA.

APLICAÇÃO

- Para escolas e diretorias de ensino.
- Em áreas comuns cobertas e em locais facilmente visíveis onde haja menor probabilidade do fogo, bloquear seu acesso conforme indicado em projeto.

Observação:

- O Projeto deverá indicar H (altura da válvula angular), observando que para H > 138cm, será necessário indicar o piso tátil de alerta conforme ABNT NBR 9050.

Sinalização

- O Projeto deverá indicar a sinalização de emergência referente a este equipamento, em atendimento à Instrução Técnica nº 20 do Corpo de Bombeiros da Polícia Militar do Estado de São Paulo e de acordo com o Manual do Sistema de Sinalização para Edificações Escolares.

EXECUÇÃO

- Instalar o abrigo com mangueira na altura indicada em projeto. Fixar o armário com 04 (quatro) parafusos. Caso a alvenaria seja de blocos vazados (de concreto ou cerâmica), utilizar graute ou tacos de madeira para fixação.
- Na saída da tubulação, usar fita veda-rosca para instalar a válvula globo angular.
- Instalar a sinalização de emergência de acordo com indicação em projeto e Ficha SI-03.

FICHAS DE REFERÊNCIA

Catálogo de Componentes

Ficha SI-03 Placa 20X20cm Acabamento Fotoluminescente (Parede)

Catálogo de Serviços

Ficha H3 Combate a incêndio

RECEBIMENTO

- O serviço pode ser recebido se atendidas todas as condições de projeto, fornecimento e execução.
- Verificar se todos os constituintes e acessórios possuem as dimensões indicadas.
- Armário: verificar fixação com 04 (quatro) parafusos, prumo, pintura sem defeitos, ausência de amassados e perfeita abertura e fechamento da porta.
- Verificar a ausência de rasgos, furos ou desfiamentos na mangueira.
- Verificar existência de vazamentos ou gotejamento na válvula.
- Verificar instalação de todos os constituintes e acessórios.
- Exigir e verificar as informações contidas no certificado de inspeção da mangueira.
- Verificar a instalação da sinalização de emergência, de acordo com o projeto.
- A entrega das chaves mestras do armário deve ser notificada através do TERMO DE RECEBIMENTO (ver ANEXO), contendo a assinatura do responsável pelo recebimento das chaves pela Unidade Escolar.

SERVIÇOS INCLUÍDOS NO PREÇO

- Armário e chaves mestras.
- Válvula globo angular 45°.

- Adaptador 2.1/2" x 1.1/2".
- Mangueira com união.
- Esguicho.
- Chave de engate rápido.
- Corrente 3/64", comprimento 40 cm.
- Acessórios.

Observação:

- A sinalização de emergência será paga em outro serviço.

CRITÉRIOS DE MEDIÇÃO

- un. — por unidade instalada.

NORMAS

- Instrução Técnica nº 20:2019 – Sinalização de Emergência, do CBPMESP- Corpo de Bombeiros da Polícia Militar do Estado de São Paulo.
- Instrução Técnica nº 22:2019 – Sistema de hidrantes e de mangotinhos para combate a incêndio, do CBPMESP.
- ABNT NBR 9050:2020 Versão corrigida: 2021 – Acessibilidade a edificações, mobiliário, espaços e equipamentos urbanos.
- ABNT NBR 11861:1998 – Mangueira de incêndio – Requisitos e métodos de ensaio.
- ABNT NBR 13714:2000 – Sistemas de hidrantes e de mangotinhos para combate a incêndio.
- ABNT NBR 12779: 2009 – Mangueira de incêndio - Inspeção, manutenção e cuidados.
- ABNT NBR 14349: 1999 – União para mangueira de incêndio - Requisitos e métodos de ensaio.

Observação:

- As edições indicadas estavam em vigor no momento desta publicação. Como toda norma está sujeita a revisão, recomenda-se verificar a existência de edições mais recentes das normas citadas.

Componentes

AH-04

Abrigo para hidrante com mangueira e esguicho regulável

Revisão 1
Data 29/07/22

Página

3/3

Código de listagem

0808028



Atenção

Preserve a escala
Quando for imprimir, use folhas A4 e desabilite a função "Fit to paper"

Respeite o Meio Ambiente.
Imprima somente o necessário

FDE FUNDAÇÃO PARA O DESENVOLVIMENTO DA EDUCAÇÃO

Termo de Recebimento de Chaves mestras – Abrigo para hidrante AH-04

Eu _____,
portador (a) do R.G. _____ e no exercício do cargo de _____
da EE/DE _____
(código FDE _____), situada na:
Rua _____,
n.º _____, bairro _____,
cidade _____, CEP _____, fone _____,
declaro que recebi nesta data das mãos de _____,
RG: _____, cargo: _____,
Empresa: _____,
o(s) abrigos para hidrante(s), código FDE AH-04:
Fabricante: _____ modelo: _____.
- Quantidade: _____ abrigo (s).

Declaro que recebi nesta data, as chaves mestras que foram testadas em todos os abrigos desta Unidade, e que deverão ficar em posse, conforme IT-20 do CBPMESP, da portaria, da secretaria escolar, das centrais de segurança e administração, e dos seguranças locais:

- Quantidade: _____ chaves.

Declaro ainda estar ciente da responsabilidade de assegurar que estas chaves sejam utilizadas exclusivamente para a utilização dos abrigos para hidrantes. Além disso, estou ciente de que os abrigos deverão ter seu acesso restrito a pessoal e a empresas capacitadas para a inspeção e manutenção de seus componentes, e ao Corpo de Bombeiros da Polícia Militar do Estado de São Paulo - CBPMESP.

Por fim, declaro estar ciente da responsabilidade quanto à conservação e integridade dos abrigos e de seus componentes.

Local:

Data:

Assinaturas:

Responsável pelo recebimento

Responsável pela entrega

ANEXO

Termo de recebimento de chaves mestras

Revisão 0
Data 29/07/22

Página

1/1

Código de listagem

0808028



Atenção

Preserve a escala
Quando for imprimir, use
folhas A4 e desabilite a
função "Fit to paper"

Respeite o Meio Ambiente.
Imprima somente o ne-
cessário