




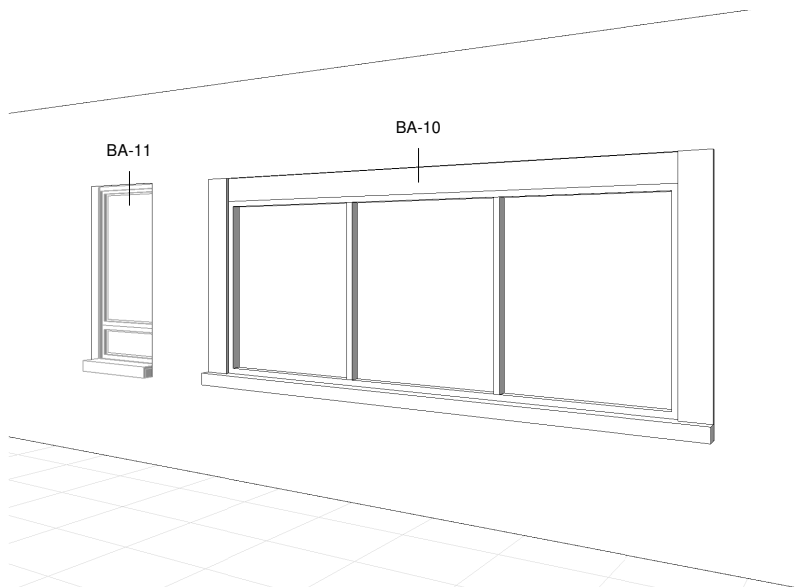

EXEMPLO DE COMPOSIÇÃO BA-10 E BA-11 - VISTA EXTERNA

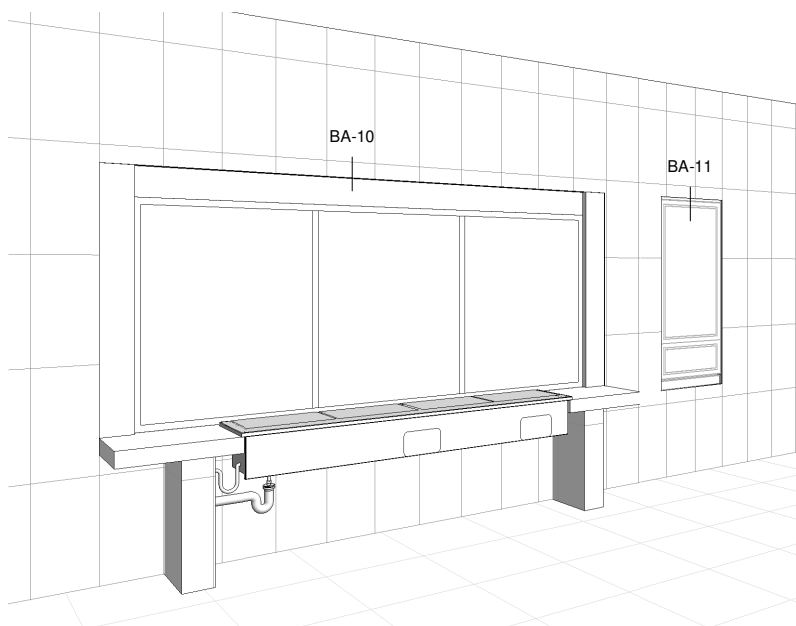

EXEMPLO DE COMPOSIÇÃO BA-10 E BA-11 - VISTA INTERNA

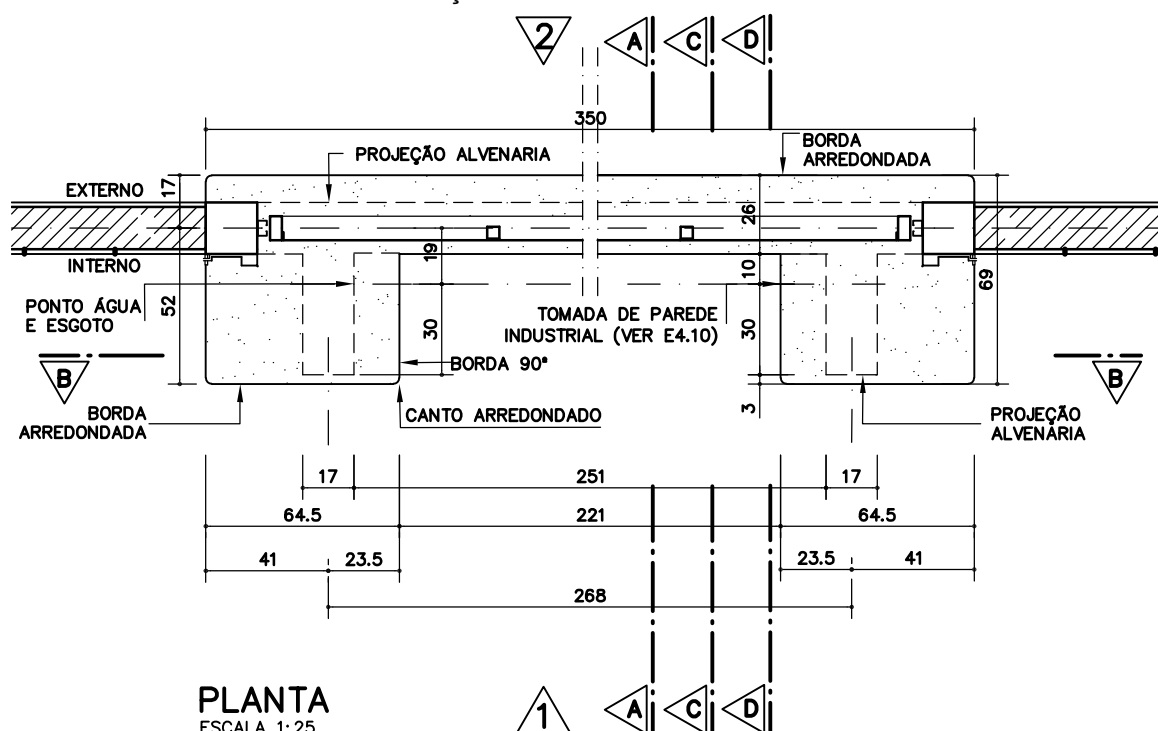

BA-10

Balcão de distribuição granito

(L=350cm)

Obs.: Este componente deve receber o Balcão térmico fixo (BT-02). Utilizar o serviço

16.06.103
Instalação de Balcão
térmico fixo (BT-02)

Revisão	8
Data	17/02/25

Página

1/11

Código de listagem

05.05.089



Atenção

Preserve a escala
Quando for imprimir, use
folhas A4 e desabilite a
função "Fit to paper"

Respeite o Meio Ambiente.
Imprima somente o necessário

BA-10

Balcão de distribuição granito

(L=350cm)

Obs.: Este componente deve receber o Balcão térmico fixo (BT-02). Utilizar o serviço 16.06.103 Instalação de Balcão térmico fixo (BT-02)

Revisão 8
Data 17/02/25


Página
2/11


Código de listagem

05.05.089

Atenção
Preserve a escala
Quando for imprimir, use folhas A4 e desabilite a função "Fit to paper"

Respeite o Meio Ambiente.
Imprima somente o necessário

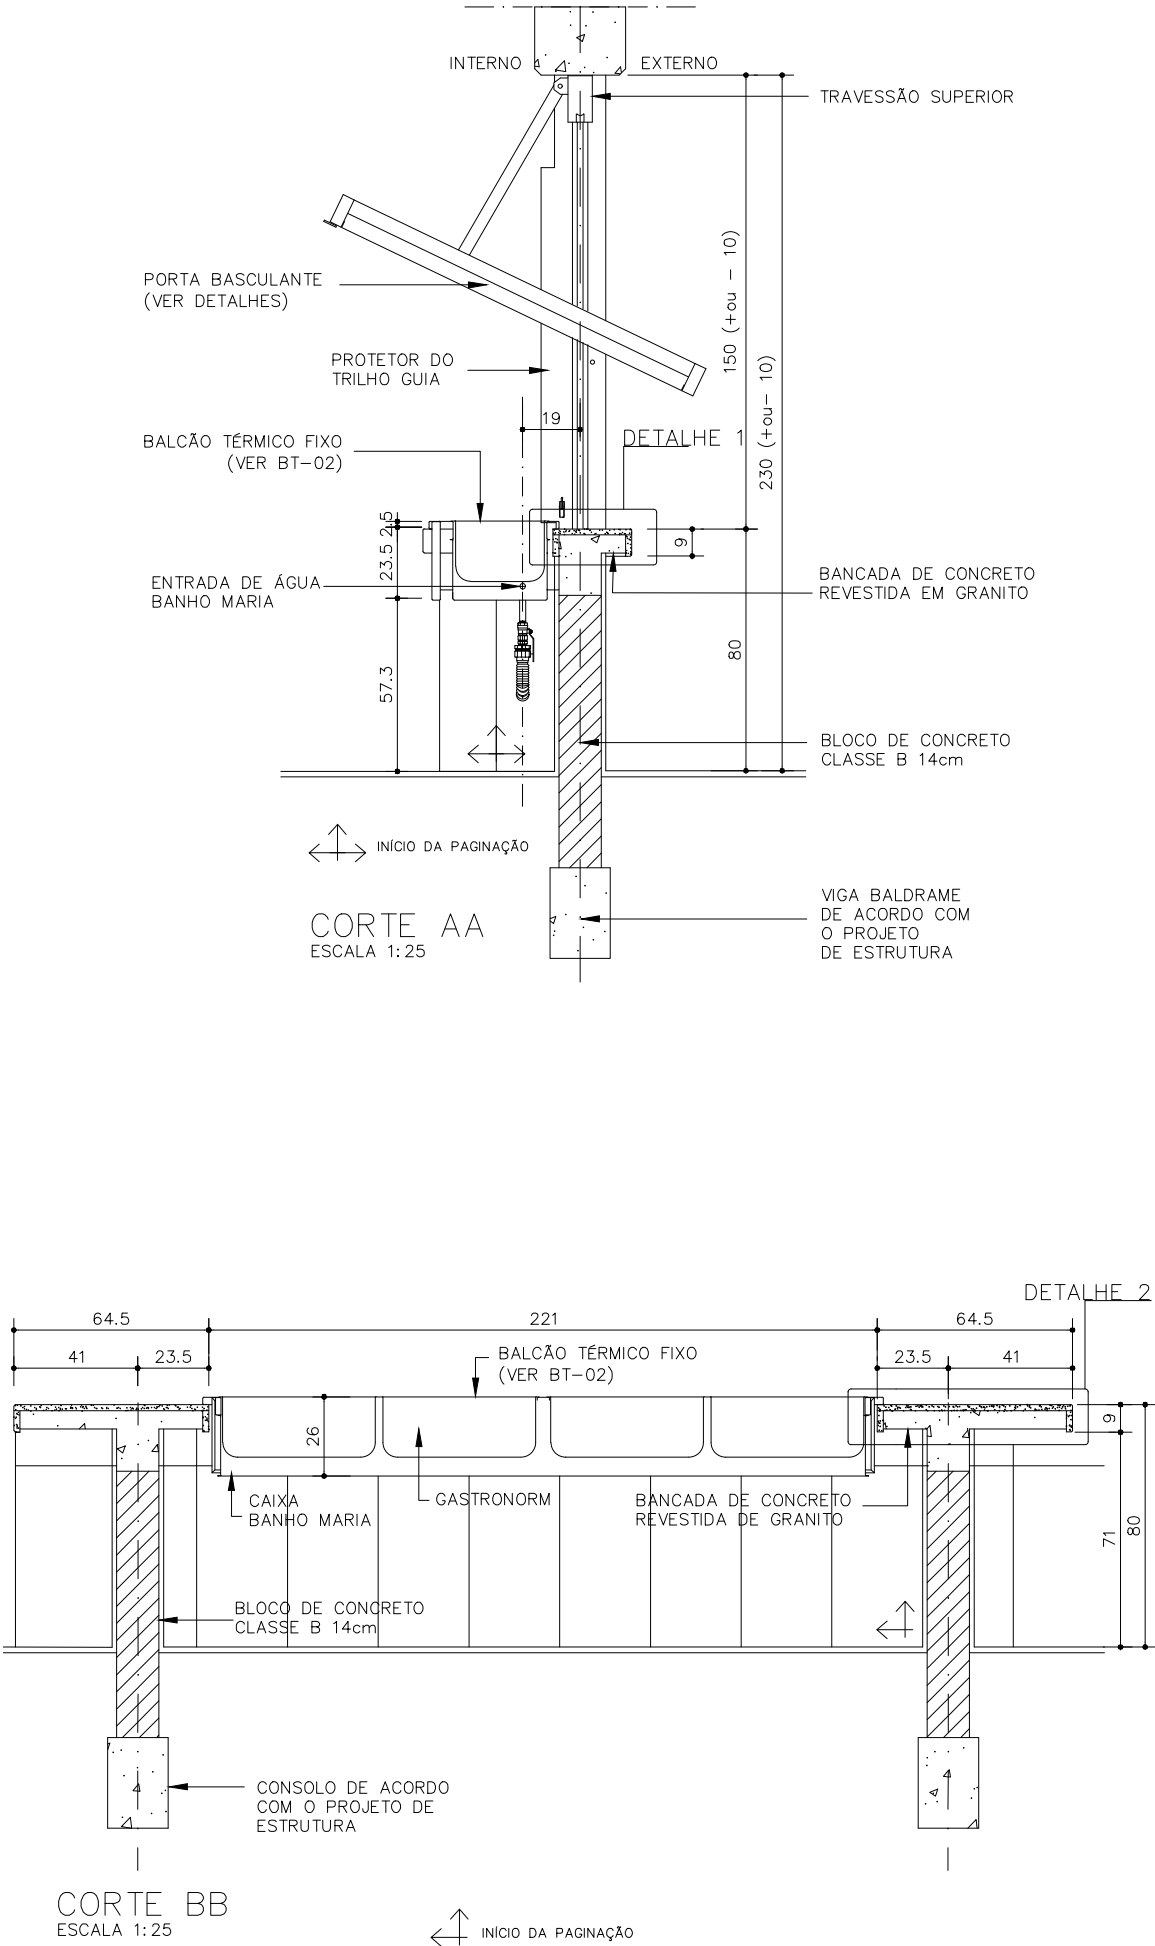


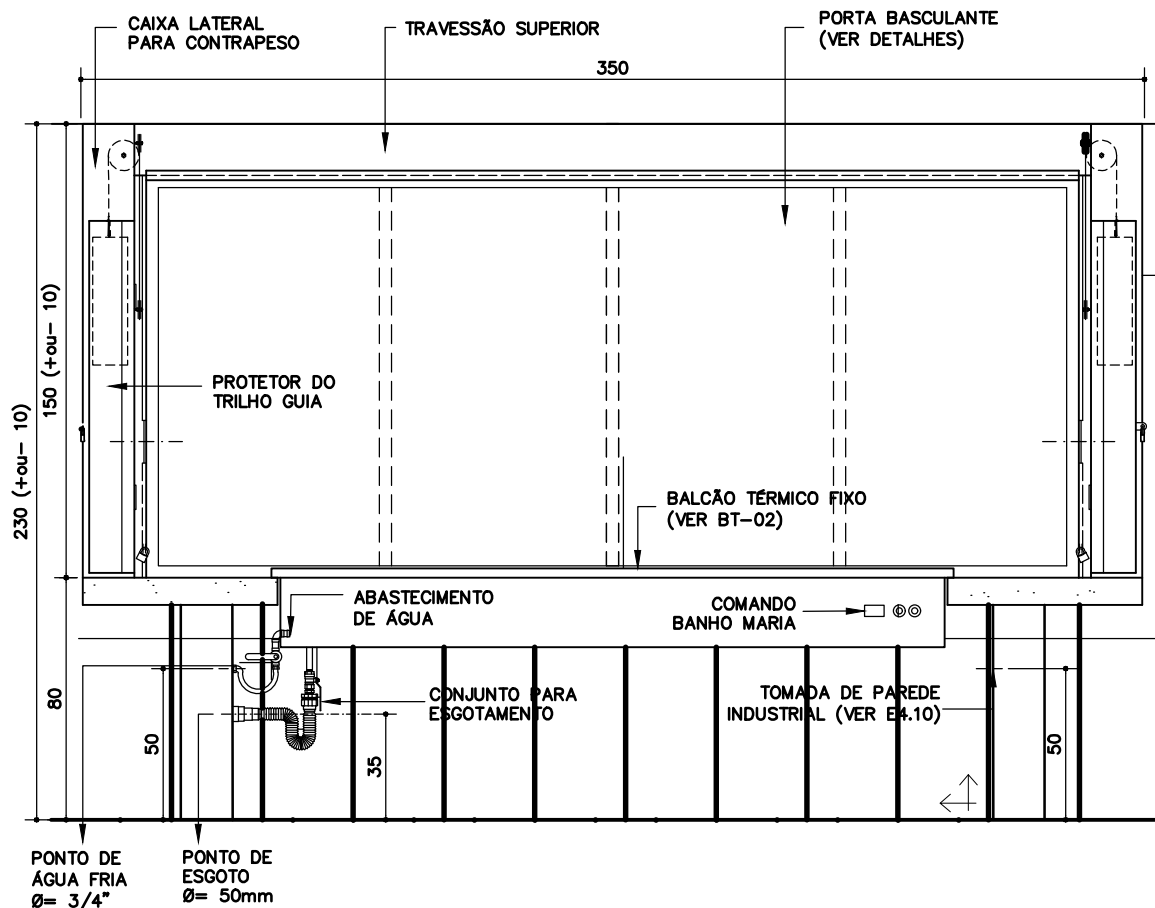

VISTA 1

ESCALA 1:25

INÍCIO DA PAGINAÇÃO

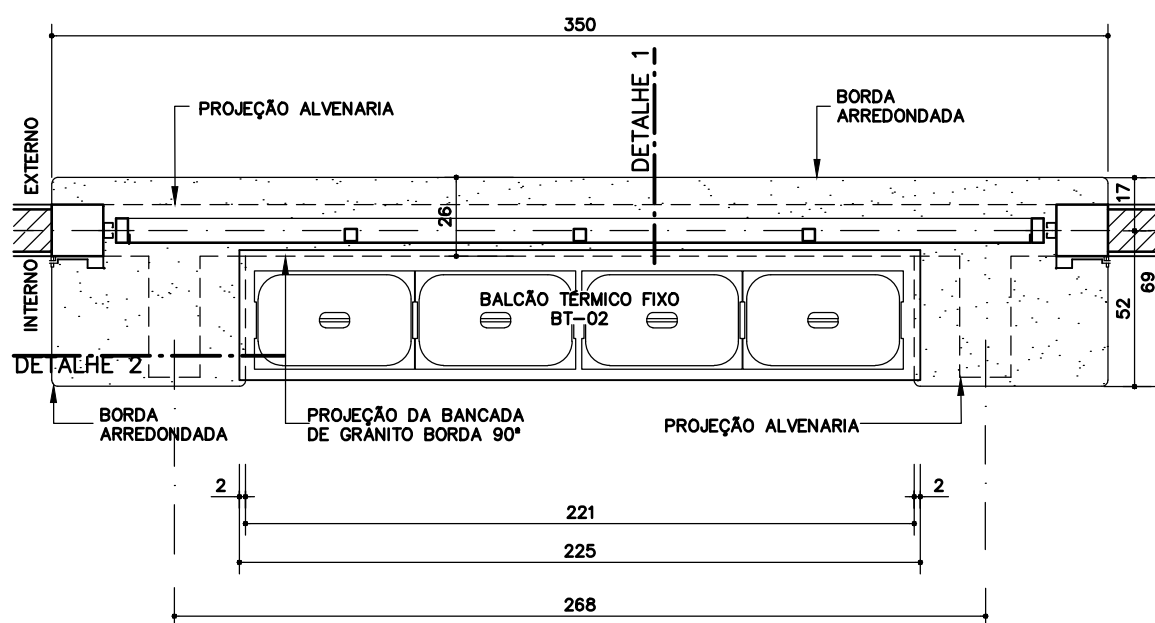

PLANTA BA-10 COM BT-02

ESCALA 1:25

BA-10

Balcão de distribuição granito

(L=350cm)

Obs.: Este componente deve receber o Balcão térmico fixo (BT-02). Utilizar o serviço 16.06.103 Instalação de Balcão térmico fixo (BT-02)

Revisão 8
Data 17/02/25

Página

3/11

Código de listagem

05.05.089



Atenção

Preserve a escala
Quando for imprimir, use
folhas A4 e desabilite a
função "Fit to paper"

Respeite o Meio Ambiente.
Imprima somente o ne-
cessário

BA-10

Balcão de distribuição granito

(L=350cm)

Obs.: Este componente deve receber o Balcão térmico fixo (BT-02). Utilizar o serviço 16.06.103 Instalação de Balcão térmico fixo (BT-02)



Revisão 8
Data 17/02/25

Página
4/11

Código de listagem
05.05.089



Atenção
Preserve a escala
Quando for imprimir, use folhas A4 e desabilite a função "Fit to paper"

Respeite o Meio Ambiente.
Imprima somente o necessário

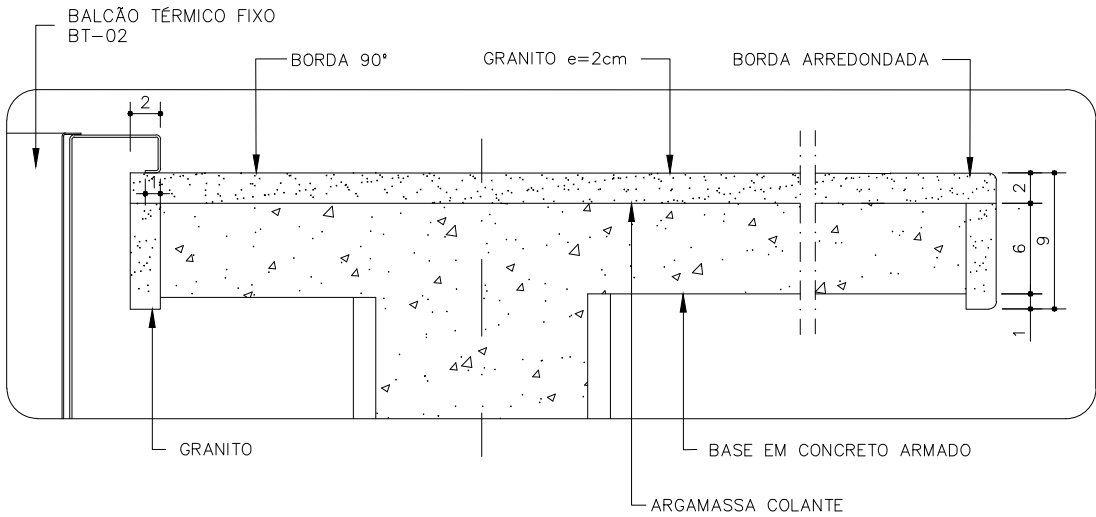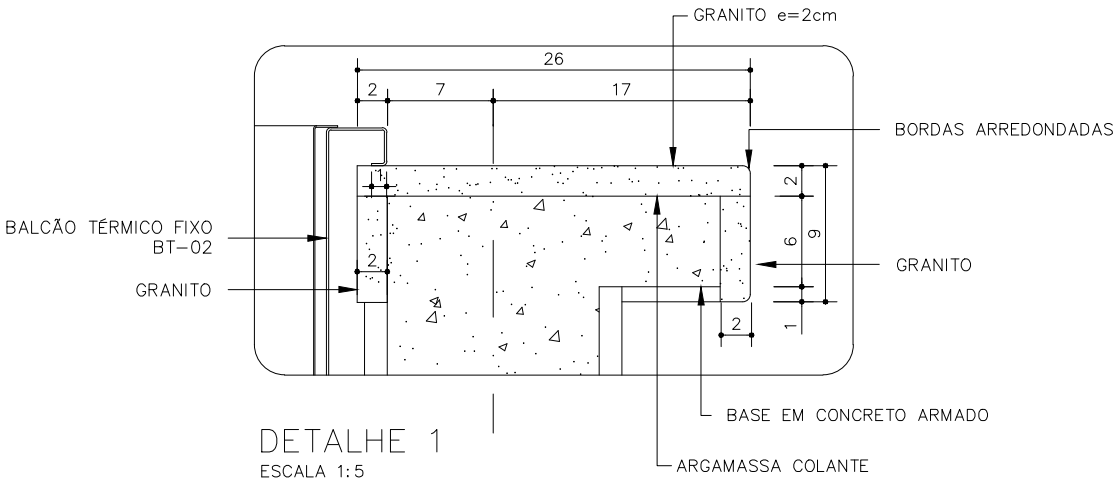

DETALHE 2
ESCALA 1:5

PORTA BASCULANTE

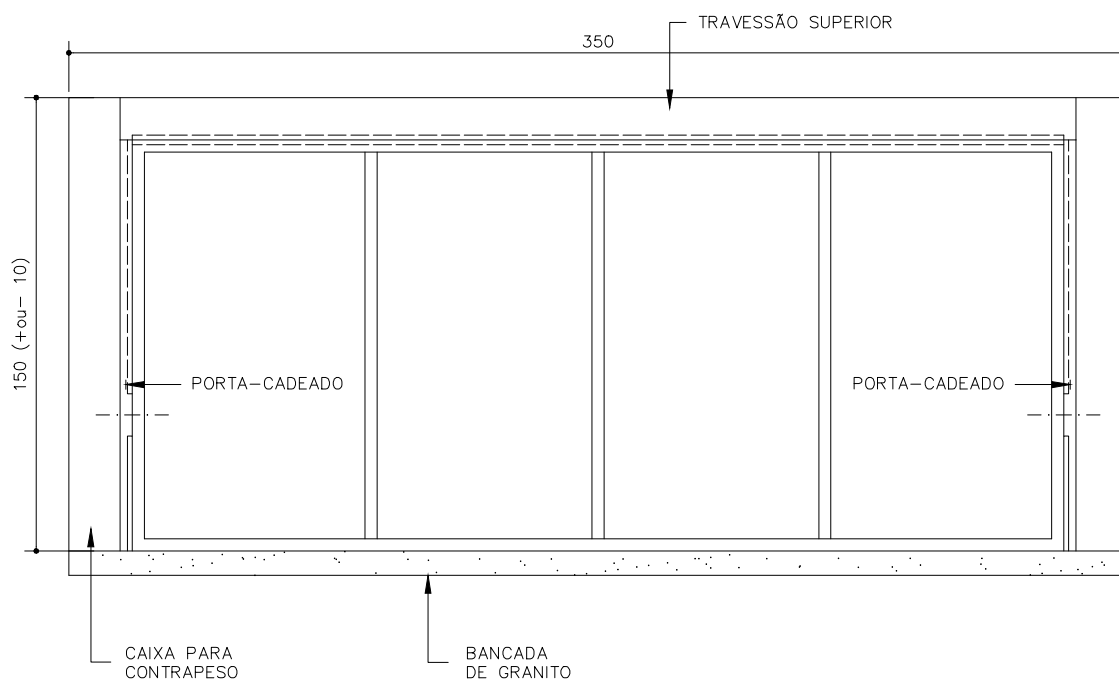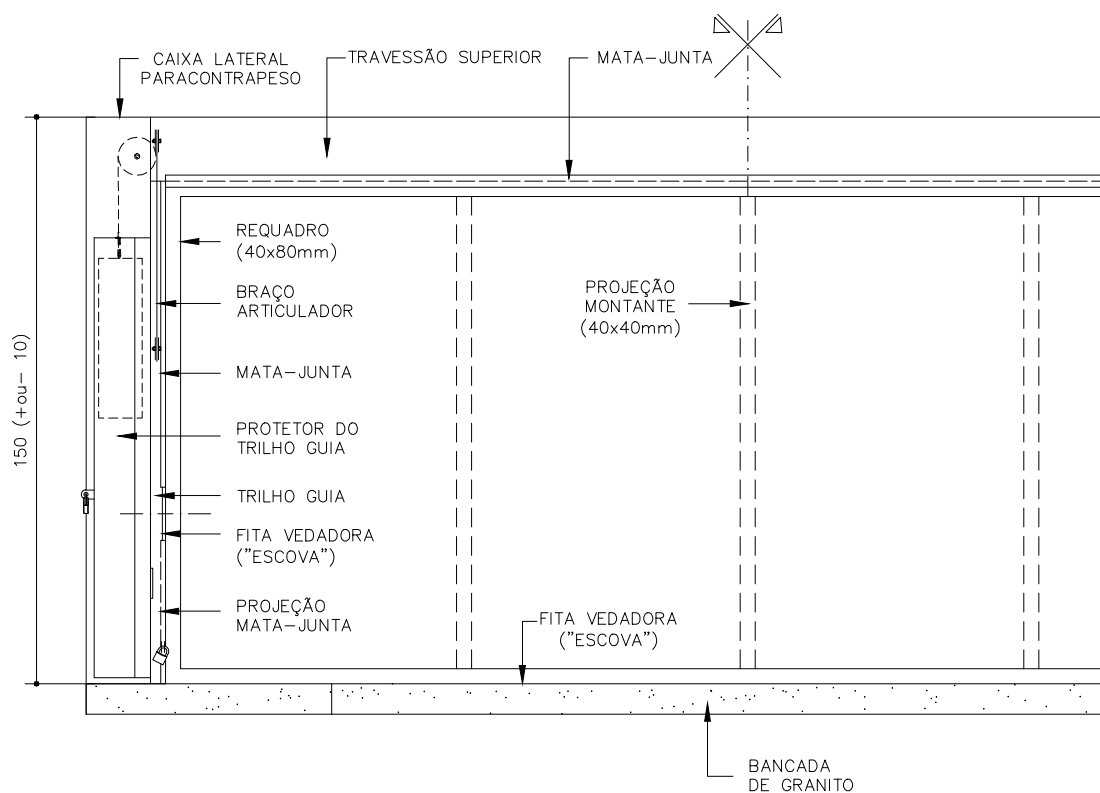VISTA 2
ESCALA 1:25AMPLIAÇÃO PARCIAL – VISTA INTERNA
ESCALA 1:20

BA-10

Balcão de
distribuição
granito

(L=350cm)

Obs.: Este
componente deve
receber o Balcão
térmico fixo (BT-02).
Utilizar o serviço

16.06.103
Instalação de Balcão
térmico fixo (BT-02)

Revisão 8
Data 17/02/25

Página
5/11

Código de listagem

05.05.089



Atenção

Preserve a escala
Quando for imprimir, use
folhas A4 e desabilite a
função "Fit to paper"

Respeite o Meio Ambiente.
Imprima somente o ne-
cessário

BA-10

Balcão de distribuição granito

[L=350cm]

Obs.: Este componente deve receber o Balcão térmico fixo [BT-02]. Utilizar o serviço 16.06.103 Instalação de Balcão térmico fixo [BT-02]

Revisão 8
Data 17/02/25


Página
6/11

Código de listagem


05.05.089

Atenção
Preserve a escala
Quando for imprimir, use folhas A4 e desabilite a função "Fit to paper"


Respeite o Meio Ambiente.
Imprima somente o necessário

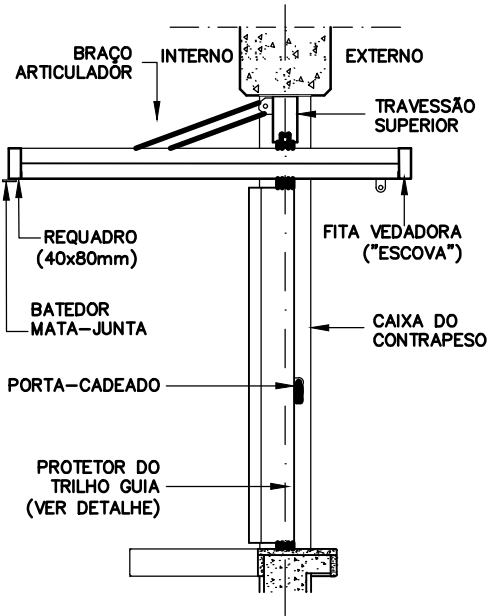


CORTE CC
POSIÇÃO ABERTA
ESCALA 1:25

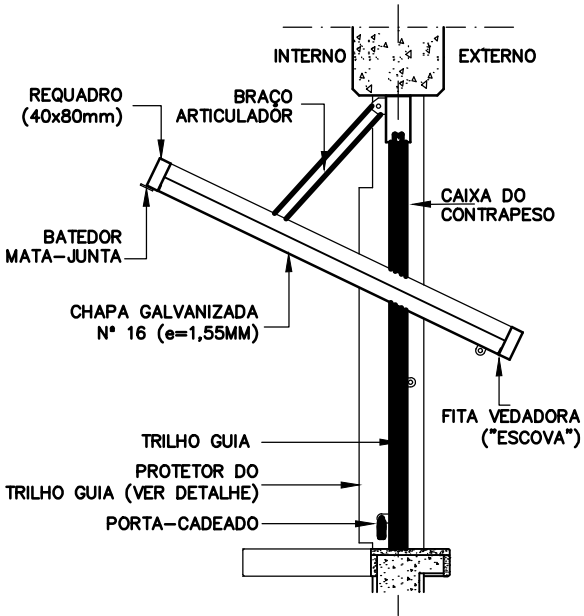

CORTE DD
POSIÇÃO SEMI-ABERTA
ESCALA 1:25

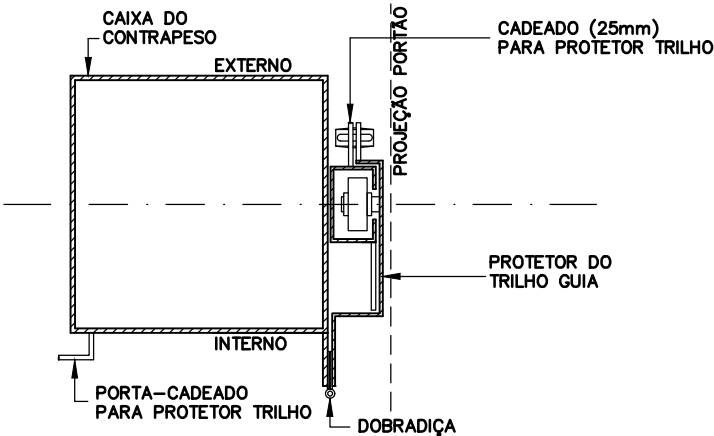


DETALHE PROTETOR DO TRILHO-GUIA
(POSIÇÃO PORTA ABERTA)
ESCALA 1:5

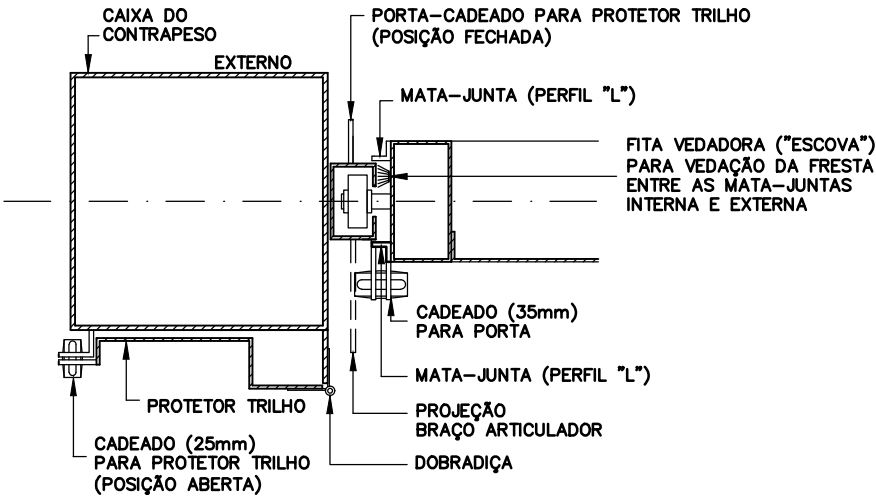


DETALHE PROTETOR DO TRILHO-GUIA
(POSIÇÃO PORTA FECHADA)

ESTRUTURA (OPÇÃO PAVIMENTO TÉRREO)


Componentes

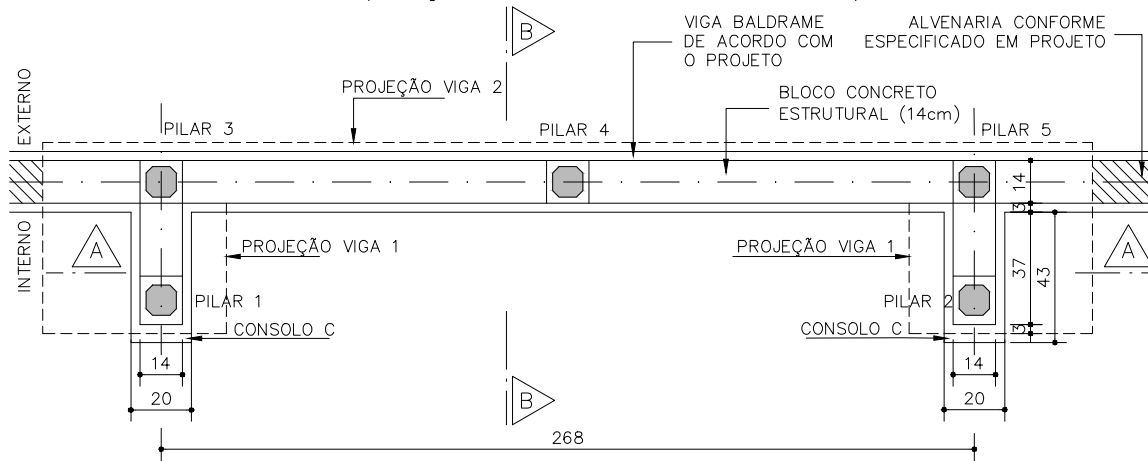

PLANTA
ESCALA 1:25

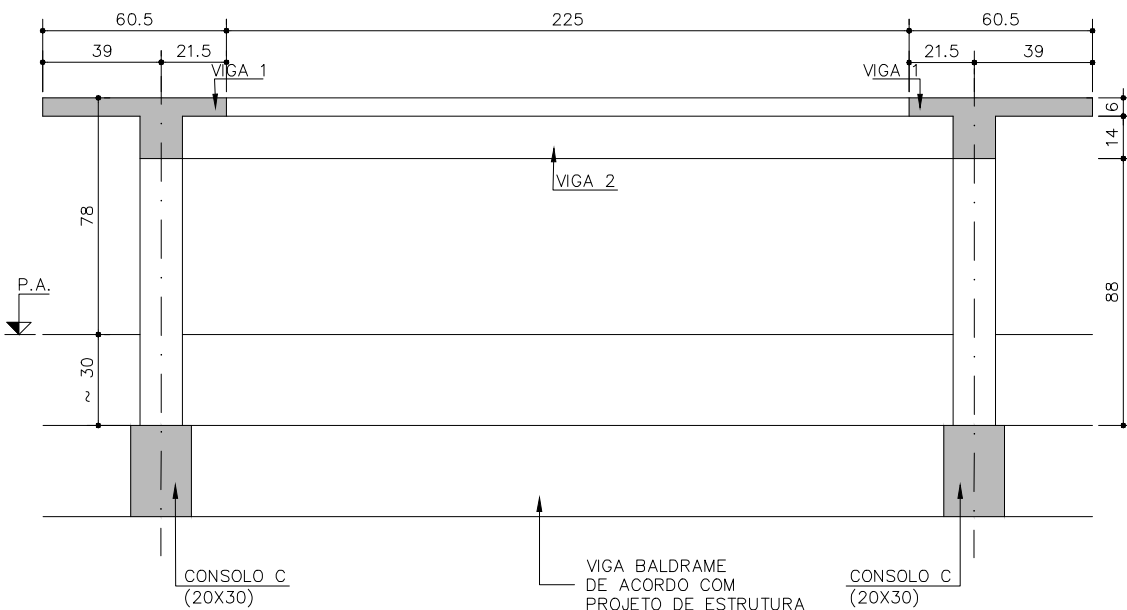

CORTE AA
ESCALA 1:25

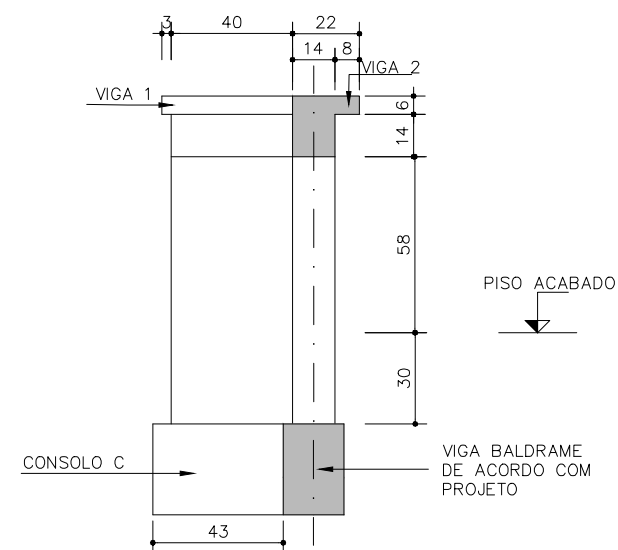

CORTE BB
ESCALA 1:25

NOTA:

1. EM PAVIMENTO TÉRREO, O CONSOLO JUNTO À VIGA BALDRAME DEVERÁ CONSTAR DO PROJETO DE ESTRUTURA.
2. EM PAVIMENTO SUPERIOR, O PROJETO DE ESTRUTURA DEVERÁ INDICAR A SOLUÇÃO ALTERNATIVA

BA-10

Balcão de distribuição granito

(L=350cm)

Obs.: Este componente deve receber o Balcão térmico fixo (BT-02). Utilizar o serviço 16.06.103 Instalação de Balcão térmico fixo (BT-02)

Revisão 8
Data 17/02/25

Página
7/11

Código de listagem

05.05.089



Atenção

Preserve a escala
Quando for imprimir, use folhas A4 e desabilite a função "Fit to paper"

Respeite o Meio Ambiente.
Imprima somente o necessário

BA-10

Balcão de distribuição granito

(L=350cm)
Obs.: Este componente deve receber o Balcão térmico fixo (BT-02). Utilizar o serviço 16.06.103 Instalação de Balcão térmico fixo (BT-02)

Revisão 8
Data 17/02/25


Página
8/11

Código de listagem




05.05.089

Atenção
Preserve a escala
Quando for imprimir, use folhas A4 e desabilite a função "Fit to paper"


Respeite o Meio Ambiente.
Imprima somente o necessário

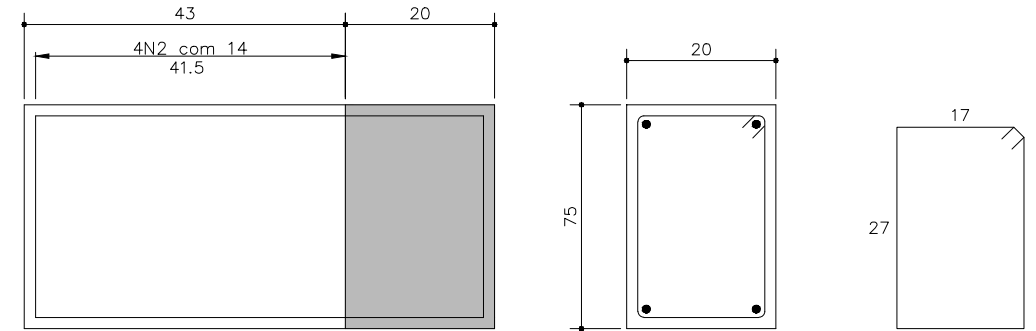

CONSOLO C (20X30)
ESCALA 1:10

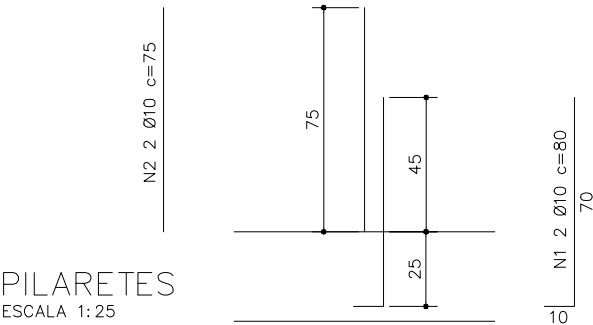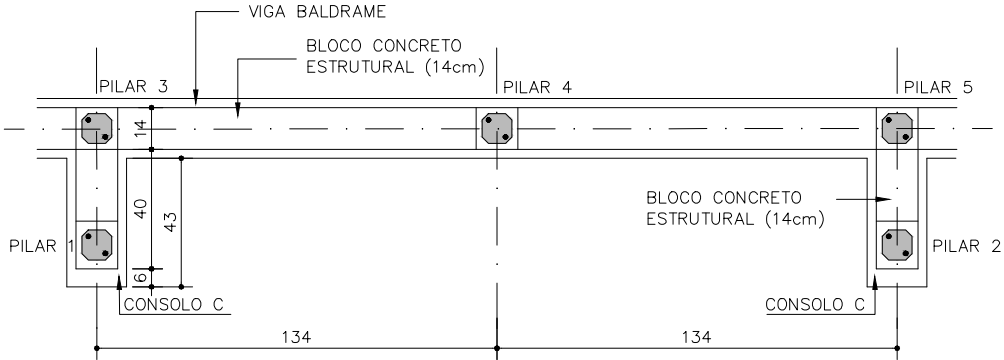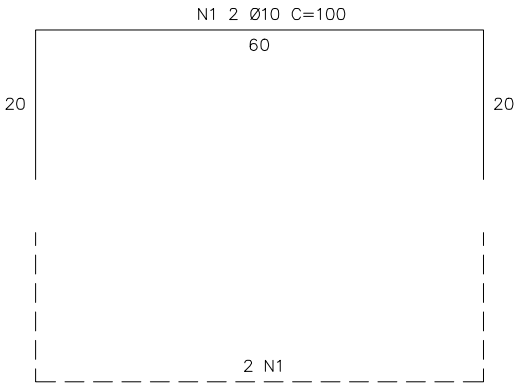

BLOCOS PREENCHIDOS COM GRAUTE
PILAR 1=PILAR 2=PILAR 3=
PILAR 4=PILAR 5 (5X)

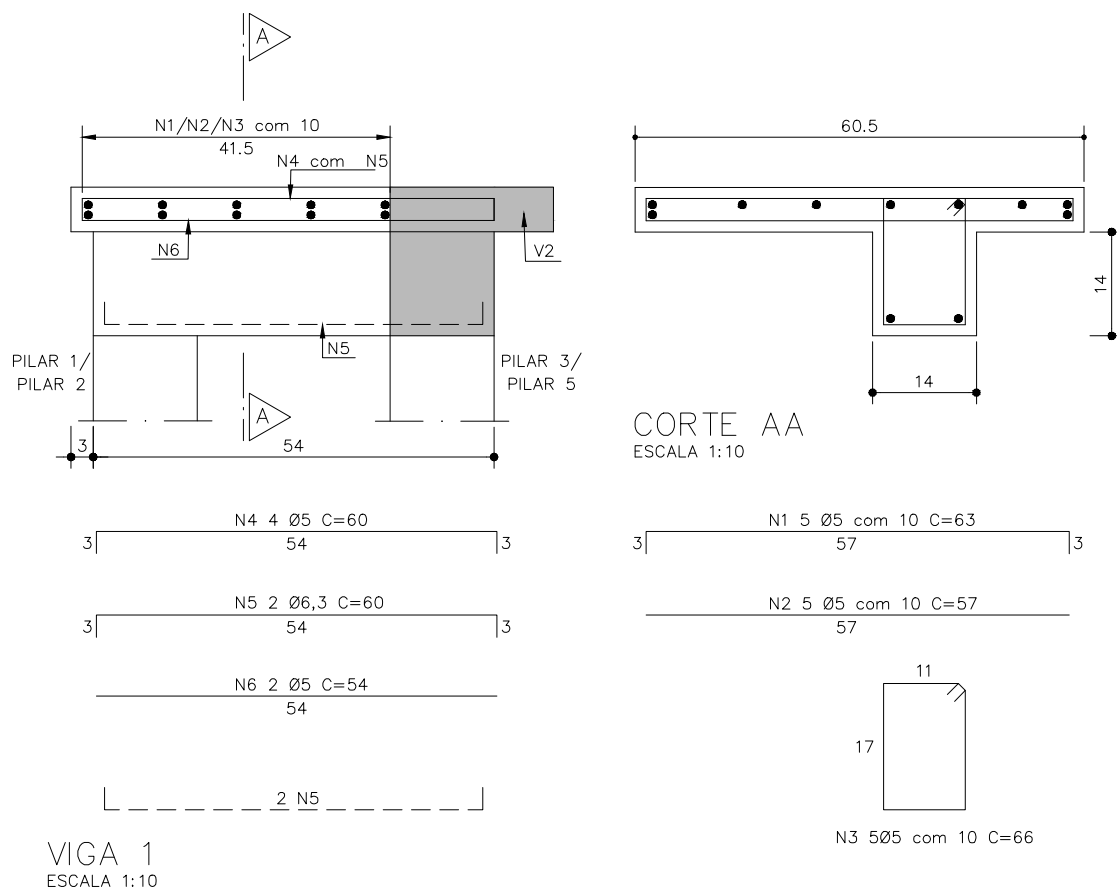

BA-10

Balcão de distribuição granito

(L=350cm)

Obs.: Este componente deve receber o Balcão térmico fixo (BT-02). Utilizar o serviço 16.06.103

Instalação de Balcão térmico fixo (BT-02)


Revisão 8
Data 17/02/25

Página

9/11

Código de listagem

05.05.089

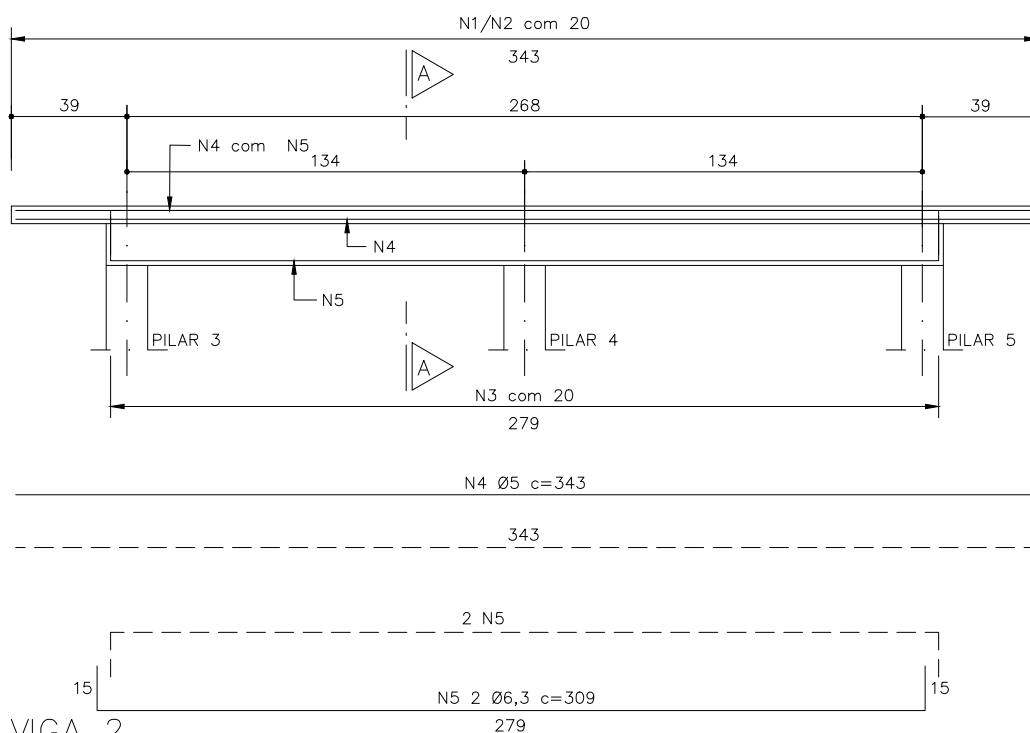

Atenção

Preserve a escala
Quando for imprimir, use
folhas A4 e desabilite a
função "Fit to paper"

Respeite o Meio Ambiente.
Imprima somente o ne-
cessário

BA-10

Balcão de distribuição granito

(L=350cm)

Obs.: Este componente deve receber o Balcão térmico fixo (BT-02).
Utilizar o serviço 16.06.103
Instalação de Balcão térmico fixo (BT-02)

Revisão 8
Data 17/02/25

Página
10/11

Código de listagem

05.05.089



Atenção
Preserve a escala
Quando for imprimir, use folhas A4 e desabilite a função "Fit to paper"

Respeite o Meio Ambiente.
Imprima somente o necessário

DESCRIÇÃO

Constituintes

- Estrutura do balcão:
 - Concreto usinado, fck 30MPa;
 - Alvenaria estrutural em bloco de concreto classe B, de 14x19x39cm, conforme ficha S7.03 do Catálogo de Serviços;
 - Concreto graute (Pilaretes);
 - Armação com aço CA50 e CA60.

Obs.: Preferencialmente, deverá ser utilizado cimento CP-III ou CP-IV, sempre que possível.

- Tampo de granito cinza andorinha ou cinza corumbá (e=2cm), com testeira, conforme detalhes.
- Revestimento em azulejos branco, conforme ficha S11.01 do Catálogo de Serviços.
- Porta basculante de acionamento manual, composta de:
 - Sistema completo de contrapeso para acionamento manual, de acordo com o fabricante;
 - Caixa lateral para o contrapeso em chapa dobrada de aço galvanizado, nº 16 (e=1,55mm) e dimensões de acordo com o fabricante;
 - Travessa superior em chapa dobrada de aço galvanizado, nº 16 (e=1,55mm) e dimensões de acordo com o fabricante;
 - Folha da porta constituída de:
 - » chapa lisa de aço galvanizado, nº 16 (e=1,55mm)
 - » requadro em tubo de aço galvanizado a fogo (40x80mm, e=1,2mm);
 - » montantes verticais em tubo de aço galvanizado a fogo (40x40mm, e=1,2mm);
 - » mata-juntas em perfis "L" (1/2" x 1/8") e barra chata (3,18mm e=3mm);
 - » fita vedadora ("escova") com base rígida de polipropileno e fios semiflexíveis, para vedação da fresta no trecho junto ao eixo de basculação onde não existe mata-junta e na parte inferior junto à bancada.
 - Protetor para o trilho e trava para o portão na posição aberto: chapa dobrada de aço galvanizado, e=1,2mm, conforme detalhe;
 - Porta-cadeados em chapa de aço galvanizado a fogo, e=3mm.
 - Niple roscável de 3/4", conectado ao ponto de água fria.
 - Conjunto de esgotamento, composto por:
 - » Sifão ajustável em polipropileno com entrada de 1 1/2", saída de 50mm e comprimento total de 660mm, conectado ao ponto de esgoto;
 - » Bucha de redução roscável de 1 1/2" X 3/4", conectada à entrada do sifão.
 - » Niple roscável de 3/4", conectado à bucha de redução.

Acessórios

- Cadeado de latão maciço, de 35mm, com dupla trava, para a porta (2 unidades).
- Cadeado de latão maciço, de 25mm, com dupla trava, para o protetor do trilho (2 unidades).

Acabamento

- Porta basculante: pintura esmalte sobre fundo para galvanizados, na cor especificada em projeto.

Protótipo comercial

- Sifão ajustável:
 - PLENA.
 - AMANCO.
- Nipples e bucha de redução:
 - TIGRE.

APLICAÇÃO

- Em Cozinhas.

Obs.:

- Em pavimento térreo, o consolo junto à viga baldrame deverá constar do projeto de estrutura;
- Em pavimento superior, o projeto estrutural deverá indicar a solução alternativa.

EXECUÇÃO

- A estrutura do balcão deve ser executada, de acordo com o especificado, respeitando-se rigorosamente as dimensões indicadas para não comprometer o encaixe perfeito do Balcão térmico fixo (BT-02).
 - O tampo de granito deve apresentar bordas boleadas externamente e, internamente (nicho do balcão térmico), bordas retas (90°).
 - O assentamento do tampo e testeira de granito deverá ser executado com argamassa colante.
 - A alvenaria deve ser revestida internamente em azulejo branco conforme ficha de serviços S11.01 Azulejos e externamente com o revestimento especificado em projeto para o refeitório.
 - Para assentamento dos azulejos, ver ficha correspondente no Catálogo de Serviços.
 - O sistema de esgotamento deve ser instalado conforme Anexo I - Orientações para instalação, constante na ficha de mobiliário do Balcão térmico fixo (BT-02).
- Obs.:** Ver Anexo I - Orientações para instalação, constante na ficha de mobiliário do Balcão térmico fixo (BT-02).

FICHAS DE REFERÊNCIA

Catálogo de Mobiliário

Ficha BT-02 Balcão térmico fixo

Catálogo de Componentes

Ficha BA-11 Balcão de devolução granito (L=70cm)
Ficha BA-12 Balcão de atendimento granito (210x60cm)
Ficha BA-13 Balcão de atendimento granito (150x60cm)
Ficha BS-05 Bancada para cozinha

Catálogo de Serviços

Ficha S4.03 Concreto dosado em central
Ficha S4.04 Concreto Grout
Ficha S7.03 Alvenaria estrutural de bloco de concreto (classe A e B)
Ficha S11.01 Azulejos
Ficha S14 Pintura
Ficha S14.09 Tinta esmalte sintético *standard*
Ficha S14.17 Galvanização
Ficha S14.21 Tinta esmalte à base de água
Ficha H2.06 Tubos e conexões de PVC rígido (água fria)
Ficha H4.04 Tubos e conexões de PVC rígido (esgoto)
Ficha E4.10 Tomada de parede industrial 32A 220V - IP65

RECEBIMENTO

- O serviço pode ser recebido se atendidas todas as condições de projeto, fornecimento e execução.
- Tampo de granito:
 - Verificar as dimensões, principalmente do nicho onde será encaixado o balcão térmico (tolerâncias admissíveis: largura e profundidade +10mm e espessura +1mm);
 - Verificar o acabamento das bordas: boleadas externamente e internamente (nicho do balcão térmico) bordas retas, a 90°. Não deve apresentar arestas quebradas;
 - Verificar o nível em duas direções ortogonais, com nível de bolha;

- Verificar o acabamento superficial, as juntas em nível e o polimento;
- Verificar a cola entre o tampo e a testeira.
- Porta basculante:
 - Exigir certificado de garantia da porta completa, emitido pelo fabricante;
 - Não será aceita porta com rebarbas, empenada, desnívelada, fora de prumo ou de esquadro, ou que apresente quaisquer defeitos decorrentes do manuseio, transporte ou instalação;
 - Verificar se as soldas nos tubos estão contínuas em toda a extensão da superfície de contato;
 - Verificar a aderência e a uniformidade da camada de pintura, atentando para que não apresentem falhas, bolhas, irregularidades ou quaisquer defeitos decorrentes da fabricação e do manuseio;
 - O funcionamento do portão deverá ser verificado após a completa secagem da pintura e subsequente lubrificação, não podendo haver jogo causado por folgas, nem dificuldade no seu deslizamento. O seu funcionamento deverá ser fácil e quando a folha estiver em posição semi-aberta, deverá permanecer parada.
- Instalações hidráulicas:
 - Verificar a instalação do conjunto de esgotamento considerando, sifão, bucha e niple.
 - Verificar a instalação do niple para abastecimento de água fria.

SERVIÇOS INCLUÍDOS NOS PREÇOS

- Estrutura do balcão: alvenaria em bloco de concreto estrutural, pilaretes grauteados e tampo de concreto (o consolo deve ser indicado no projeto estrutural e será pago em outros serviços).
- Tampo de granito.
- Azulejos (apenas na alvenaria de apoio lateral)
- Porta basculante completa, executada e instalada.
- Pintura na porta basculante com esmalte, incluindo fundo para galvanizado e galvanização a frio.

Obs.: Instalações elétricas e hidráulicas serão pagas em outros serviços.

CRITÉRIOS DE MEDIÇÃO

- un. — por unidade executada.

LEGISLAÇÃO

- Portaria CVS-05, de 09/04/2013, do Centro de Vigilância Sanitária - Secretaria de Estado da Saúde de São Paulo
- Aprova regulamento técnico sobre boas práticas para estabelecimentos comerciais de alimentos e para serviços de alimentação.

NORMAS

- ABNT NBR 9050:2020 (versão corrigida 2021) – Acessibilidade a edificações, mobiliário, espaços e equipamentos urbanos

Obs: As edições indicadas estavam em vigor no momento desta publicação. Como toda norma está sujeita a revisão, recomenda-se verificar a existência de edições mais recentes das normas citadas.

Componentes

BA-10

Balcão de distribuição granito

(L=350cm)

Obs.: Este componente deve receber o Balcão térmico fixo (BT-02). Utilizar o serviço 16.06.103 Instalação de Balcão térmico fixo (BT-02)

Revisão 8
Data 17/02/25

Página

11/11

Código de listagem

05.05.089



Atenção

Preserve a escala
Quando for imprimir, use folhas A4 e desabilite a função "Fit to paper"

Respeite o Meio Ambiente.
Imprima somente o necessário