

BA-11

**Balcão de
devolução
granito**
(L=70cm)



Revisão 5
Data 30/09/21

Página
1/5


Código de listagem

05.05.090




Atenção
Preserve a escala
Quando for imprimir, use
folhas A4 e desabilite a
função "Fit to paper"

Respeite o Meio Ambiente.
Imprima somente o ne-
cessário

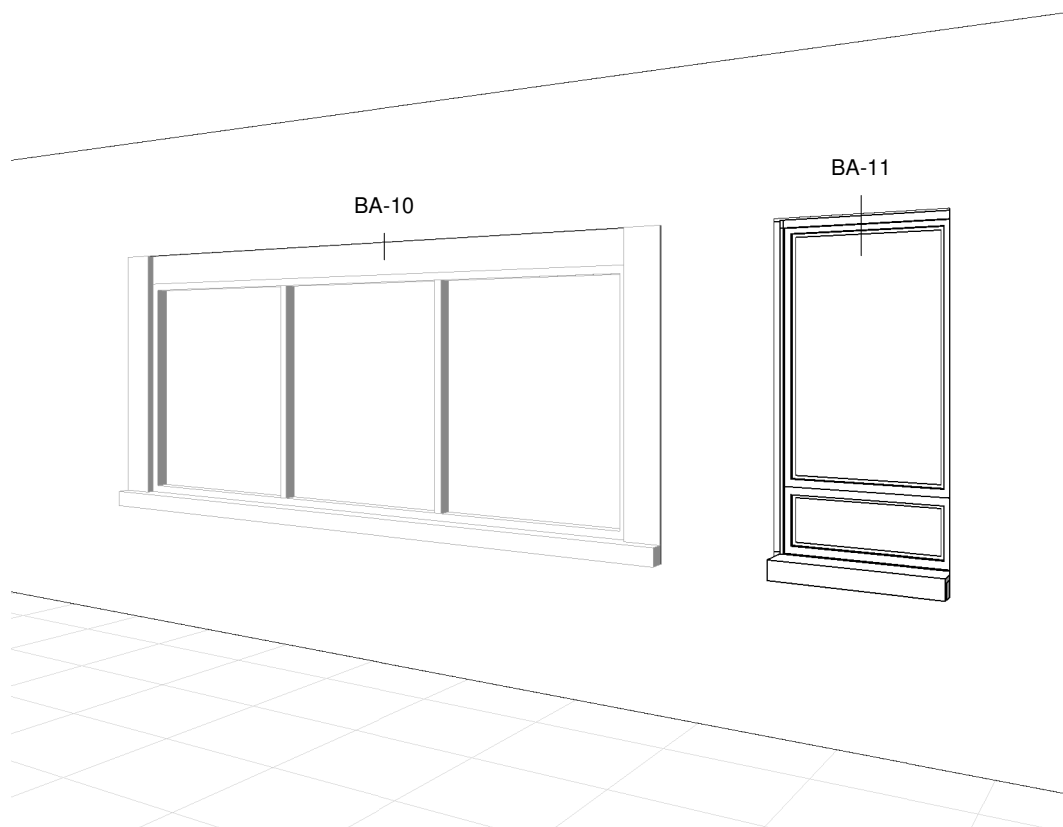


EXEMPLO DE COMPOSIÇÃO BA-11 E BA-10 - VISTA EXTERNA

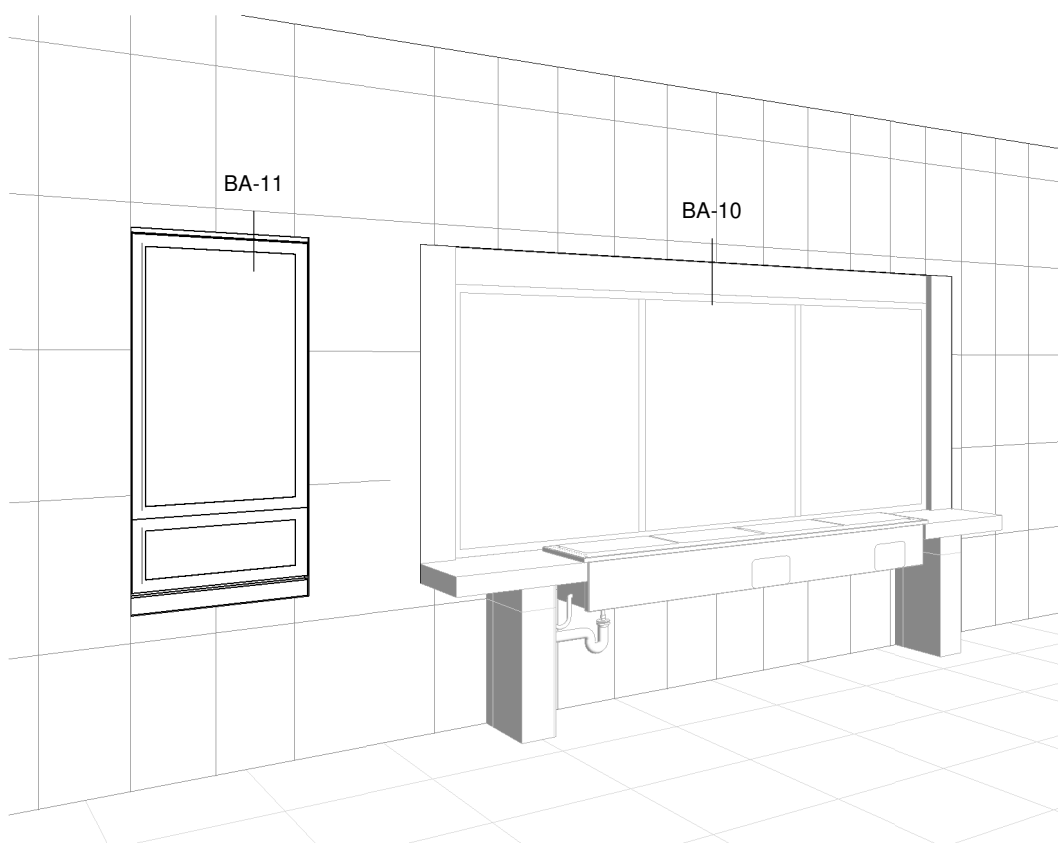


EXEMPLO DE COMPOSIÇÃO BA-11 E BA-10 - VISTA INTERNA

BA-11


Balcão de
devolução
granito
(L=70cm)

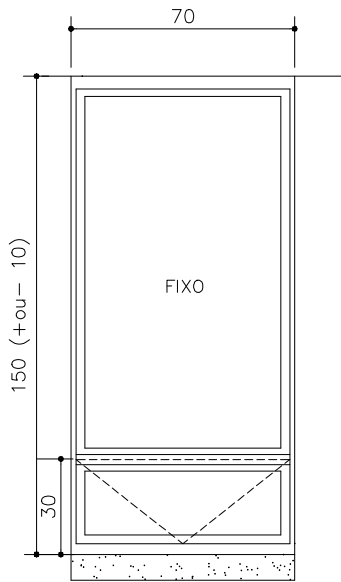

VISTA 1 EXTERNA
ESCALA 1:25

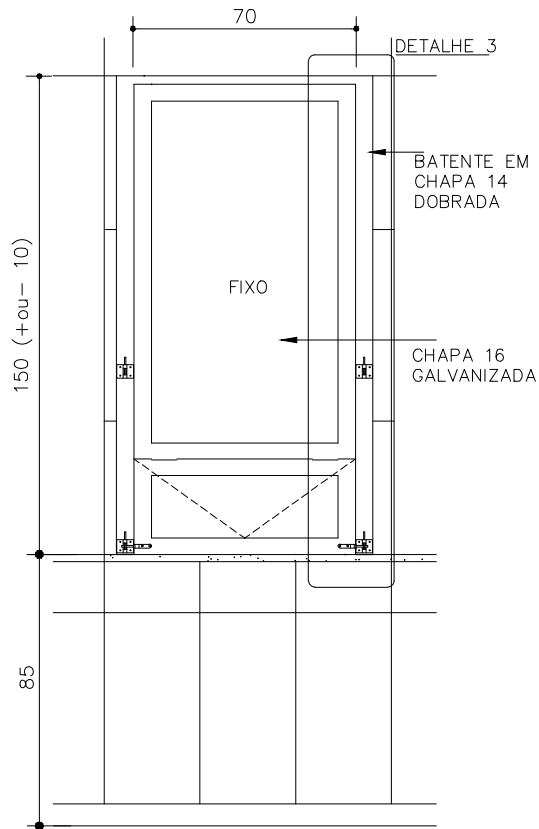

VISTA 2 INTERNA
ESCALA 1:25

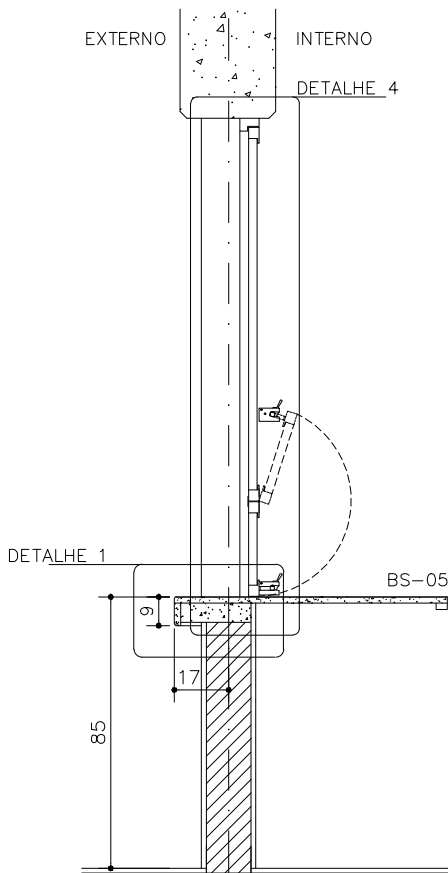

CORTE A-A
ESCALA 1:25

Revisão 5
Data 30/09/21

Página
2/5


Código de listagem

05.05.090



Atenção
Preserve a escala
Quando for imprimir, use
folhas A4 e desabilite a
função "Fit to paper"

Respeite o Meio Ambiente.
Imprima somente o ne-
cessário

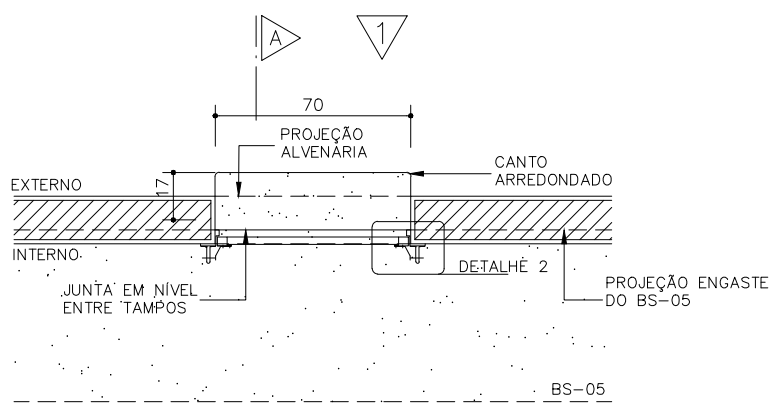

PLANTA
ESCALA 1:25

BA-11

**Balcão de
devolução
granito**
(L=70cm)



Revisão 5
Data 30/09/21

Página
3/5


Código de listagem

05.05.090




Atenção
Preserve a escala
Quando for imprimir, use
folhas A4 e desabilite a
função "Fit to paper"


Respeite o Meio Ambiente.
Imprima somente o ne-
cessário

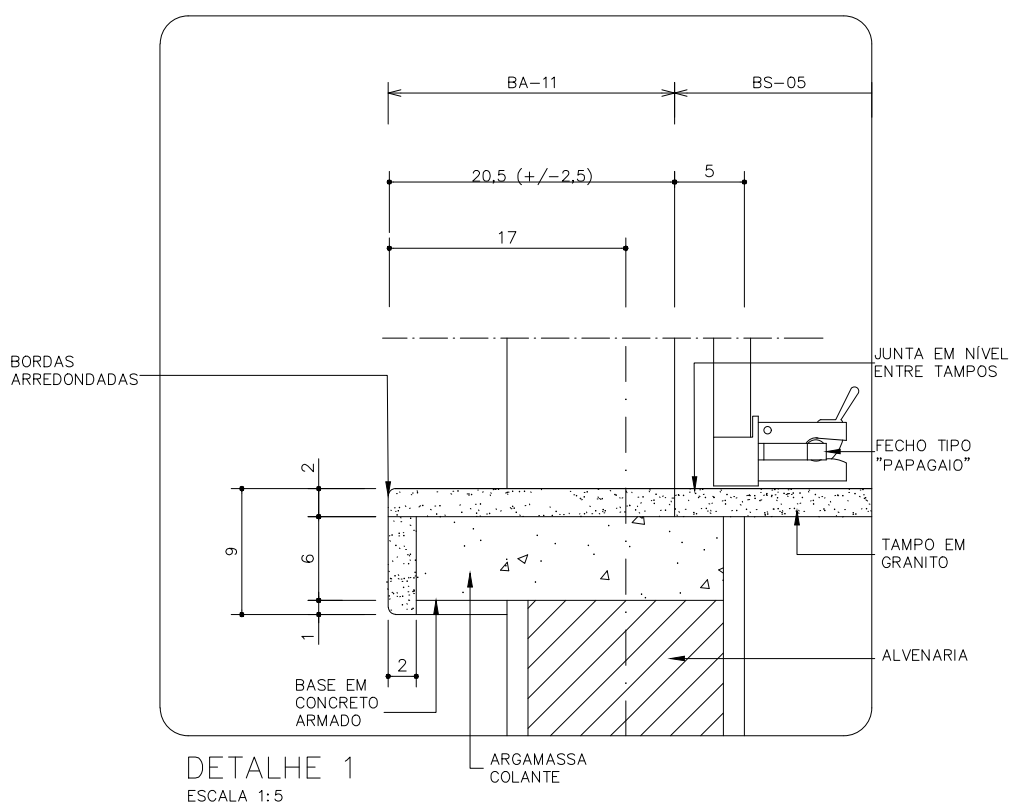

DETALHE 1
ESCALA 1:5

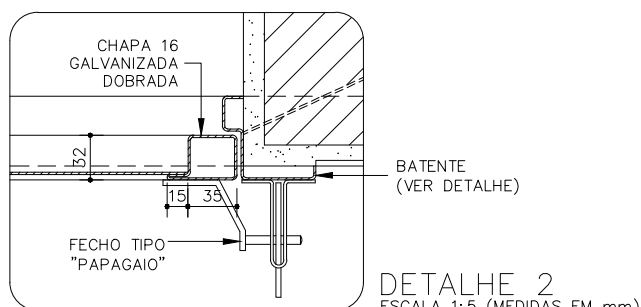

DETALHE 2
ESCALA 1:5 (MEDIDAS EM mm)

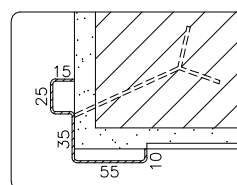

DETALHE BATENTE
ESCALA 1:5 (MEDIDAS EM mm)

BA-11

Balcão de
devolução
granito
(L=70cm)



Revisão 5
Data 30/09/21

Página
4/5


Código de listagem

05.05.090




Atenção
Preserve a escala
Quando for imprimir, use
folhas A4 e desabilite a
função "Fit to paper"

Respeite o Meio Ambiente.
Imprima somente o ne-
cessário

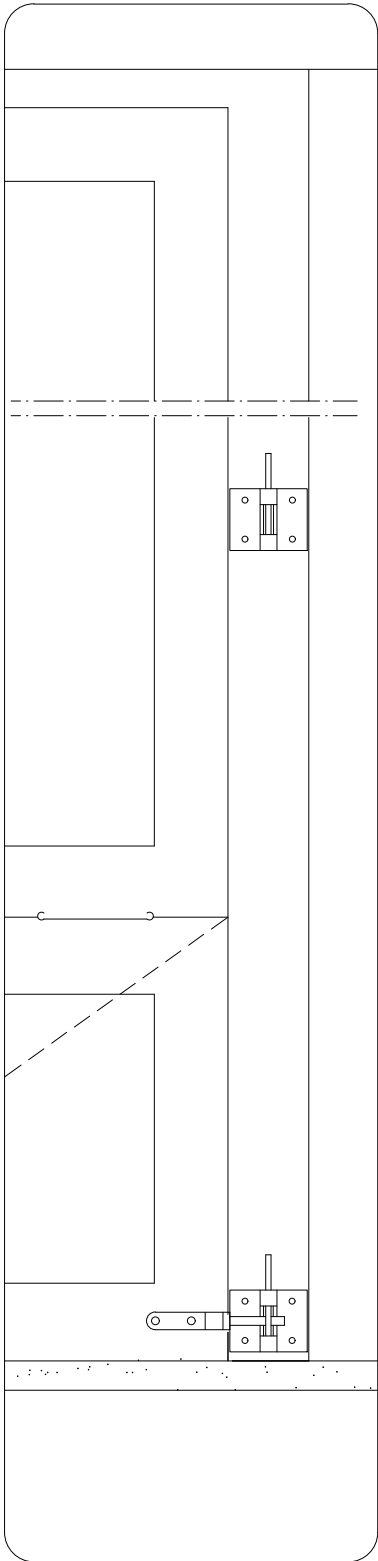

DETALHE 3
ESCALA 1:5

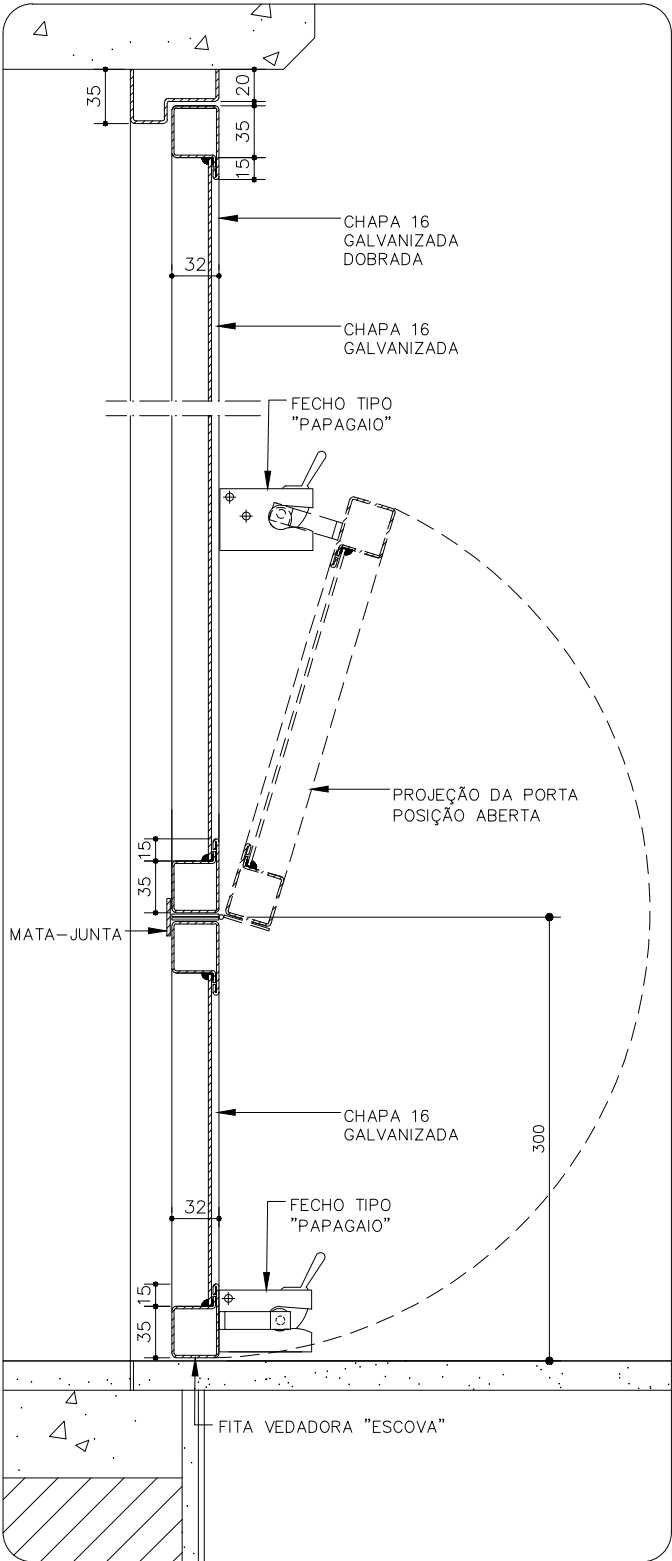

DETALHE 4
ESCALA 1:5

DESCRIÇÃO

Constituintes

- Base em concreto armado para apoio do tampo de granito:
 - Concreto usinado, fck 20MPa;
 - Armação em aço CA60, Ø=4,2mm, malha 5 x 5cm.
 - **Obs.:** Preferencialmente, deverá ser utilizado cimento CP-III ou CP-IV, sempre que possível.
- Tampo de granito cinza andorinha ou cinza corumbá (e=2cm), com testeira, conforme Detalhe 01.
- Porta:
 - Batente em chapa 14 (1,9mm), galvanizada, dobrada;
 - Perfis em chapa 16 (1,6mm), galvanizada, dobrada;
 - Chapa 16 (1,6mm), galvanizada, lisa;
 - Mata-junta em barra chata (3,18mm, e=3mm), galvanizada;
 - Galvanização a frio nos pontos de corte e solda.
 - Fita vedadora ("escova") na face inferior junto à bancada.

Acessórios

- Dobradiça de aço, cromado, com pino e bolas, 3" x 2 1/2" (2 unidades).
- Fecho "papagaio", em aço galvanizado, 4 unidades (Protótipo comercial: SOPRANO).

Acabamento

- Porta: pintura esmalte sobre fundo para galvanizados, na cor especificada em projeto.

APLICAÇÃO

- Em Cozinhas, onde se utilizar o componente BA-10 (balcão de distribuição).
- **Obs.:** Uso em conjunto com o componente BS-05 (bancada para cozinha).

EXECUÇÃO

- A base de concreto do balcão deve ser executada, de acordo com o especificado.
- O tampo de granito deve apresentar bordas e cantos boleados.
- O assentamento do tampo e testeira de granito deverá ser executado com argamassa colante.
- Porta:
 - A esquadria deve ser montada com perfis previamente galvanizados;
 - Bater os pontos de solda e eliminar todas as rebarbas nas emendas e cortes dos perfis;
 - Os pontos de solda e corte devem ser tratados com galvanização a frio (tratamento anticorrosivo composto de zinco);
 - Antes da aplicação do fundo para galvanizados, toda superfície metálica deve estar completamente limpa, seca e desengraxada.
- Internamente (Cozinha), a alvenaria deve ser revestida com azulejo branco, conforme ficha S11.01 do Catálogo de Serviços.
- Externamente, a alvenaria deve receber revestimento do Refeitório, conforme especificado em projeto.

FICHAS DE REFERÊNCIA

Catálogo de Componentes

- Ficha BA-10 Balcão de distribuição granito (L=350)
- Ficha BA-12 Balcão de atendimento granito (210x60cm)
- Ficha BA-13 Balcão de atendimento granito (150x60cm)
- Ficha BS-05 Bancada para cozinha

Catálogo de Serviços

- Ficha S11.01 Azulejos

- Ficha S14.09 Tinta esmalte sintético standard
- Ficha S14.17 Galvanização
- Ficha S14.21 Tinta esmalte à base de água

RECEBIMENTO

- O serviço pode ser recebido se atendidas todas as condições de projeto, fornecimento e execução.
- Tampo de granito:
 - Verificar dimensões (tolerâncias admissíveis):
 - » largura: $\pm 10\text{mm}$
 - » espessura: $\pm 1\text{mm}$;
 - Verificar o acabamento boleado nas bordas e cantos; não devendo apresentar arestas quebradas;
 - Verificar o nível em duas direções ortogonais, com nível de bolha;
 - Verificar o acabamento superficial, o polimento e a junta em nível com o componente BS-05;
 - Verificar a cola entre o tampo e a testeira.
- Porta:
 - Não será aceita porta com rebarbas, empenada, desnívelada, fora de prumo ou de esquadro, ou que apresente quaisquer defeitos decorrentes do manuseio, transporte ou instalação;
 - Verificar se as soldas nos tubos estão contínuas em toda a extensão da superfície de contato;
 - Verificar a aderência e a uniformidade da camada de pintura, atentando para que não apresentem falhas, bolhas, irregularidades ou quaisquer defeitos decorrentes da fabricação e do manuseio;
 - O funcionamento da porta deverá ser verificado após a completa secagem da pintura e subsequente lubrificação, não podendo haver jogo causado por folgas. O seu funcionamento deverá ser fácil e o encaixe nos fechos "papagaio" deverá ser perfeito.

SERVIÇOS INCLUÍDOS NOS PREÇOS

- Tampo de granito e base de concreto.
- Porta completa, executada e instalada.
- Pintura da porta com tinta esmalte, incluindo galvanização a frio e fundo para galvanizados.
- **Obs.:** Revestimento em azulejos será pago em outro serviço.

CRITÉRIOS DE MEDIÇÃO

- un. — por unidade executada.

LEGISLAÇÃO

- Portaria CVS-05, de 09/04/2013, do Centro de Vigilância Sanitária - Secretaria de Estado da Saúde de São Paulo
- Aprova regulamento técnico sobre boas práticas para estabelecimentos comerciais de alimentos e para serviços de alimentação.

NORMAS

- NBR 9050:2015 – Acessibilidade a edificações, mobiliário, espaços e equipamentos urbanos
- **Obs:** As edições indicadas estavam em vigor no momento desta publicação. Como toda norma está sujeita a revisão, recomenda-se verificar a existência de edições mais recentes das NORMAS citadas.

Componentes

BA-11

Balcão de devolução granito

(L=70cm)



Revisão 5
Data 30/09/21

Página
5/5

Código de listagem

05.05.090



Atenção

Preserve a escala
Quando for imprimir, use folhas A4 e desabilite a função "Fit to paper"

Respeite o Meio Ambiente.
Imprima somente o necessário