


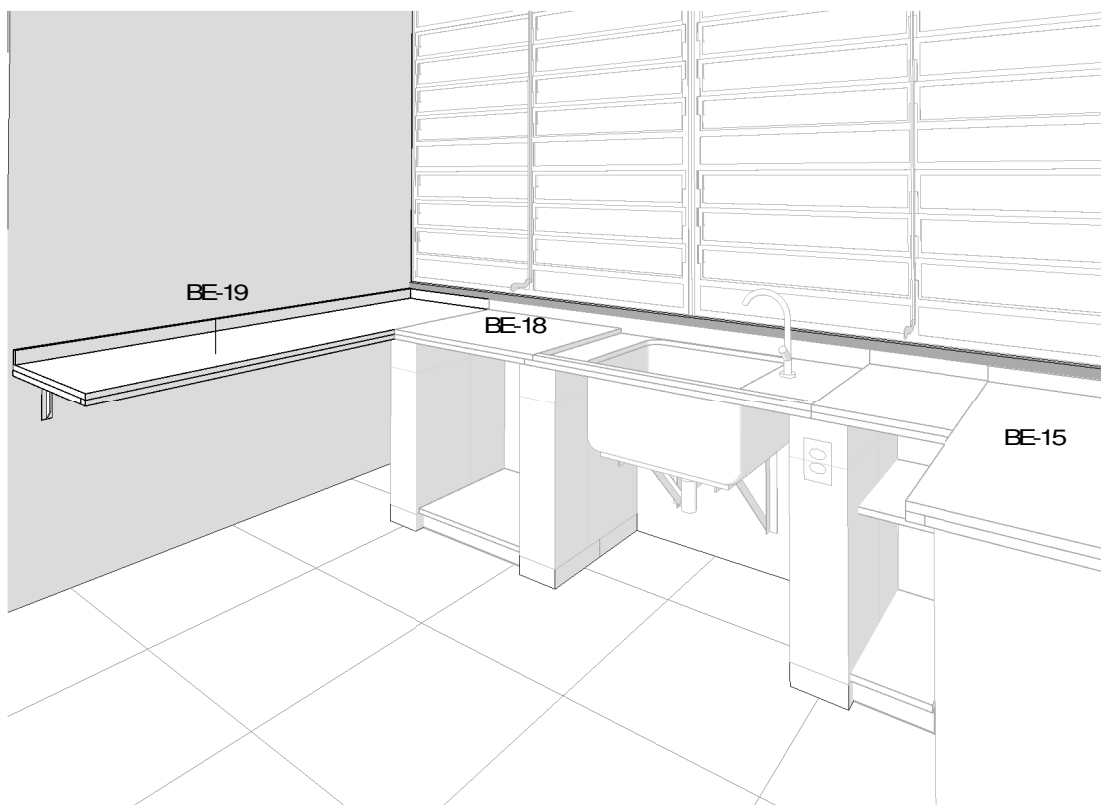




BE-19

**Bancada
laboratório
simples**

EXEMPLOS DE COMPOSIÇÃO

ESCALA 1:75

EXEMPLO 1

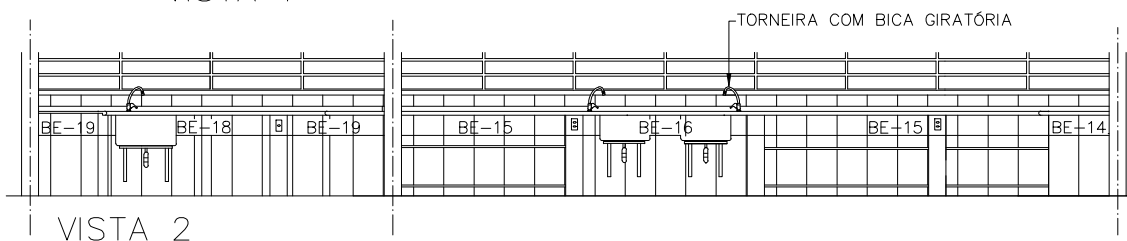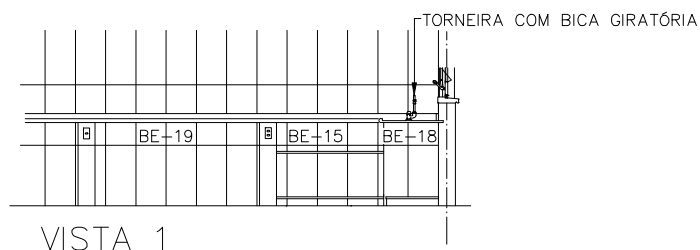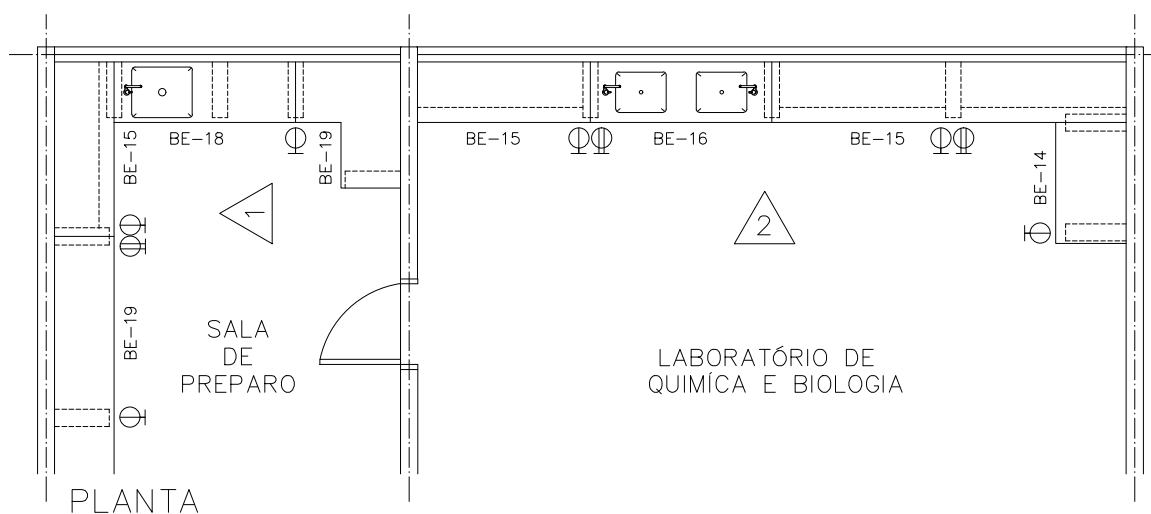

Revisão 2
Data 30/09/21

Página
1/4

Código de listagem

05.05.069



Atenção


Preserve a escala
Quando for imprimir, use
folhas A4 e desabilite a
função "Fit to paper"

Respeite o Meio Ambiente.
Imprima somente o ne-
cessário

BE-19

Bancada
laboratório
simples

EXEMPLO 2

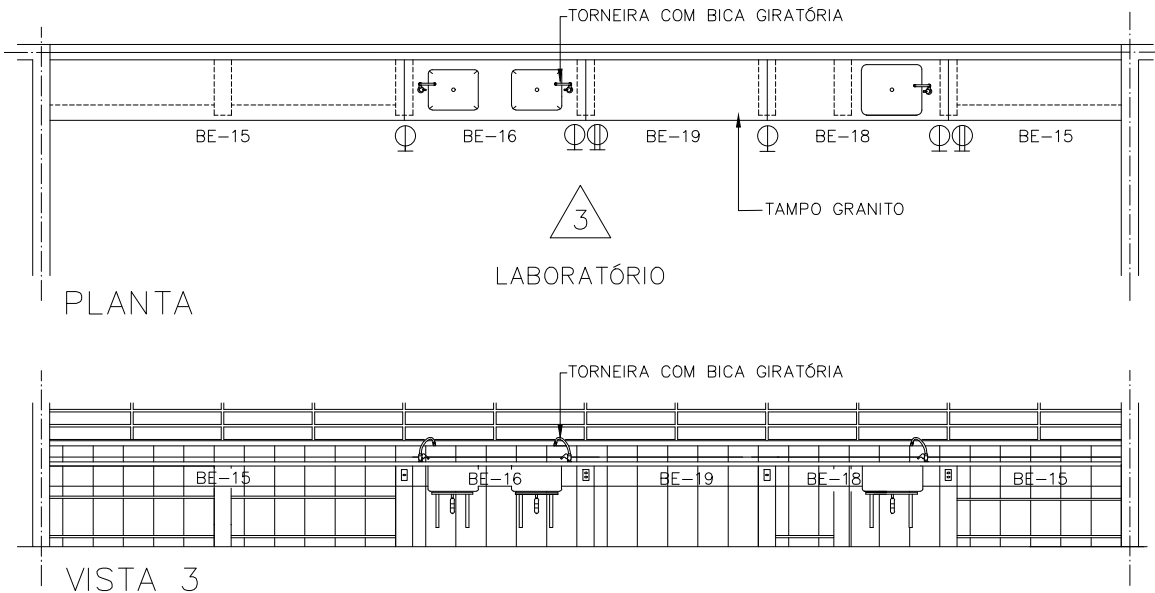

Revisão 2
Data 30/09/21

Página
2/4

Código de listagem

05.05.069



Atenção
Preserve a escala
Quando for imprimir, use
folhas A4 e desabilite a
função "Fit to paper"

Respeite o Meio Ambiente.
Imprima somente o ne-
cessário

BE-19

Bancada
laboratório
simples

Revisão 2
Data 30/09/21

Página
3/4

Código de listagem

05.05.069






Atenção


Preserve a escala
Quando for imprimir, use
folhas A4 e desabilite a
função "Fit to paper"

Respeite o Meio Ambiente.
Imprima somente o ne-
cessário


FDE FUNDAÇÃO PARA O
DESENVOLVIMENTO
DA EDUCAÇÃO

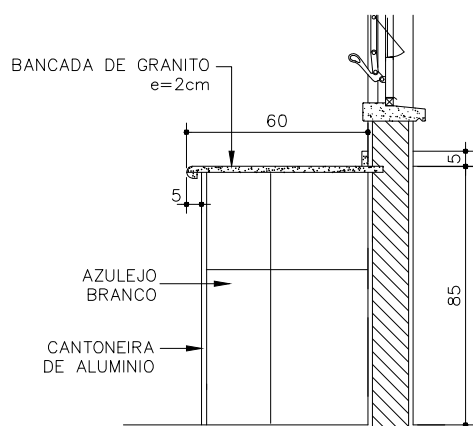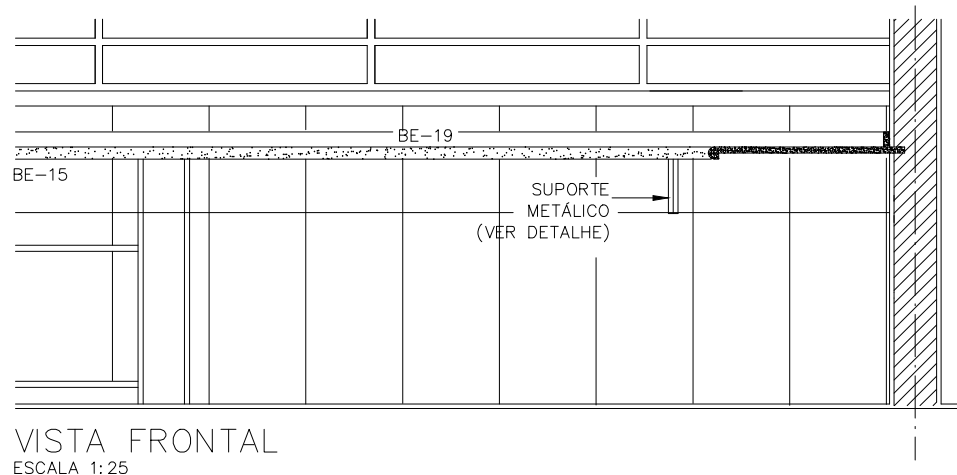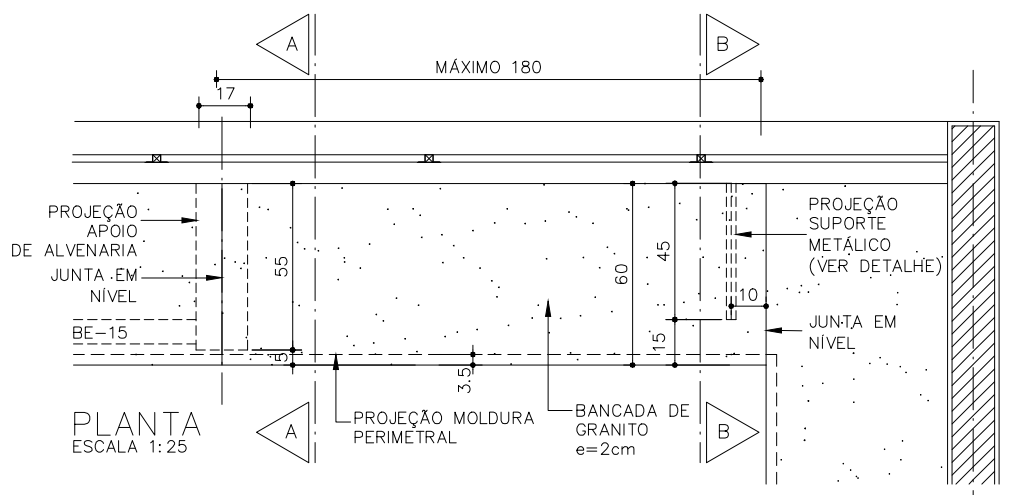

CORTE AA
ESCALA 1:25

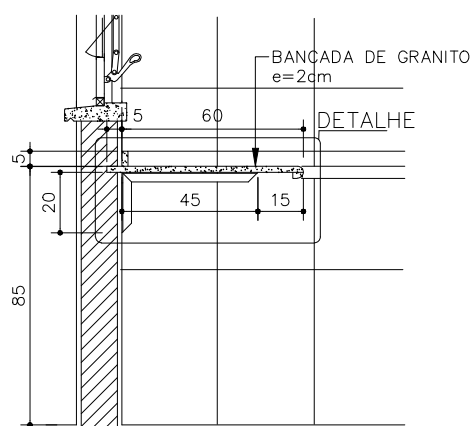

CORTE BB
ESCALA 1:25

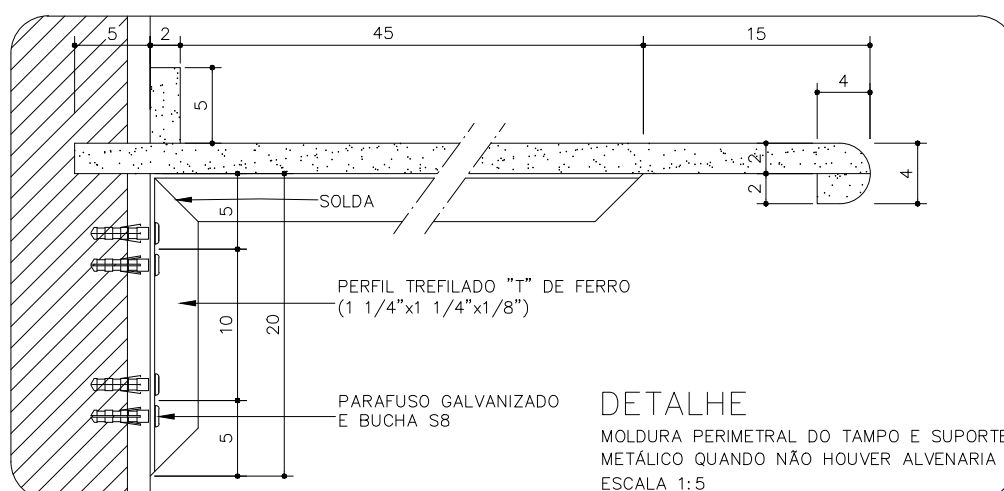

BE-19

Bancada
laboratório
simples

Revisão 2
Data 30/09/21

Página
4/4

Código de listagem

05.05.069



Atenção
Preserve a escala
Quando for imprimir, use
folhas A4 e desabilite a
função "Fit to paper"

Respeite o Meio Ambiente.
Imprima somente o ne-
cessário

DESCRIÇÃO

Constituintes

- Tampo de granito polido (L=65cm, e=2cm), cinza andorinha ou cinza corumbá, com moldura perimetral (3,5x2cm) e frontão (5x2cm), conforme detalhe 1.
- Alvenaria de apoio em bloco de concreto classe C (e=14cm), revestida com azulejos brancos, conforme ficha S11.01 do Catálogo de Serviços.
- **Obs.:**
 - Instalações elétricas, conforme projeto de elétrica, serão pagas em outros serviços:
 - » tomadas 110V e 220V, em caixas 4"x2", conforme ficha E4.06;
 - » se não houver outra indicação em projeto, instalar as tomadas na altura de 70cm do piso acabado, conforme sugerido nos desenhos.

Protótipo comercial

- Azulejos, argamassa de assentamento e pasta de rejunte: ver ficha S11.01 do Catálogo de Serviços.

APLICAÇÃO

- Sala de preparo, vinculada ao laboratório de química e biologia e ao laboratório de matemática e física, conforme especificado em projeto.

EXECUÇÃO

- Antes da execução do revestimento do piso da sala, executar as alvenarias de apoio e o ressalto da base, conforme dimensões e especificações em desenho.
- Executar as instalações elétricas, e inclusive caixas das tomadas, conforme projeto executivo de elétrica.
- Tampo de granito:
 - Deve ser engastado na alvenaria posterior e na alvenaria lateral (quando houver), e sobreposto nos apoios de alvenaria;
 - Junto à alvenaria posterior, o arremate deve ser efetuado com frontão.
- Executar o revestimento com azulejo, conforme indicado em desenho, seguindo instruções dos fabricantes e ficha S11.01 do Catálogo de Serviços.
- Finalizar instalações elétricas, colocando espelhos e acessórios complementares nas tomadas.

FICHAS DE REFERÊNCIA

Catálogo de Componentes

Ficha	BE-06	Bancada alunos/ química e biologia (L=540cm)
Ficha	BE-07	Bancada alunos/ química e biologia (L=900cm)
Ficha	BE-14	Bancada apoio para a capela
Ficha	BE-15	Bancada laboratório com prateleira
Ficha	BE-16	Bancada laboratório/ 2 cubas 50x40x25cm (L=180cm)
Ficha	BE-17	Bancada laboratório/ 1cuba 50x40x25cm (L=120cm)
Ficha	BE-18	Bancada laboratório/ 1cuba 60x50x30cm (L=180cm)

Catálogo de Serviços

Ficha	E2.04	Eletrodutos e conexões de PVC rígido roscável
Ficha	E2.06	Fios e cabos elétricos
Ficha	E4.06	Tomadas de parede
Ficha	S7.03	Alvenaria de bloco de concreto (classe C)
Ficha	S11.01	Azulejos
Ficha	S11.02	Cantoneira de alumínio

RECEBIMENTO

- O serviço pode ser recebido se atendidas todas as condições de projeto, fornecimento e execução.
- Aferir as especificações e a conformidade com os protótipos homologados.
- Tampo de granito:
 - Verificar dimensões (tolerâncias admissíveis):
 - » largura: $\pm 10\text{mm}$;
 - » espessura: $\pm 1\text{mm}$.
 - Nível: verificar em duas direções ortogonais com nível de bolha;
 - Verificar o polimento, não devendo haver arestas vivas;
 - Verificar entre tampos a cola entre o tampo e a moldura perimetral;
 - Verificar o rejuntamento entre tampos e a limpeza das superfícies.
- Alvenaria de apoio:
 - Verificar dimensões. Tolerância admissível de $\pm 50\text{mm}$ entre os eixos.
- Azulejos:
 - Verificar prumo, alinhamento, superfície.
 - Verificar os rejuntamentos e a limpeza das superfícies.
- Serviços elétricos:
 - Atendidas as condições especificadas em projeto e descritas nas fichas de referência, verificar a tensão fornecida e o funcionamento das tomadas.

SERVIÇOS INCLUÍDOS NOS PREÇOS

- Alvenaria de apoio.
- Azulejos, apenas na alvenaria de apoio.
- Tampo de granito.
- **Obs.:** as instalações elétricas, inclusive tomadas, serão pagas em outros serviços.

CRITÉRIOS DE MEDIÇÃO

- m — por comprimento executado