



PLANTA
ESC. 1:25




VISTA 1 (SEM ESCALONAMENTO)
ESC. 1:25

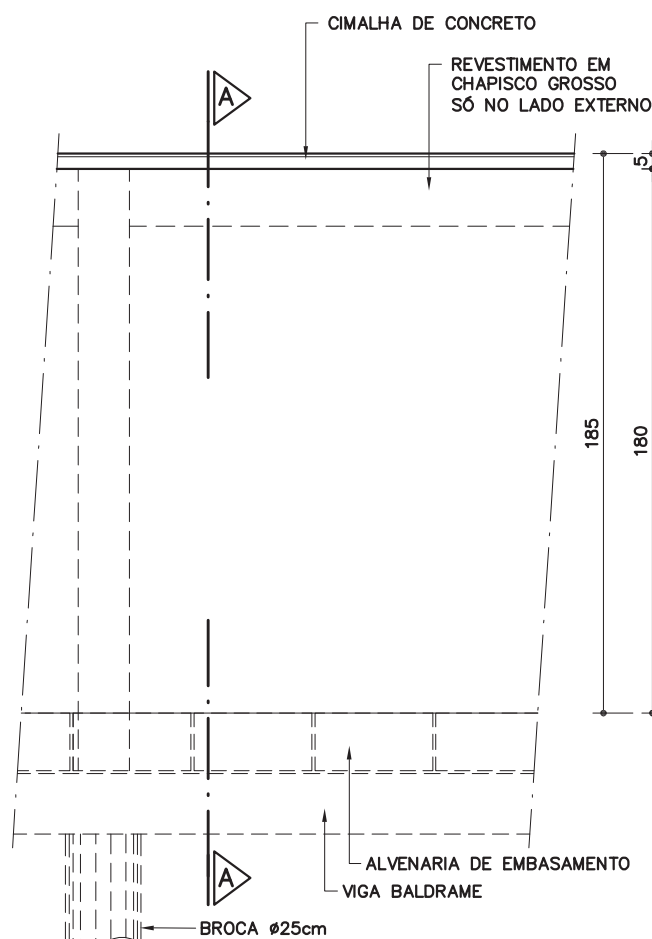


CORTE AA
ESC. 1:25

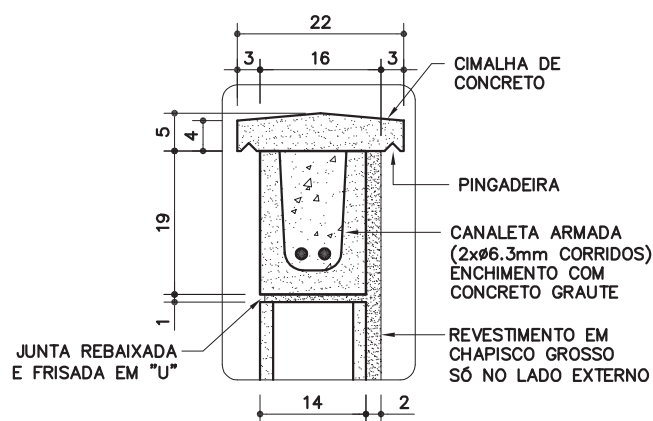

DET. 01
ESC. 1:10

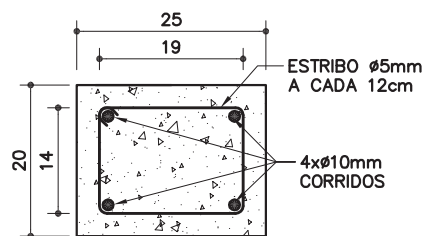

VIGA BALDRAME
ESC. 1:10

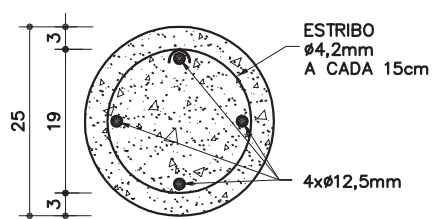

BROCA
ESC. 1:10

FD-08

**Fechamen-
to divisa/
bloco de
concreto /
rev. chapis-
co grosso**

revestimento
apenas na face
externa
(h=185cm / broca)

Revisão	6
Data	20/03/19

Página

 $\frac{1}{3}$ **Código de listagem**

1601009



Atenção

Preserve a escala
Quando for imprimir, use folhas A4 e desabilite a função "Fit to paper"

Respeite o Meio Ambiente.
Imprima somente o necessário

FD-08

**Fechamen-
to divisa/
bloco de
concreto /
rev. chapis-
co grosso**

revestimento
apenas na face
externa
[h=185cm / broca]

Revisão	6
Data	20/03/19


Página
2/3

Código de listagem

1601009

EXEMPLOS DE ESCALONAMENTOS

ESC. 1:50

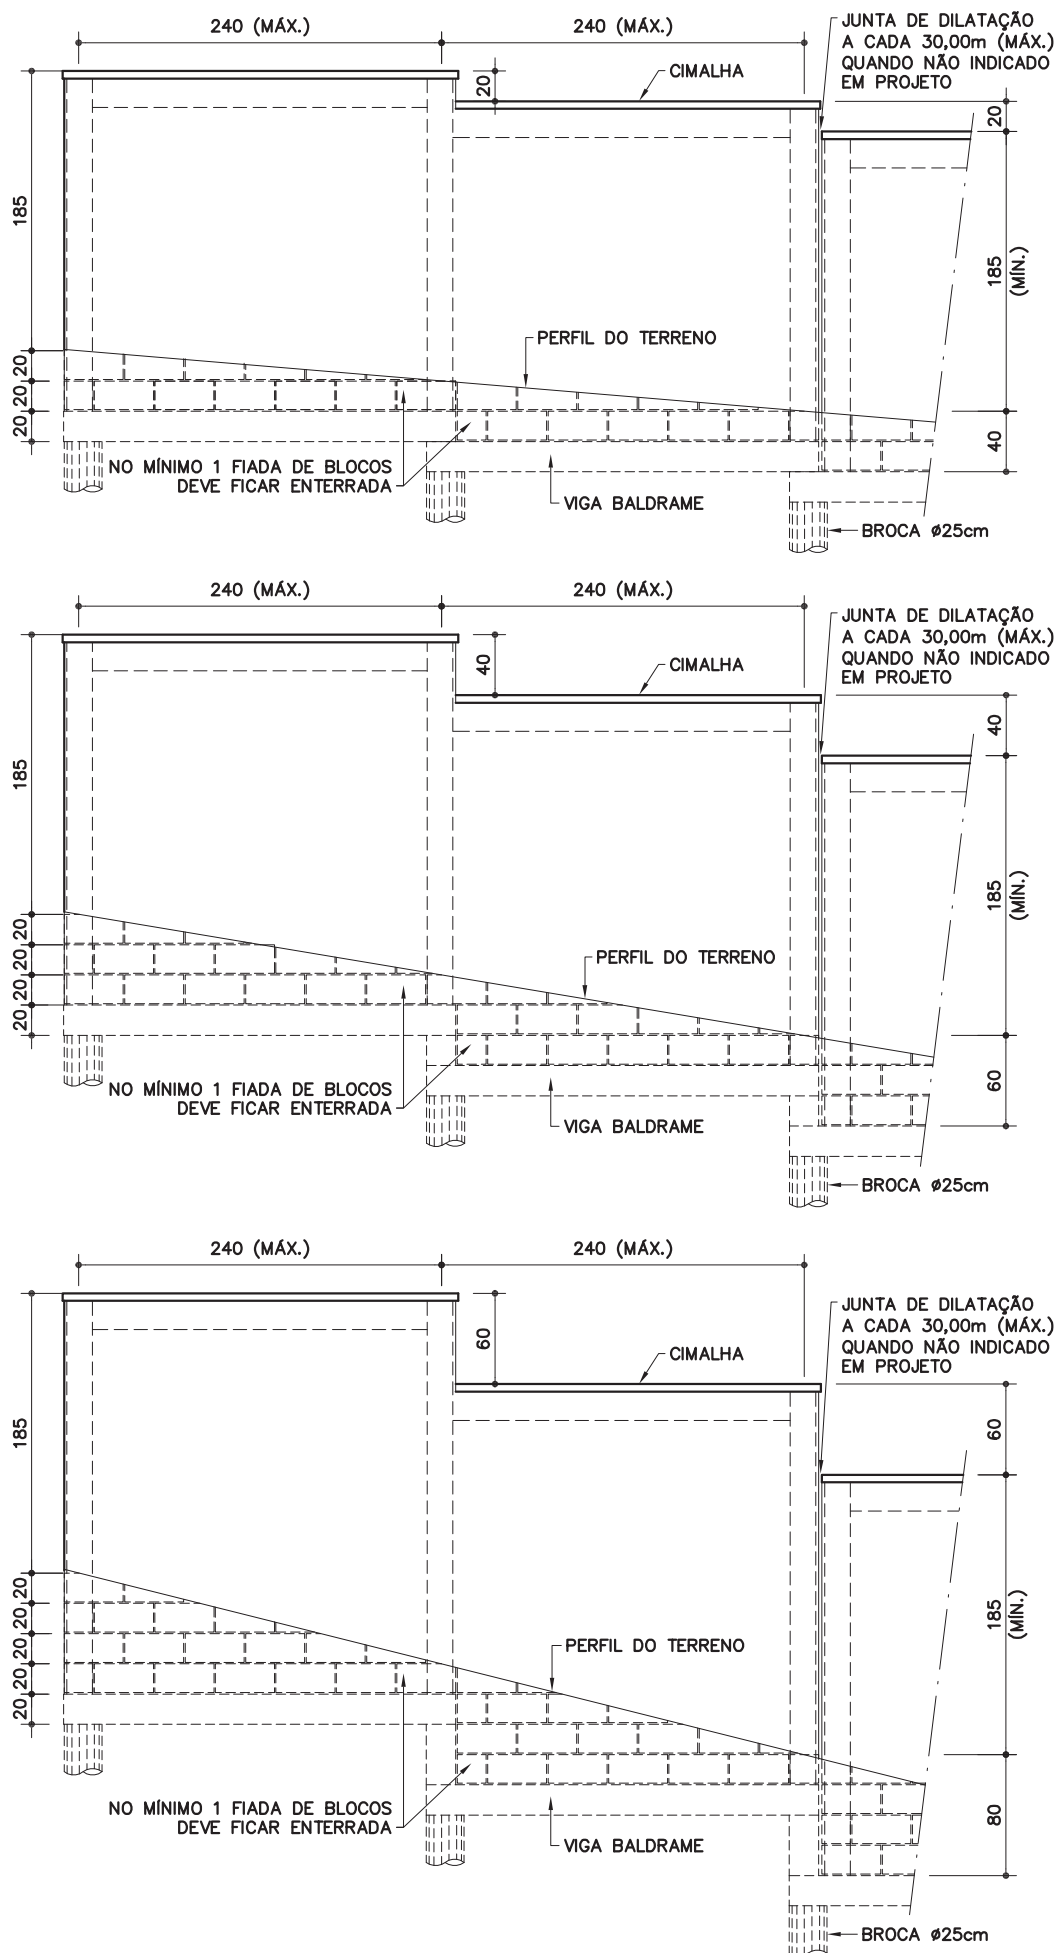

DESCRIÇÃO

Constituintes

- Fundação:
 - Brocas com vigas baldrame;
 - Broca Ø 25cm (armação com aço CA-50: 4 x Ø 12,5mm e estribos Ø 4,2mm a cada 15cm);
 - Viga baldrame 25 x 20cm (armação com aço CA-50: 4 x Ø 10mm corridos e estribos Ø 5mm a cada 12cm);
 - Fôrmas de tábuas de madeira maciça com espessura de 2,5cm (espécies de madeira conforme classificação G1-C2 constante da ficha G1 Gestão de madeira do Catálogo de Serviços);
 - Concreto usinado, fck 25MPa.
- Alvenaria de blocos de concreto, classe C, família M-15, linha 15x40 (14x19x39cm), conforme ficha S7.04 do Catálogo de Serviços.
- Enchimento e armação dos blocos (pilaretes e canaletas):
 - Concreto graute;
 - Armação com aço CA-50 (pilaretes - 4 x Ø 10mm e canaletas - 2 x Ø 6,3mm corridos).
- Cimalha de concreto com pingadeira.
- Impermeabilização rígida, tipo cristalização, na fundação e na alvenaria de embasamento, conforme ficha S10.03 do Catálogo de Serviços.
- Obs.:** Sempre que possível, deverá ser utilizado cimento CP-III ou CP-IV, preferencialmente.

Acabamentos

- Chapisco grosso, somente na face externa.

APLICAÇÃO

- Em divisas de terrenos (onde não há diferença de nível entre os dois terrenos).

EXECUÇÃO

- Escalonar de acordo com a inclinação do terreno (ver exemplos).
- As fôrmas em madeira maciça devem ser executadas com espécie de madeira constante da classificação G1-C2, conforme ficha G1 Gestão de Madeira do Catálogo de Serviços, e produtos adquiridos de empresa cadastrada no CADMADEIRA.
- Prever junta de dilatação de 2 cm a cada 30,00m (no máximo), quando não indicado em projeto.
- Fundação: quando não indicado em projeto, a broca deverá ter profundidade mínima de 2,50m.
- Assentamento dos blocos:
 - Argamassa traço 1: 0,5: 4,5 cimento, cal e areia;
 - O bloco deve ser nivelado, prumado e alinhado durante o assentamento;
 - Executar amarração horizontal dos blocos ao pilarete, a cada 2 fiadas (aço CA-50 de Ø 6,3mm, comprimento = 80cm).
 - Juntas desencontradas (em amarração) com espessura de 1,0 cm. Na face interna da alvenaria (sem revestimento) as juntas devem ser rebaixadas e frisadas em "U" e rejuntadas com argamassa de cimento e areia no traço 1: 2.
- Enchimento e armação dos blocos (pilaretes e canaletas):
 - As armaduras dos pilaretes devem ser adequadamente ancoradas na viga baldrame;
 - Todas as superfícies em contato com o concreto graute devem estar limpas e isentas de agregados soltos, óleo, graxas e etc;
 - Executar visitas (furos com dimensões mínimas de 7,5cm x 10cm), para inspeção e limpeza, ao pé de cada pilarete a grautear.
- Cimalha de concreto moldada "in loco" com pingadeira em "V".

- Impermeabilização rígida (cristalização) na sapata corrida e na alvenaria de embasamento, avançando 15cm de altura na alvenaria de elevação (acima do solo), conforme indicado na ficha S10.03 do Catálogo de Serviços.
- Revestimento da face externa da alvenaria com chapisco grosso, conforme ficha S11.04 do Catálogo de Serviços.

FICHAS DE REFERÊNCIA

Catálogo de Serviços

Ficha	G1	Gestão de madeira
Ficha	S3.01	Broca de concreto
Ficha	S4.01	Armadura
Ficha	S4.03	Concreto dosado em central
Ficha	S4.04	Concreto graute
Ficha	S4.05	Fôrmas e cimbramento em madeira
Ficha	S7.04	Alvenaria de bloco de concreto (classe C)
Ficha	S10	Impermeabilização
Ficha	S10.03	Cristalização
Ficha	S11.04	Chapisco

RECEBIMENTO

- O serviço pode ser recebido se atendidas todas as condições de projeto, fornecimento e execução.
- Fôrmas de madeira:
 - Verificar se os insumos de madeira foram adquiridos de empresas cadastradas no CADMADEIRA;
 - A aceitação do lote e a verificação da espécie botânica devem ser efetuadas conforme orientações constantes da ficha G1 Gestão de Madeira do Catálogo de Serviços.
- Verificar as especificações do bloco de concreto.
- Verificar o prumo, o nível e o alinhamento na face interna (sem revestimento) da alvenaria, os quais não deverão apresentar diferenças superiores a 5mm por metro (colocada a régua de 2 metros em qualquer posição, não poderá haver afastamentos maiores que 5mm nos pontos intermediários da régua e 1cm nas pontas).
- Verificar visualmente o assentamento, as juntas, a textura dos blocos e o revestimento em chapisco grosso, que deve apresentar-se uniforme em toda a extensão do muro.

SERVIÇOS INCLUÍDOS NOS PREÇOS

- Escavação da vala e apiloamento do fundo.
- Aberturas, fôrmas, armação e concretagem das vigas baldrame / brocas.
- Impermeabilização da fundação e da alvenaria de embasamento.
- Alvenaria, armação e concretagem dos pilaretes e canaletas.
- Cimalha de concreto com pingadeira.
- Revestimento da face externa da alvenaria.
- Reaterro, regularização, compactação e limpeza do terreno, inclusive externamente.

CRITÉRIOS DE MEDIÇÃO

- m — por metro linear executado, medido na projeção horizontal.

NORMAS

- NBR 6136:2016- Blocos vazados de concreto simples para alvenaria - Requisitos.
- NBR 16697:2018 - Cimento Portland - Requisitos.
- Obs.:** As edições indicadas estavam em vigor no momento desta publicação. Como toda norma está sujeita à revisão, recomenda-se verificar a existência de edições mais recentes das normas citadas.

Componentes

FD-08

Fechamento divisa/ bloco de concreto / rev. chapisco grosso

revestimento apenas na face externa (h=185cm / broca)

Revisão 6
Data 20/03/19

Página
3/3

Código de listagem

1601009



Atenção
Preserve a escala
Quando for imprimir, use folhas A4 e desabilite a função "Fit to paper"

Respeite o Meio Ambiente.
Imprima somente o necessário