



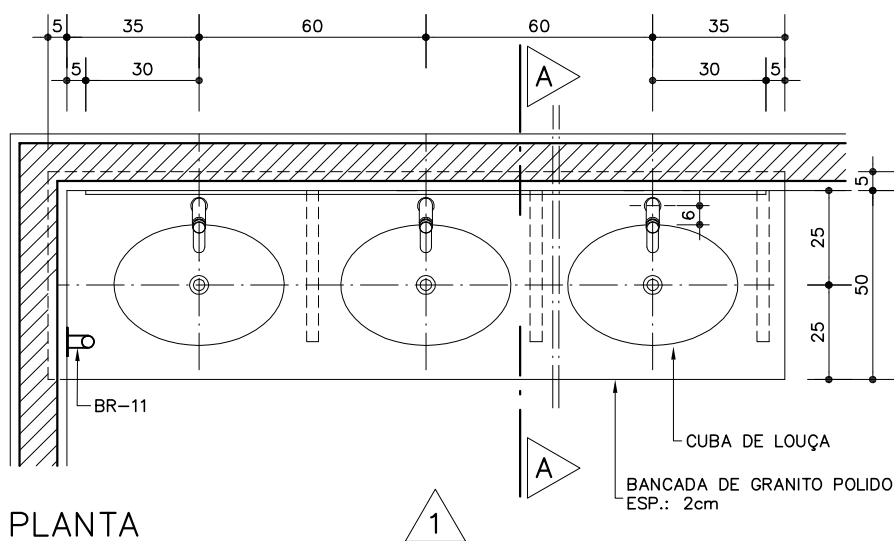

PLANTA
ESC. 1:20

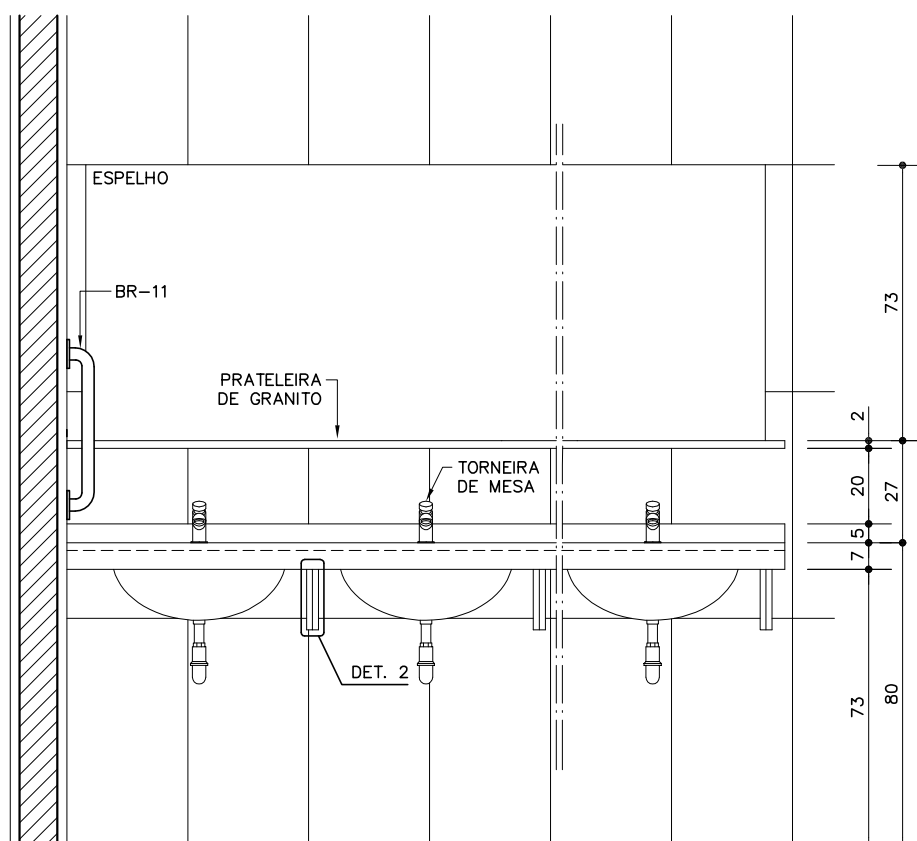

VISTA 1
ESC. 1:20

LT-07

Lavatório com torneira de mesa

[Sanitário
administrativo]

eco

Revisão	4
Data	31/01/22

Página

 $\frac{1}{4}$

Código de listagem

08.15.019



Atenção

Preserve a escala
Quando for imprimir, use folhas A4 e desabilite a função "Fit to paper"

Respeite o Meio Ambiente.
Imprima somente o necessário

LT-07

Lavatório com torneira de mesa

(Sanitário administrativo)

eco

Revisão	4
Data	31/01/22

Página
2/4

Código de listagem


08.15.019



Atenção

Preserve a escala
Quando for imprimir, use
folhas A4 e desabilite a
função "Fit to paper"

Respeite o Meio Ambiente.
Imprima somente o necessário

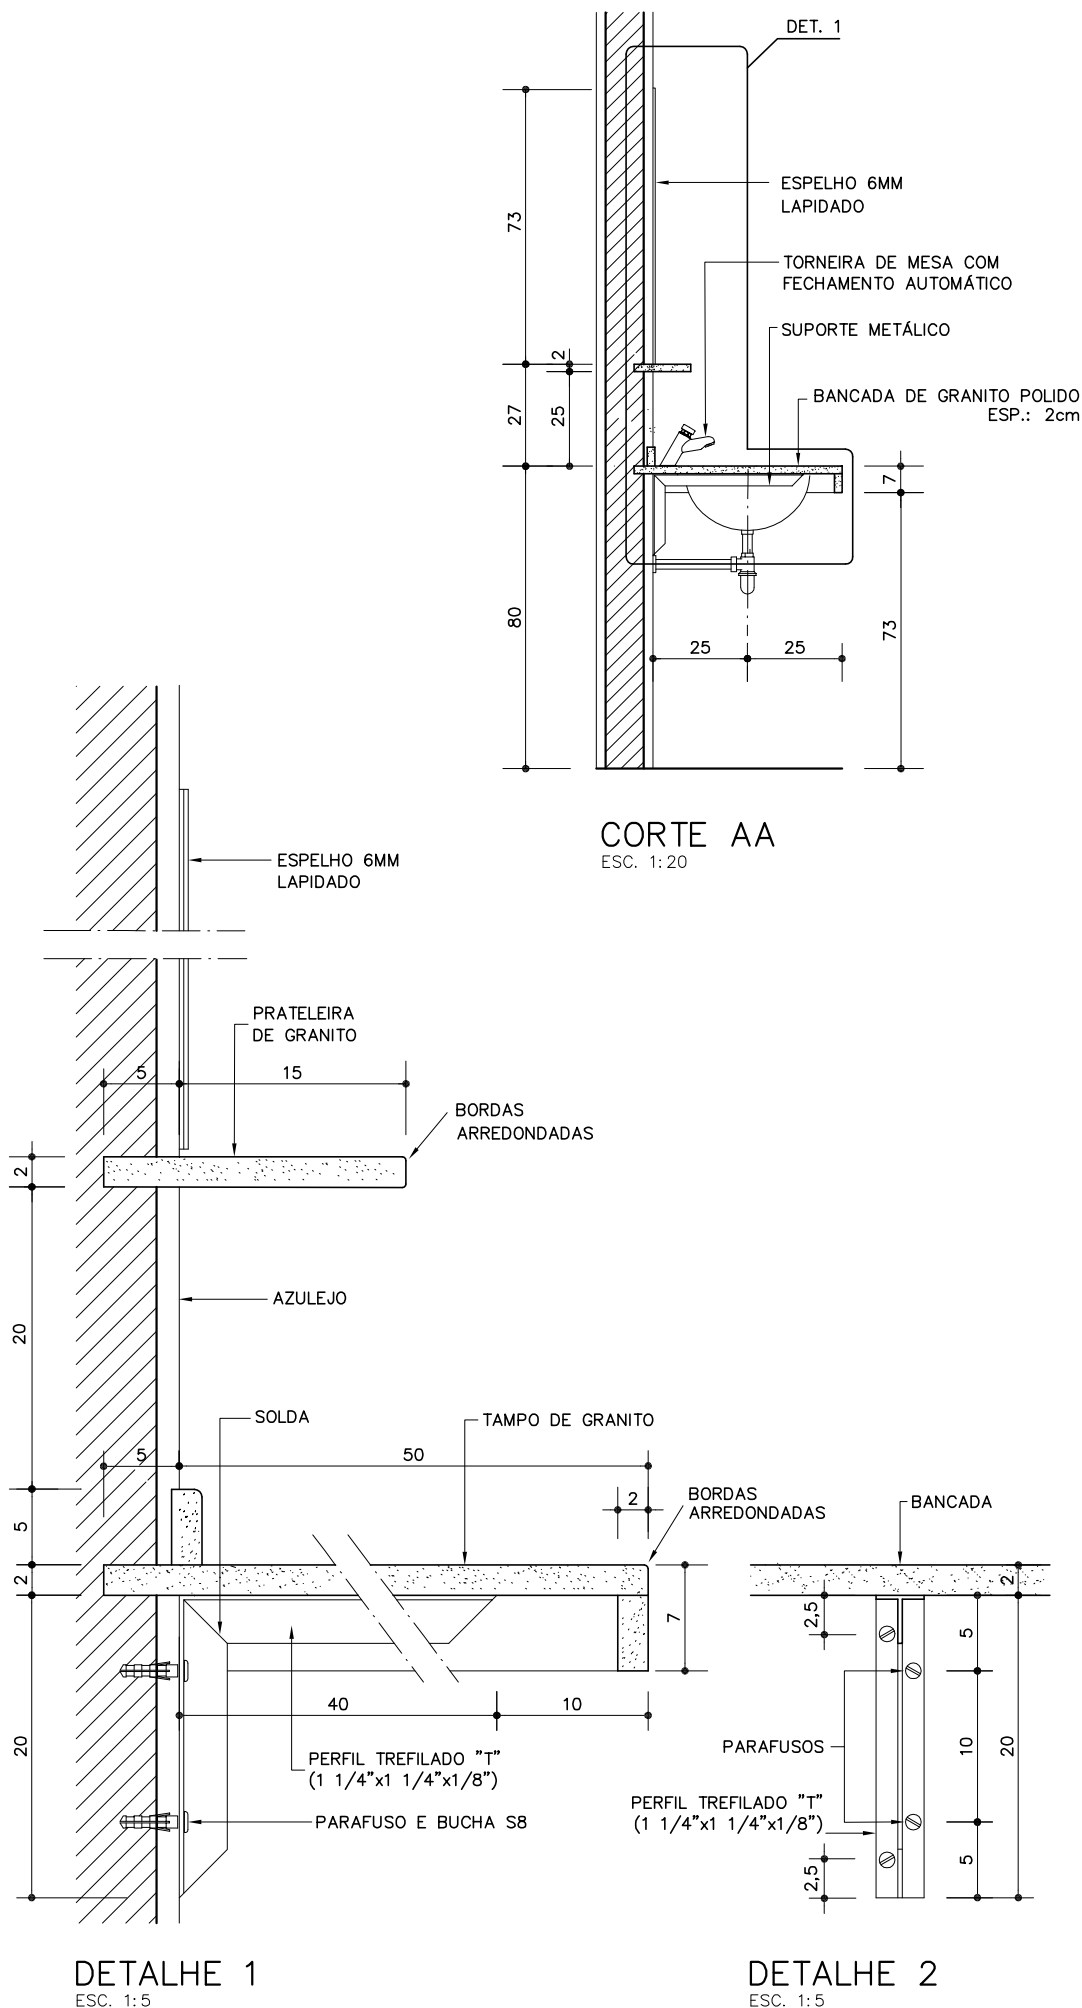

DESCRIÇÃO

Constituintes

- Tampo com frontão e prateleira de granito polido, L=55cm, e=2cm, cinza andorinha ou cinza corumbá.
- Cuba de embutir, oval, de cerâmica esmaltada impermeável, na cor branca, isenta de defeitos visíveis como: gretamento, empenamento da superfície de fixação, trinca, rachadura, ondulação, bolhas, acabamento opaco (esmaltado mal acabado) e corpo exposto (porção não esmaltada), em todas as partes da peça;
- Suporte metálico (40 x 20cm) em perfil trefilado "T" (1 1/4" x 1 1/4" x 1/8"), de aço galvanizado.
- Torneira de acionamento manual e ciclo de fechamento automático, eixo de entrada d'água na vertical (mesa), conforme ficha H6.12 do Catálogo de Serviços.
- Sifão tipo copo - Ø=1" x 1 1/2", conforme ficha H6.18 do Catálogo de Serviços.
- Válvula de escoamento - Ø=1", conforme ficha H6.18 do Catálogo de Serviços.
- Espelho de 6mm de espessura, lapidado e adesivado ao substrato.

Obs.: O componente BR-11 não faz parte do LT-07, sendo pago em outro serviço.

Acessórios

- Parafusos galvanizados de rosca soberba e buchas de nylon (FISCHER S8), para os suportes metálicos.
- Massa plástica para fixação da cuba: resina poliéster.
- Fita veda-rosca de politetrafluoretileno.
- Adesivo elastomérico a base d'água para fixar o espelho (CEBRACE).
- Trava química.

Acabamentos

- Suportes metálicos:
 - Tratamento de galvanização a frio nos pontos de solda, fundo para galvanizado e pintura esmalte na cor grafite, se não houver outra indicada em projeto.

Protótipo comercial

- Cuba:
 - INCEPA/CELITE: 76117
 - DECA: L37 17
 - FIORI: CB01
 - ICASA: IL6
- Torneira de mesa:
 - Ver ficha H6.12 do Catálogo de Serviços.
- Sifão, válvula de escoamento, fita veda-rosca e trava química:
 - Ver ficha H6.18 do Catálogo de Serviços.
- Adesivo elastomérico a base d'água para fixar o espelho:
 - CEBRACE (Fixa espelho)

APLICAÇÃO

- Em sanitários administrativos ou conforme especificação em projeto.

EXECUÇÃO

- As dimensões e a localização dos equipamentos devem ser obedecidas integralmente, pois foram definidas para atender às condições de acessibilidade da norma NBR 9050.
- Tampo de granito: deve ser engastado na alvenaria posterior e laterais (quando houver) e apoiado nos perfis de ferro.
- Prateleira de granito:
 - Deve ser engastada na alvenaria posterior e laterais (quando houver).
- Fixar a cuba no tampo de granito com massa plástica.

- As pontas dos perfis de apoio devem ser chanfradas, conforme desenho.
- Torneira de mesa:
 - A torneira deve ser instalada corretamente, de acordo com instruções do fabricante e conforme constante na ficha H6.12.
 - Eixo do furo para torneira a 6cm da borda da cuba, conforme desenho em planta;
 - A flange de travamento da torneira deve ser de metal. Caso o fabricante a forneça em material plástico, esta deve ser substituída, pois a trava química só funciona entre metais;
 - Após a limpeza da rosca da torneira passar, obrigatoriamente, a trava química segundo orientações do fabricante, mantendo a torneira na posição correta.
- Espelho:
 - Adesivado ao substrato com adesivo elastomérico a base d'água.

Observações:

- Seguir as instruções de uso do fabricante do adesivo para a sua aplicação e rendimento (www.cebrace.com.br);
- Não utilizar adesivos de contato que contenha solventes orgânicos ou componentes ácidos, pela possibilidade de ataque químico a superfície espelhada.

Obs.: As barras de apoio e puxadores das portas devem possuir o mesmo tipo de acabamento quando aplicados em um mesmo ambiente, mantendo a homogeneidade.

FICHAS DE REFERÊNCIA

Catálogo de Componentes

Ficha BR-11 Barra de apoio para lavatórios coletivos

Catálogo de Serviços

Ficha H2.05 Tubos e conexões de ferro galvanizado
Ficha H6 Aparelhos, louças e metais
Ficha H6.12 Torneira de fechamento automático
Ficha H6.18 Complementos de instalação hidráulica

RECEBIMENTO

- O serviço pode ser recebido se atendidas todas as condições de projeto, fornecimento e execução.
- Aferir a conformidade com as especificações e os protótipos homologados.
- Tampo e prateleira de granito:
 - Verificar dimensões (tolerâncias admissíveis: largura ± 10 mm, espessura ± 1 mm);
 - Verificar o nível em duas direções ortogonais com "nível de bolha";
 - Verificar o polimento, não devendo haver arestas vivas.
- Suportes metálicos:
 - Devem ter, necessariamente, as bitolas indicadas; verificar se as pontas estão chanfradas e se na pintura não há defeitos visíveis;
 - Exigir os certificados de galvanização a fogo emitido pela empresa galvanizadora, ou nota fiscal discriminada, para todos os perfis de ferro e a aplicação da galvanização a frio nos pontos de solda;
 - Verificar o uso de parafusos galvanizados.
- Cubas:
 - Verificar a locação e a ausência de defeitos visíveis nas superfícies como: empenamento da superfície de fixação e do plano de transbordamento, gretamento, trinca, rachadura, ondulação, bolhas, acabamento opaco (esmaltado mal acabado) e corpo exposto (porção não esmaltada), em todas as partes visíveis da peça.
- Torneiras de mesa:

Componentes

LT-07

Lavatório com torneira de mesa

[Sanitário administrativo]



Revisão 4
Data 31/01/22

Página
3/4

Código de listagem

08.15.019



Atenção
Preserve a escala
Quando for imprimir, use folhas A4 e desabilite a função "Fit to paper"

Respeite o Meio Ambiente.
Imprima somente o necessário

FDE FUNDAÇÃO PARA O DESENVOLVIMENTO DA EDUCAÇÃO

Componentes

LT-07

Lavatório com torneira de mesa

[Sanitário
administrativo]

eco

Revisão 4
Data 31/01/22

Página
4/4

Código de listagem

08.15.019

- Verificar se o equipamento foi instalado conforme instruções do fabricante e o constante da ficha H6.12;
 - Verificar se está bem fixa (não pode haver movimentação lateral);
 - Verificar a impossibilidade de extrair a torneira manualmente (sem uso de ferramentas), para confirmação do uso da trava química.
- Espelho:
 - Verificar a planicidade na instalação e a isenção de riscos, lascas e trincas.

SERVIÇOS INCLUÍDOS NOS PREÇOS

- Tampo com frontão e prateleira de granito.
- Cubas.
- Torneiras de mesa, com trava química.
- Acessórios de instalações hidráulicas.
- Suporte metálico e parafusos com bucha.
- Espelho adesivado.

CRITÉRIOS DE MEDIÇÃO

- m — por metro linear executado.

LEGISLAÇÃO

- Decreto Estadual 45.805, de 15 de maio de 2001 - Institui o Programa Estadual de uso racional de água potável e dá providências correlatas.
- Decreto Estadual 48.138, de 07 de outubro de 2003 – Institui medidas de redução de consumo e racionalização do uso de água no âmbito do estado de São Paulo.

NORMAS

- NBR 9050:2020- Acessibilidade a edificações, mobiliário, espaços e equipamentos urbanos.
- NBR 16728-1:2019 - Tanques, lavatórios e bidês - Parte 1: Requisitos e métodos de ensaio.
- NBR 16728-2:2019 - Tanques, lavatórios e bidês - Parte 2: Procedimento para instalação.

Obs.: As edições indicadas estavam em vigor no momento desta publicação. Como toda norma está sujeita à revisão, recomenda-se verificar a existência de edições mais recentes das normas citadas.

eco Torneira de baixo consumo de água, com ciclo de fechamento automático, propiciando economia e uso racional de água potável com objetivo de preservação do recurso natural.



Atenção

Preserve a escala
Quando for imprimir, use
folhas A4 e desabilite a
função "Fit to paper"

Respeite o Meio Ambiente.
Imprima somente o ne-
cessário