



PF-19

Porta de ferro para reservatório
(60x180cm)

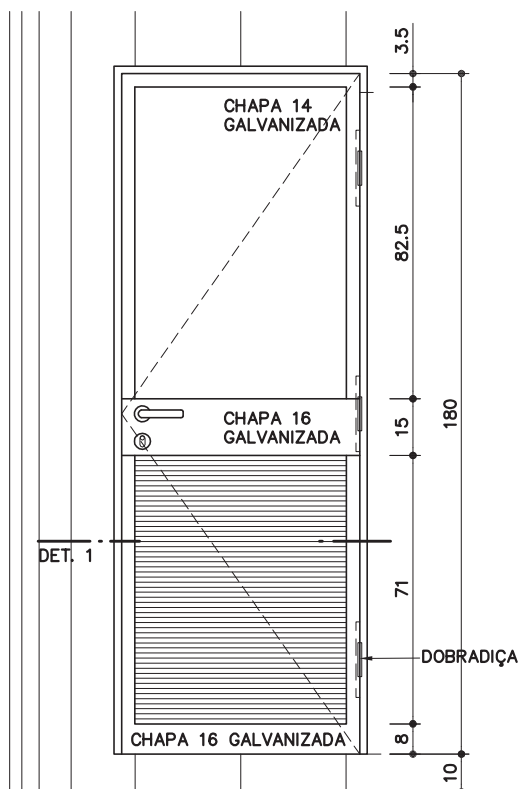


VISTA EXTERNA

ESC. 1:20

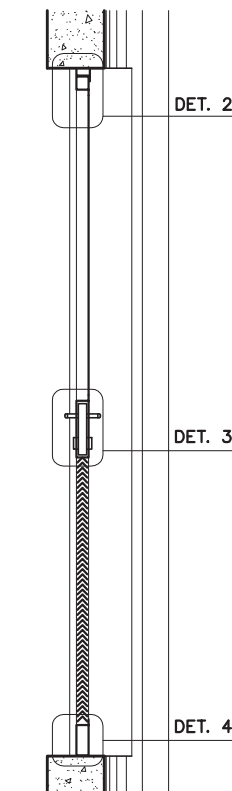


CORTE

ESC. 1:20

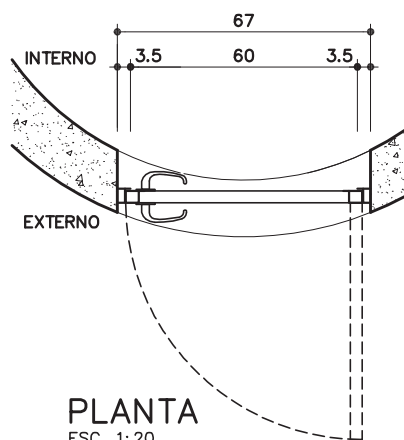

PLANTA

ESC. 1:20

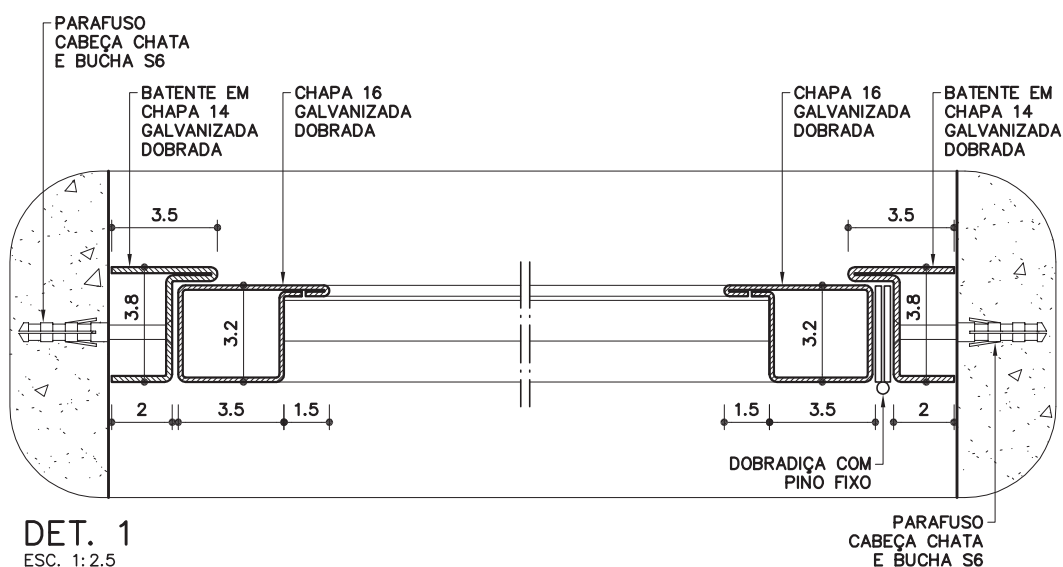

DET. 1

ESC. 1:2.5

Revisão 7
Data 31/10/17

Página

1/3

Código de listagem

06.02.019



Atenção

Preserve a escala
Quando for imprimir, use
folhas A4 e desabilite a
função "Fit to paper"

Respeite o Meio Ambiente.
Imprima somente o ne-
cessário

PF-19

Porta de ferro para reservatório
(60x180cm)

Revisão 7
Data 31/10/17

Página
2/3

Código de listagem


06.02.019



Atenção

Preserve a escala
Quando for imprimir, use
folhas A4 e desabilite a
função "Fit to paper"

Respeite o Meio Ambiente.
Imprima somente o necessário

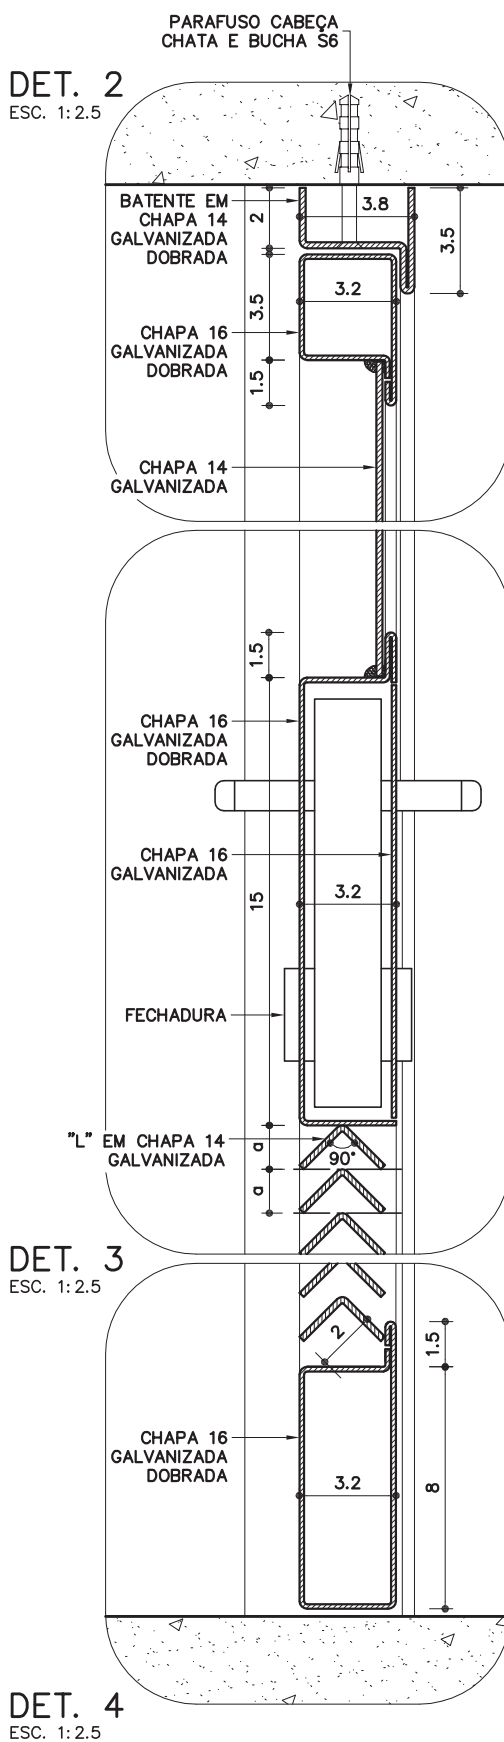

DESCRIÇÃO

Constituintes

- Folha da porta:
 - Perfis em chapas 14 (e=1,9mm) e 16 (e=1,5mm) de aço galvanizado, dobradas;
 - Chapa 14, de aço galvanizado, lisa.
- Batente: perfil em chapa 14 (e=1,9mm) de aço galvanizado, dobrado.
- Galvanização a frio (tratamento anticorrosivo rico em zinco) nos pontos de solda e corte, conforme Ficha S14.17 do Catálogo de Serviços.

Acessórios

- Ferragens, conforme Ficha S17.01 do Catálogo de Serviços:
 - Conjunto fechadura - maçaneta;
 - Dobradiças: 3 unidades.

Acabamentos

- Pintura esmalte sobre fundo para galvanizados, na cor especificada em projeto.

Protótipo comercial

- Ferragens (conjunto fechadura - maçaneta; dobradiças):
 - Ver Ficha S17.01 do Catálogo de Serviços.
- Galvanização a frio:
 - Ver ficha S14.17 do Catálogo de Serviços.

APLICAÇÃO

- Em barriletes de reservatórios elevados, conforme especificado em projeto.

EXECUÇÃO

- Bater os pontos de solda e eliminar todas as rebarbas nas emendas e linhas de corte dos perfis e chapas.
- Todos os pontos de solda e corte devem estar isentos de poeira, gordura, graxa, sabão, ferrugem ou qualquer outro contaminante para receber galvanização a frio (ver Ficha S14.17).
- Antes da aplicação de fundo para galvanizados, toda superfície metálica deve estar completamente limpa, seca e desengraxada.

FICHAS DE REFERÊNCIA

Catálogo de Serviços

Ficha	S14	Pintura
Ficha	S14.09	Tinta esmalte sintético standard
Ficha	S14.17	Galvanização
Ficha	S14.18	Fundos para metais
Ficha	S14.21	Tinta esmalte à base de água
Ficha	S17.01	Ferragens para porta

RECEBIMENTO

- O serviço pode ser recebido se atendidas todas as condições de projeto, fornecimento e execução.
- Perfis e chapas devem ter, necessariamente, as bitolas indicadas.
- Verificar a não ocorrência de rebarbas e pontos de solda mal batidos.
- Não serão aceitas portas empenadas, desniveladas, fora de prumo ou de esquadro, ou que apresentem quaisquer defeitos decorrentes do manuseio e transporte.
- Verificar o acabamento, atentando para que não apresente falhas na pintura ou quaisquer danos decorrentes do manuseio.
- O funcionamento da porta deve ser verificado após a completa secagem da pintura e subsequente lubrificação; não deve apresentar jogo causado por folgas.

- A folha da porta deverá ser colocada em posição semi-aberta e permanecer parada, caso contrário, será sinal evidente de desvio de prumo.
- Acessórios:
 - Aferir as especificações e protótipo comercial, conforme constante da Ficha S17.01;
 - Verificar a correta instalação e funcionamento.
- Exigir certificado de galvanização a fogo, emitido pela empresa galvanizadora ou nota fiscal discriminada, comprovando o uso de chapas e perfis e galvanizados.
- Verificar o tratamento dos pontos de solda e corte com galvanização a frio.
- Verificar o uso de parafusos galvanizados.

SERVIÇOS INCLUÍDOS NOS PREÇOS

- Porta completa (folha e batente), com todos os seus constituintes, inclusive galvanização a frio nos pontos de corte e solda.
- Acessórios (ferragens).
- Lubrificação das partes móveis
- Obs.:** A pintura de acabamento será paga em outro serviço.

CRITÉRIOS DE MEDIÇÃO

- un. — por unidade instalada.

NORMAS

- NBR 9050:2015 - Acessibilidade a edificações, mobiliário, espaços e equipamentos urbanos.
- Obs.:** As edições indicadas estavam em vigor no momento desta publicação. Como toda norma está sujeita à revisão recomenda-se verificar a existência de edições mais recentes das normas citadas.

Componentes

PF-19

Porta de ferro para reservatório
(60x180cm)

Revisão 7
Data 31/10/17

Página
3/3

Código de listagem

06.02.019



Atenção
Preserve a escala
Quando for imprimir, use folhas A4 e desabilite a função "Fit to paper"

Respeite o Meio Ambiente.
Imprima somente o necessário

FDE FUNDAÇÃO PARA O DESENVOLVIMENTO DA EDUCAÇÃO