
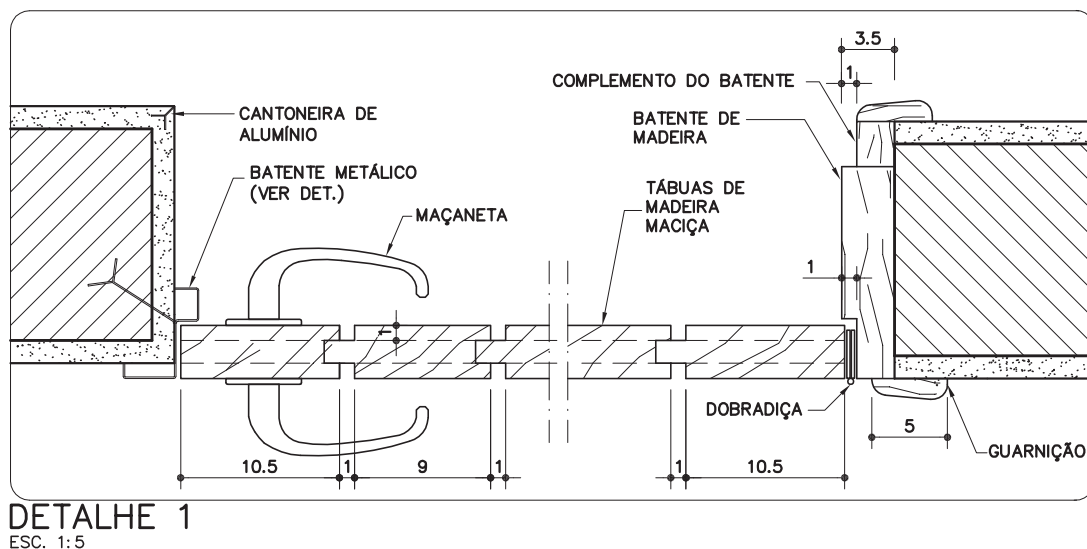


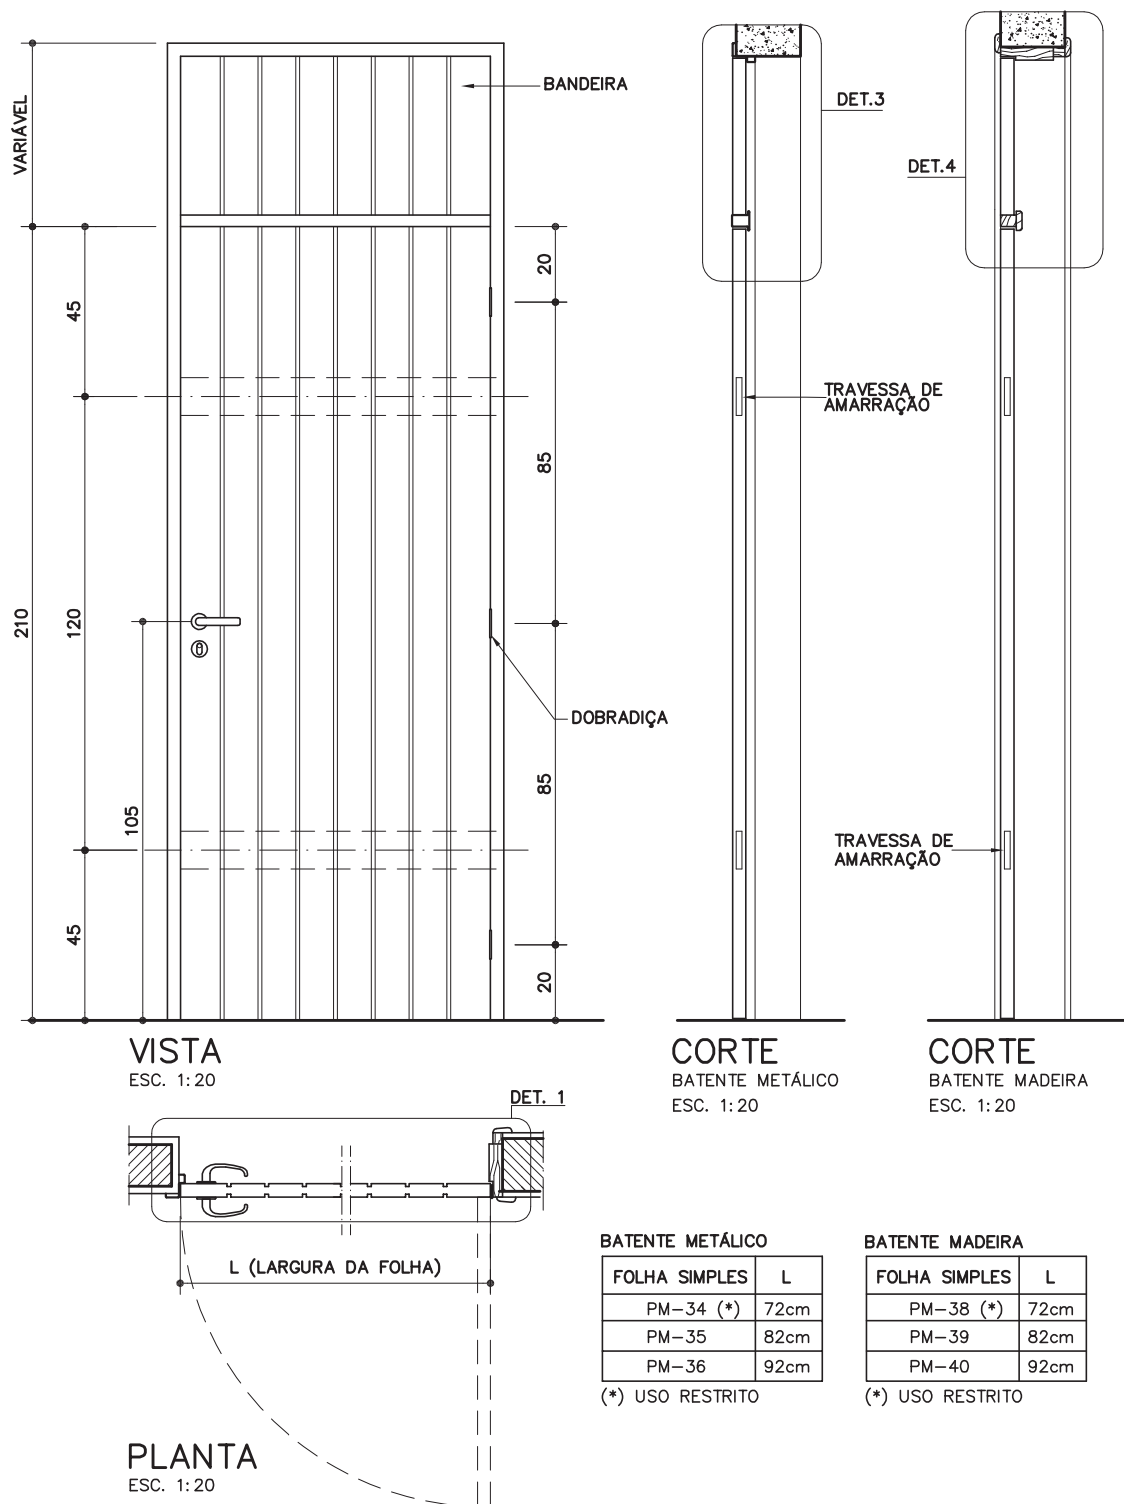

Componentes

PM-34
A
PM-41

**Porta de
madeira
macho-
fêmea p/
pintura c/
bandeira**
PM-34 a PM-37
(Batente metálico)

PM-38 a PM-41
[Batente madeira]

Revisão	8
Data	31/10/17

Página

 $\frac{1}{5}$ **Código de listagem**

05.01.024
05.01.025
05.01.026
05.01.103
05.01.036
05.01.037
05.01.044
05.01.104



Atenção

Preserve a escala
Quando for imprimir, use folhas A4 e desabilite a função "Fit to paper"

Respeite o Meio Ambiente.
Imprima somente o necessário

PM-34 A PM-41

Porta de madeira macho-fêmea p/ pintura c/ bandeira
PM-34 a PM-37
(Batente metálico)

PM-38 a PM-41
(Batente madeira)

Revisão 8
Data 31/10/17


Página
2/5


Código de listagem

- 05.01.024
- 05.01.025
- 05.01.026
- 05.01.103
- 05.01.036
- 05.01.037
- 05.01.044
- 05.01.104


Atenção
Preserve a escala
Quando for imprimir, use folhas A4 e desabilite a função "Fit to paper"

Respeite o Meio Ambiente.
Imprima somente o necessário

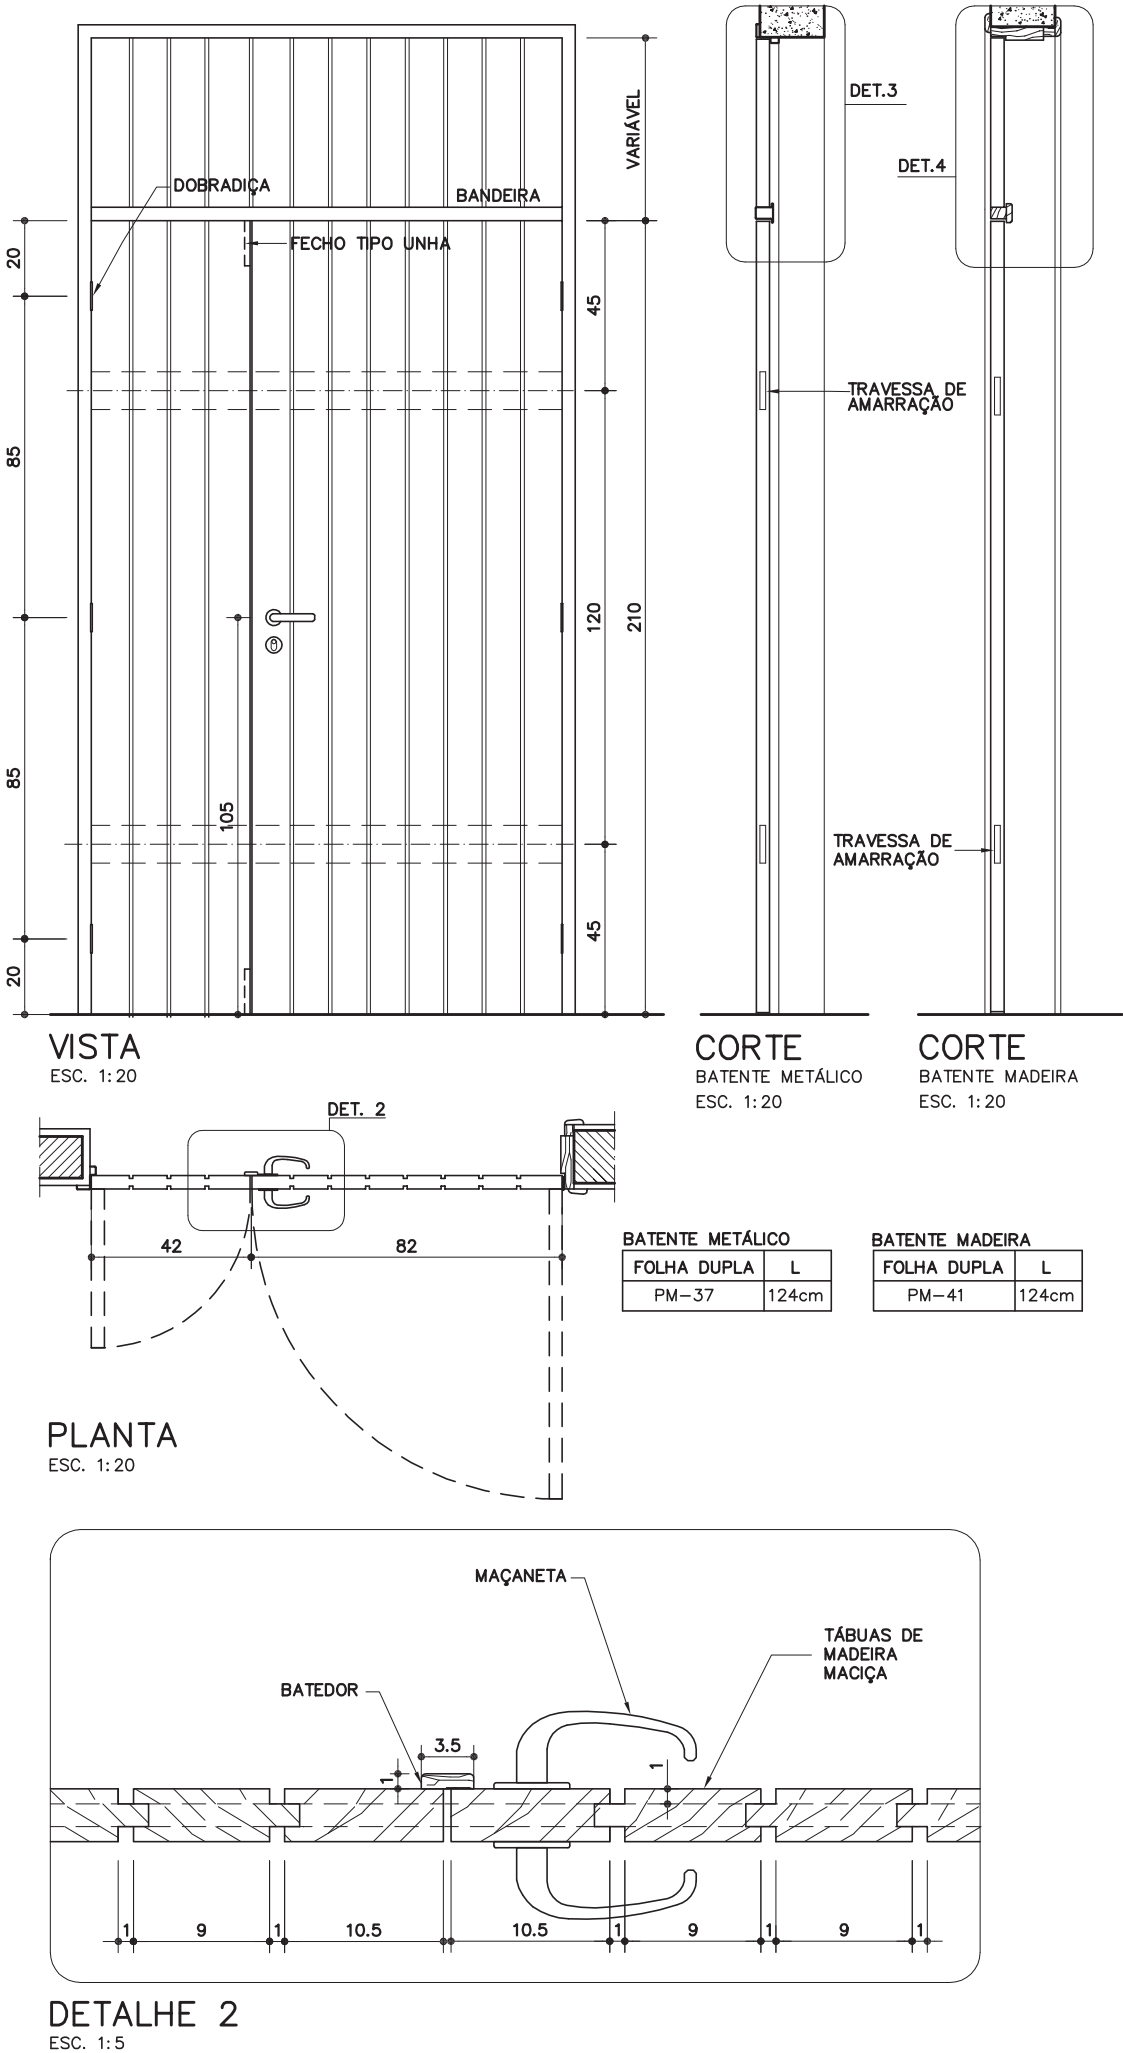

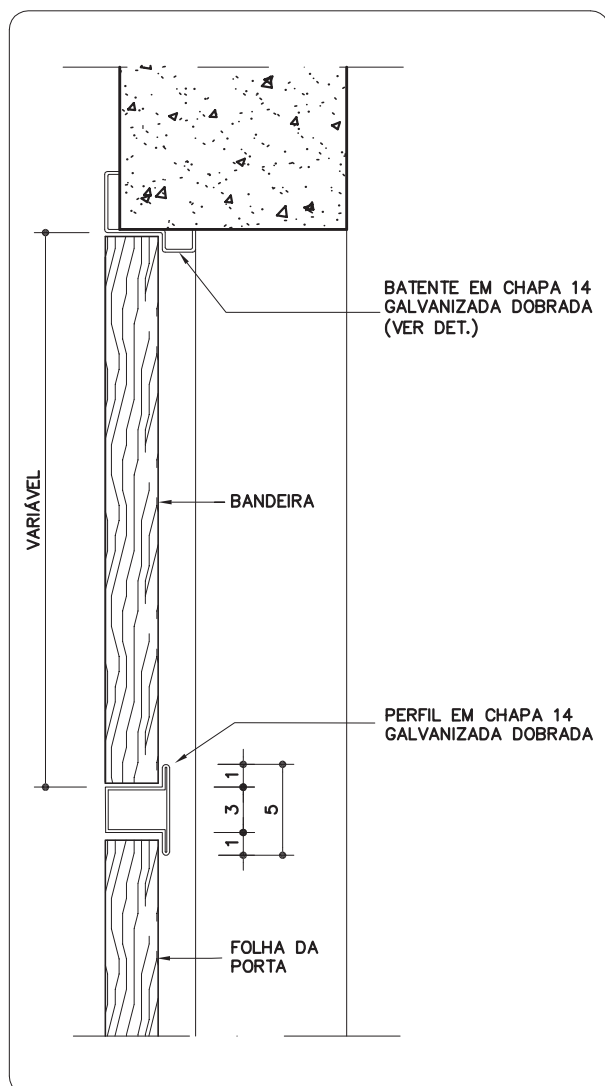

DETALHE 3
BATENTE METÁLICO
ESC. 1:5

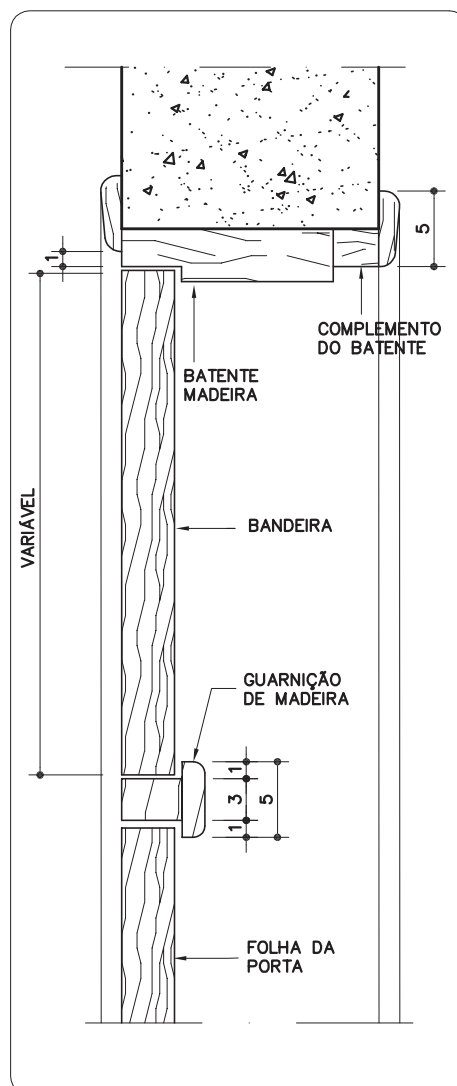


DETALHE 4
BATENTE DE MADEIRA
ESC. 1:5

DETALHE DO BATENTE METÁLICO

ESC. 1:2

* MEDIDAS EM MILÍMETROS

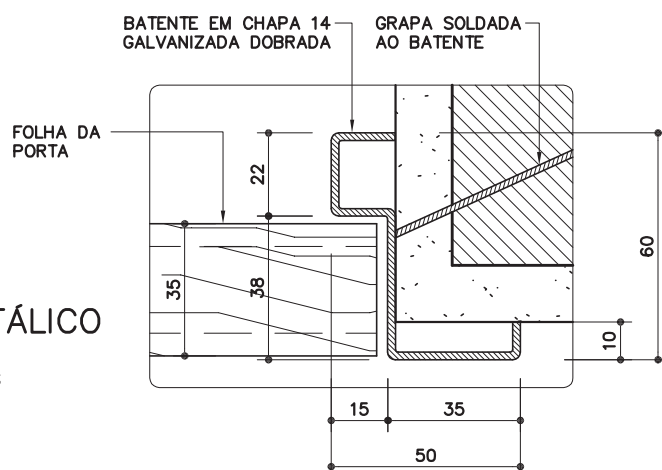

PM-34 A PM-41

Porta de madeira macho-fêmea p/ pintura c/ bandeira

PM-34 a PM-37
[Batente metálico]

PM-38 a PM-41
[Batente madeira]

Revisão 8
Data 31/10/17

Página
3/5

Código de listagem

05.01.024
05.01.025
05.01.026
05.01.103
05.01.036
05.01.037
05.01.044
05.01.104



Atenção

Preserve a escala
Quando for imprimir, use folhas A4 e desabilite a função "Fit to paper"

Respeite o Meio Ambiente.
Imprima somente o necessário

PM-34 A PM-41

Porta de madeira macho-fêmea p/ pintura c/ bandeira
PM-34 a PM-37
(Batente metálico)

PM-38 a PM-41
(Batente madeira)

Revisão 8
Data 31/10/17

Página
4/5

Código de listagem

05.01.024
05.01.025
05.01.026
05.01.103
05.01.036
05.01.037
05.01.044
05.01.104



Atenção
Preserve a escala
Quando for imprimir, use folhas A4 e desabilite a função "Fit to paper"

Respeite o Meio Ambiente.
Imprima somente o necessário

DESCRIÇÃO

Constituintes

- Espécies de madeira, conforme Classificação de Uso constante da ficha G1 Gestão de Madeira do Catálogo de Serviços:
 - Folha da porta, bandeira e batente: classificação G1-C1, construção leve - esquadria;
 - Guarnições: classificação G1-C4, construção leve interna - utilidade geral.
- Folha da porta e bandeira tipo mexicana (e=35mm), confeccionada com tábuas de madeira para pintura, encaixe macho-fêmea e amarração com travessas embutidas.
- PM-34 a PM-37:
 - Batente em chapa 14 (e=1,9mm), de aço galvanizado, dobrada, fixado com grapas ou parafusos e buchas.
- PM-38 a PM-41:
 - Batente de madeira maciça (3,5 x 14cm) fixado através de chapuz de madeira, espuma expansiva ou parafusos e buchas;
 - Complemento do batente destinado a ajustar as dimensões do batente à parede acabada. Utilizar madeiras desempenadas e lixadas com as mesmas características do batente;
 - Guarnições de madeira maciça (5cm).

Acessórios

- Ferragens conforme Ficha S17.01 do Catálogo de Serviços:
 - Conjunto fechadura-maçaneta;
 - Dobradiças:
 - » PM-34 a PM-36 e PM-20 a PM-40: 3P unidades;
 - » PM-37 e PM-41 (portas duplas): 6 unidades.
 - Fecho tipo "unha": 2 unidades, para PM-37 e PM-41 (portas duplas).

Acabamentos

- Folha da porta, batente, complementos e guarnições de madeira:
 - Pintura esmalte na cor especificada em projeto.
- Batente metálico:
 - Pintura esmalte sobre fundo para galvanizados, na cor especificada em projeto.

Protótipo comercial

- Folha da porta, batente, complementos e guarnições de madeira:
 - Empresas cadastradas no CADMADEIRA.
- Ferragens para porta (conjunto fechadura-maçaneta; dobradiças; fecho tipo "unha"):
 - Ver Ficha S17.01 do Catálogo de Serviços.

APLICAÇÃO

- Em ambientes com acesso externo ou que requeiram maior segurança, conforme indicação em projeto.

EXECUÇÃO

- Batente metálico:
 - Bater os pontos de solda e eliminar as rebarbas em todas as emendas e linhas de corte das chapas;
 - Todos os locais onde houver ponto de solda e/ou corte, devem estar isentos de poeira, gordura, graxa, sabão, ferrugem ou qualquer outro contaminante, para receber tratamento com galvanização a frio (ver Ficha S14.17);
 - Antes da aplicação de fundo para galvanizados, toda a superfície metálica deve estar completamente limpa, seca e desengraxada.

FICHAS DE REFERÊNCIA

Catálogo de Serviços

Ficha G1 Gestão de Madeira
Ficha S11.02 Cantoneira de alumínio

Ficha S14 Pintura
Ficha S14.09 Tinta esmalte sintético standard
Ficha S14.17 Galvanização
Ficha S14.18 Fundos para metais
Ficha S14.19 Fundos para madeira
Ficha S14.21 Tinta esmalte à base de água
Ficha S17.01 Ferragens para porta

RECEBIMENTO

- O serviço pode ser recebido, se atendidas todas as condições de especificação, projeto, fornecimento e execução.
- A aceitação do lote se fará mediante a comprovação documental da origem da madeira, exigindo-se:
 - Notas fiscais;
 - Declaração de emprego apenas de produtos e subprodutos de madeira de origem exótica ou de origem nativa da flora brasileira adquirida de pessoas jurídicas cadastradas no CADMADEIRA;
 - Comprovante de cadastramento do fornecedor perante o CADMADEIRA (a situação cadastral do fornecedor deverá ser conferida eletronicamente).
- Aferir as especificações de todos os itens.
- Folha da porta, batente, complementos e guarnições de madeira:
 - Espécie botânica:
 - » Conferir a espécie da madeira utilizada, de acordo com a Classificação de Uso constante da ficha G1 Gestão de Madeira, do Catálogo de Serviços;
 - » A Fiscalização poderá, a seu critério, requerer a identificação da espécie botânica da madeira e os resultados de ensaios físico-mecânicos. As amostras, retiradas aleatoriamente do mesmo lote, deverão ser avaliadas em laboratório.
 - Verificar a inexistência de fungos, apodrecimentos ou furos de insetos;
 - Rejeitar peças empenadas, desniveladas, fora de prumo ou de esquadro;
 - A folha da porta deverá ser colocada em posição semi-aberta e permanecer parada, caso contrário, será sinal evidente de desvio de prumo da esquadria.
- Batente metálico:
 - Exigir certificado de galvanização, emitido pela empresa galvanizadora ou nota fiscal discriminada do fornecedor, comprovando o uso de chapa galvanizada;
 - Verificar a não ocorrência de rebarbas e pontos de solda mal batidos;
 - Verificar o tratamento dos pontos de solda e corte com galvanização a frio.
- Acessórios:
 - Aferir as especificações e protótipo comercial;
 - Verificar a correta instalação e funcionamento.
- Verificar a ausência de falhas na pintura ou quaisquer defeitos decorrentes do manuseio.
- O funcionamento da porta deverá ser aferido após a completa secagem da pintura e subsequente lubrificação, não podendo apresentar jogo causado por folgas.

SERVIÇOS INCLUÍDOS NOS PREÇOS

- Folha da porta e bandeira.
- Batente, guarnições e complemento.
- Acessórios (ferragens).
- Lubrificação das partes móveis.

CRITÉRIOS DE MEDIÇÃO

- un. — por unidade instalada.

LEGISLAÇÃO

- Decreto Estadual nº 53.047, de 02 de junho de 2008 - cria o CADMADEIRA e estabelece procedimentos na aquisição de produtos de subprodutos de madeira de origem nativa pelo Governo do Estado de São Paulo.

NORMAS

- NBR 9050:2015 - Acessibilidade a edificações, mobiliário, espaços e equipamentos urbanos.
- **Obs.:** As edições indicadas estavam em vigor no momento desta publicação. Como toda norma está sujeita à revisão, recomenda-se verificar a existência de edições mais recentes das normas citadas.

Componentes

PM-34 A PM-41

**Porta de
madeira
macho-
fêmea p/
pintura c/
bandeira**

PM-34 a PM-37
[Batente metálico]

PM-38 a PM-41
[Batente madeira]

Revisão 8
Data 31/10/17

Página
5/5

Código de listagem

05.01.024
05.01.025
05.01.026
05.01.103
05.01.036
05.01.037
05.01.044
05.01.104



Atenção
Preserve a escala
Quando for imprimir, use
folhas A4 e desabilite a
função "Fit to paper"

Respeite o Meio Ambiente.
Imprima somente o ne-
cessário