



PM-82 (VÃO LIVRE=90cm)

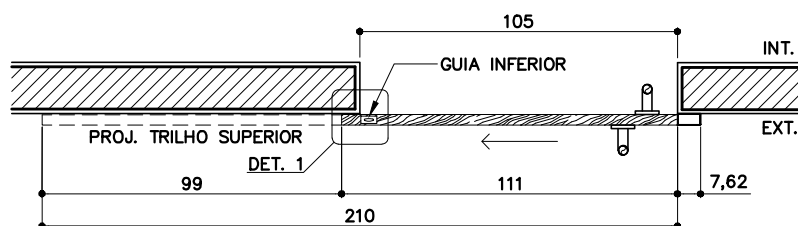


PLANTA-POSIÇÃO FECHADA

ESC. 1: 25

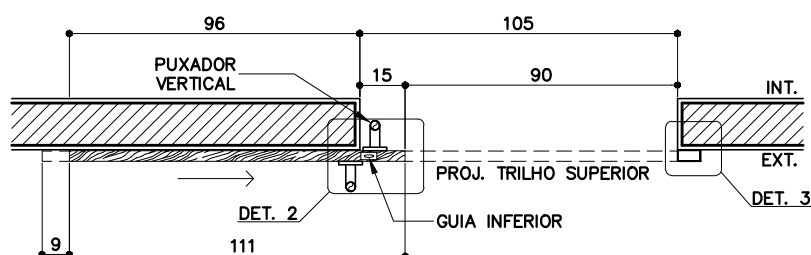

PLANTA-POSIÇÃO ABERTA

ESC. 1: 25

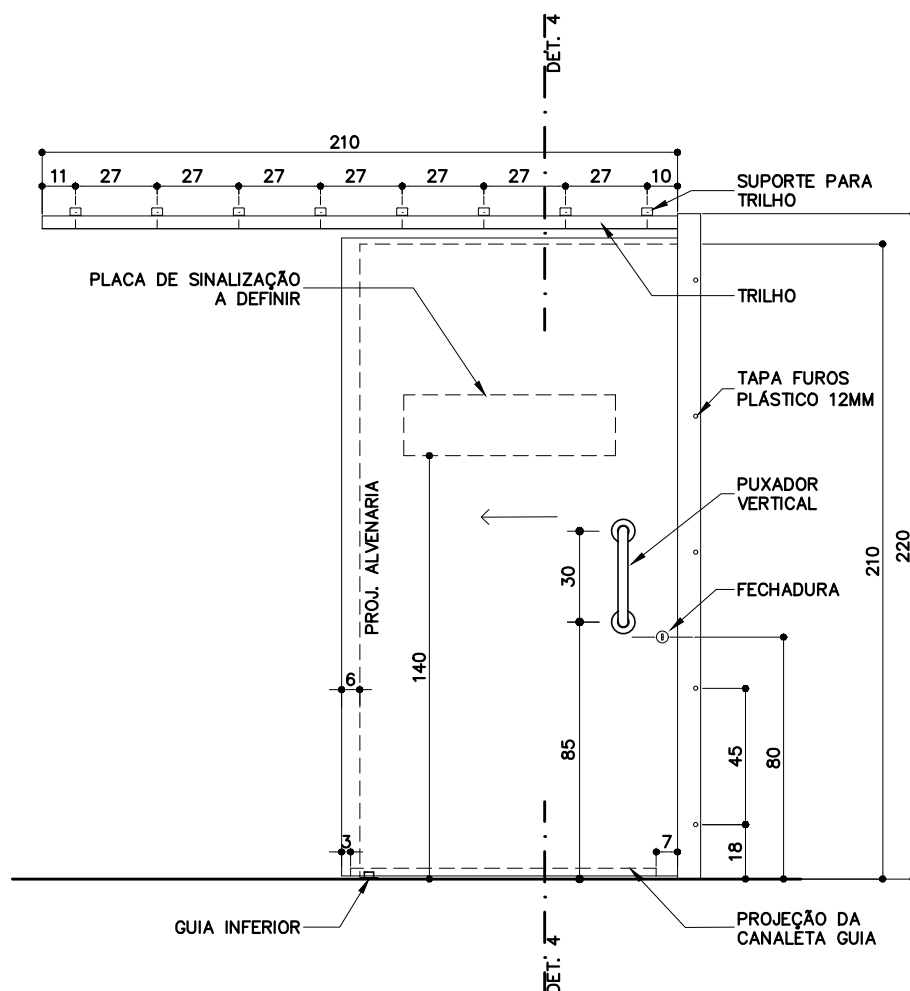

ELEVAÇÃO EXTERNA

ESC. 1: 25

PM-82
PM-83
PM-85Porta de
correr
acessível

[Sarrafeada

Maciça p/ pintura]

PM-82[L = 111cm]

PM-83[L = 101cm]

PM-85[L = 121cm]

Revisão 5
Data 13/06/24Página
1/7

Código de listagem

05.01.069

05.01.070

05.01.111



Atenção

Preserve a escala
Quando for imprimir, use
folhas A4 e desabilite a
função "Fit to paper"

Respeite o Meio Ambiente.
Imprima somente o ne-
cessário

PM-82
PM-83
PM-85

Porta de
correr
acessível

[Sarrafeada
Maciça p/ pintura]
PM-82[L = 111cm]
PM-83[L = 101cm]
PM-85[L = 121cm]

Revisão 5
Data 13/06/24

Página
2/7


Código de listagem

05.01.069
05.01.070
05.01.111

Atenção
Preserve a escala
Quando for imprimir, use
folhas A4 e desabilite a
função "Fit to paper"


Respeite o Meio Ambiente.
Imprima somente o ne-
cessário

PM-83 (VÃO LIVRE=80cm)

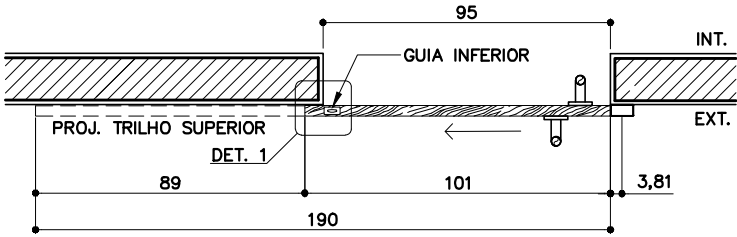


PLANTA-POSIÇÃO FECHADA

ESC. 1: 25

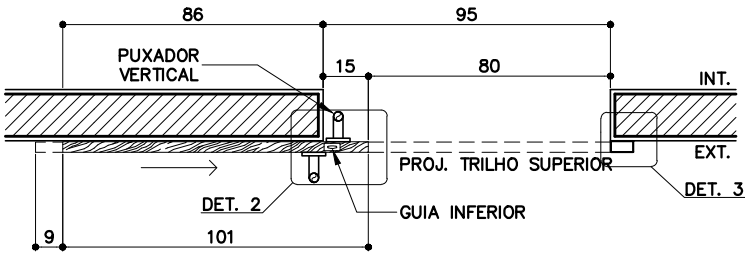

PLANTA-POSIÇÃO ABERTA


ESC. 1: 25

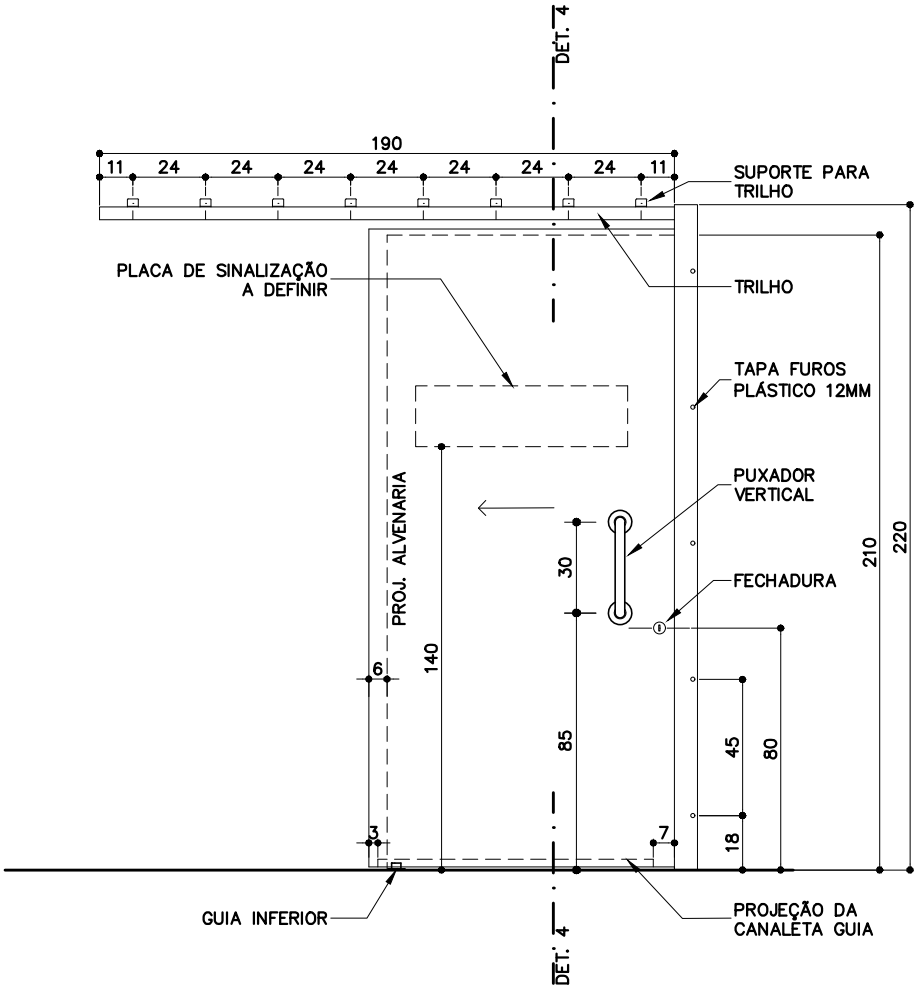

ELEVAÇÃO EXTERNA


ESC. 1: 25

PM-85 (VÃO LIVRE=100cm)

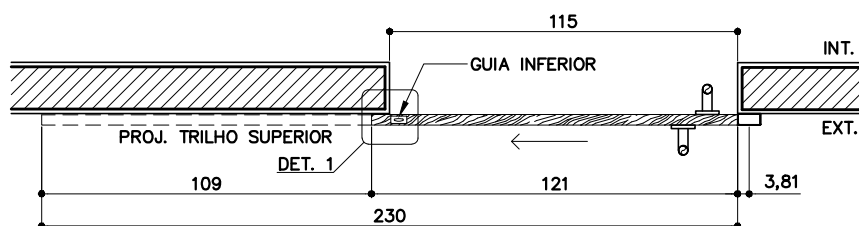


PLANTA-POSIÇÃO FECHADA

ESC. 1: 25

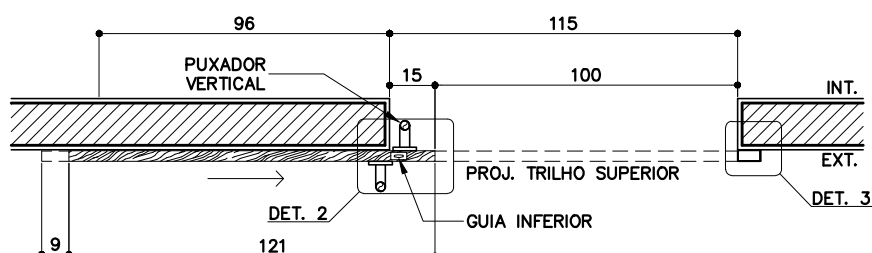

PLANTA-POSIÇÃO ABERTA

ESC. 1: 25

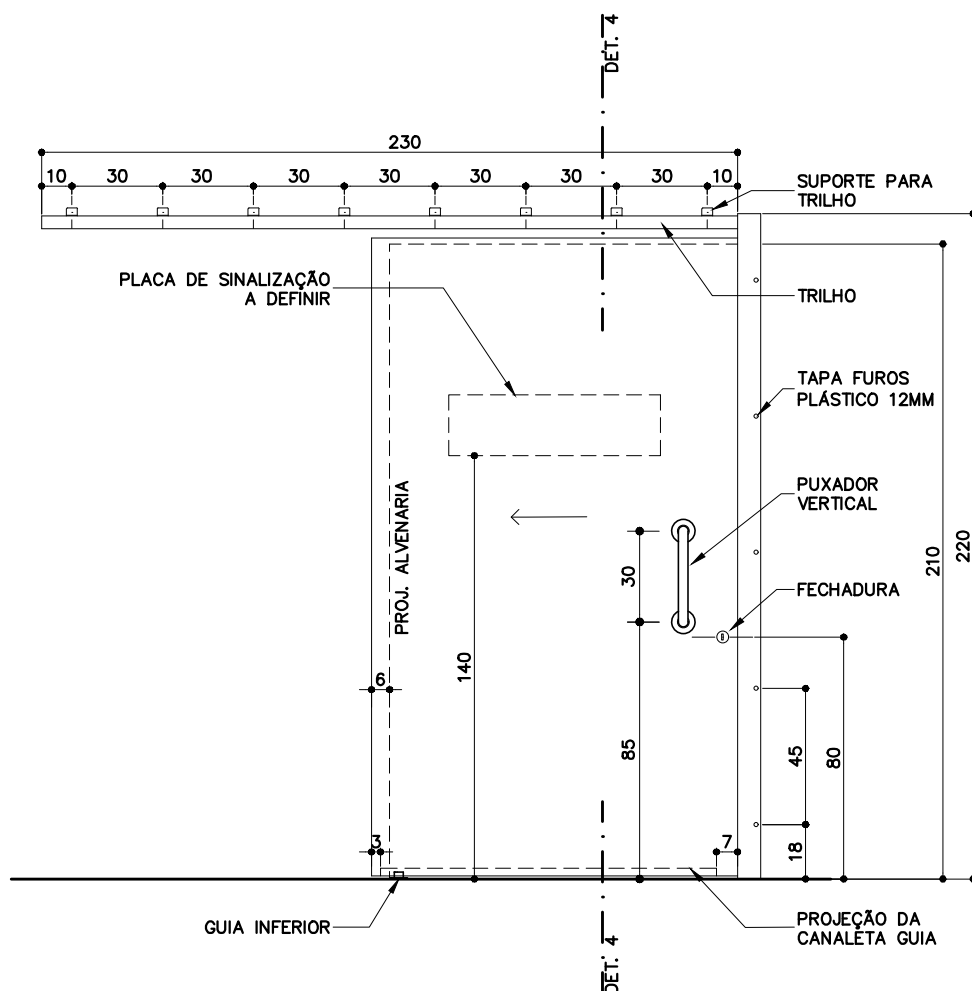

ELEVAÇÃO EXTERNA

ESC. 1: 25

PM-82
PM-83
PM-85Porta de
correr
acessível

[Sarrafeada

Maciça p/ pintura]

PM-82[L = 111cm]

PM-83[L = 101cm]

PM-85[L = 121cm]

Revisão 5
Data 13/06/24Página
3/7

Código de listagem

05.01.069

05.01.070

05.01.111



Atenção

Preserve a escala
Quando for imprimir, use
folhas A4 e desabilite a
função "Fit to paper"

Respeite o Meio Ambiente.
Imprima somente o ne-
cessário

PM-82 PM-83 PM-85

Porta de correr acessível

(Sarrafeada
Maciça p/ pintura)
PM-82(L = 111cm)
PM-83(L = 101cm)
PM-85(L = 121cm)

Revisão 5
Data 13/06/24

Página
4/7

Código de listagem


05.01.069
05.01.070
05.01.111



Atenção


Preserve a escala
Quando for imprimir, use
folhas A4 e desabilite a
função "Fit to paper"

Respeite o Meio Ambiente.
Imprima somente o ne-
cessário

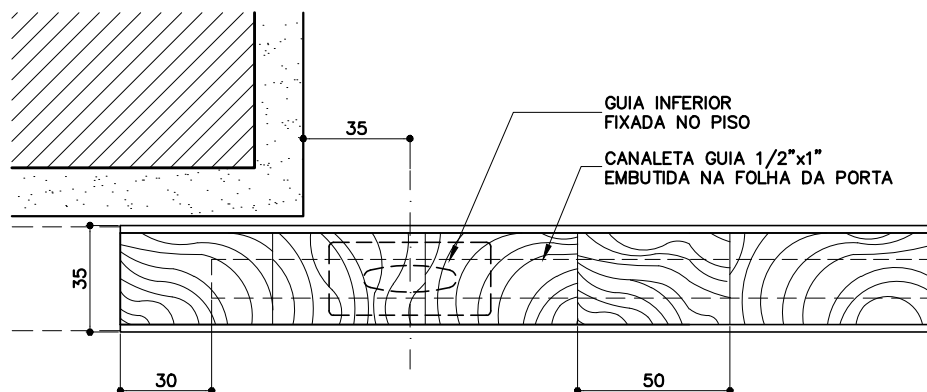


DETALHE 1

ESC. 1:2,5
(MEDIDAS EM mm)

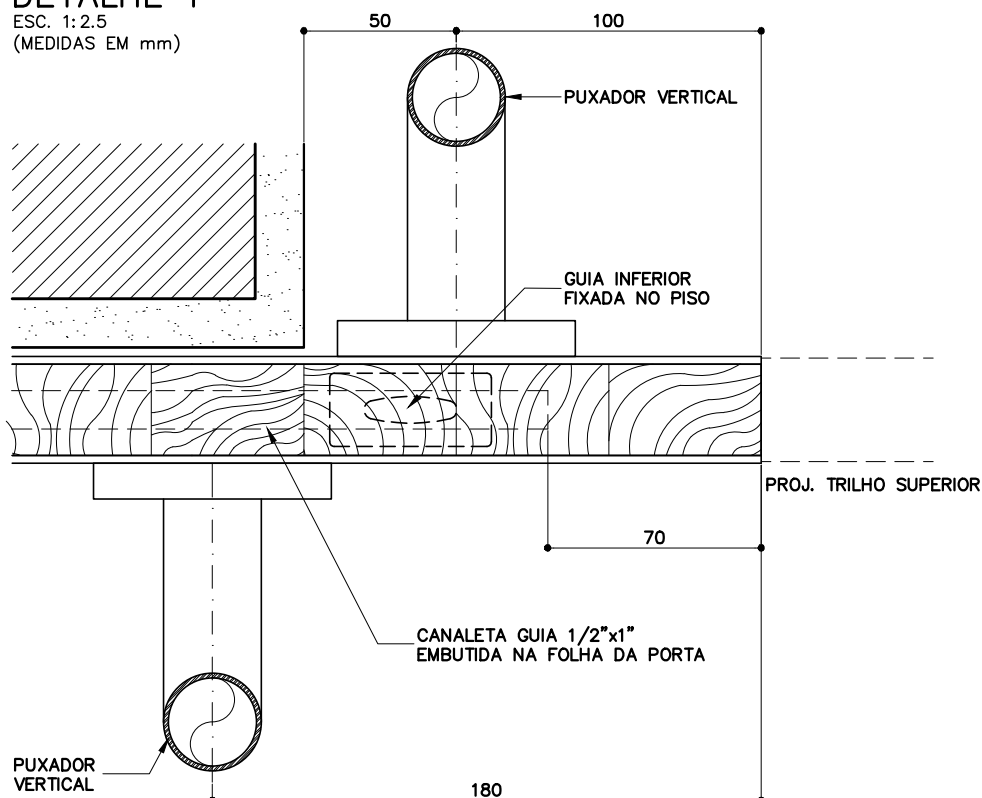


DETALHE 2

ESC. 1:2,5
(MEDIDAS EM mm)

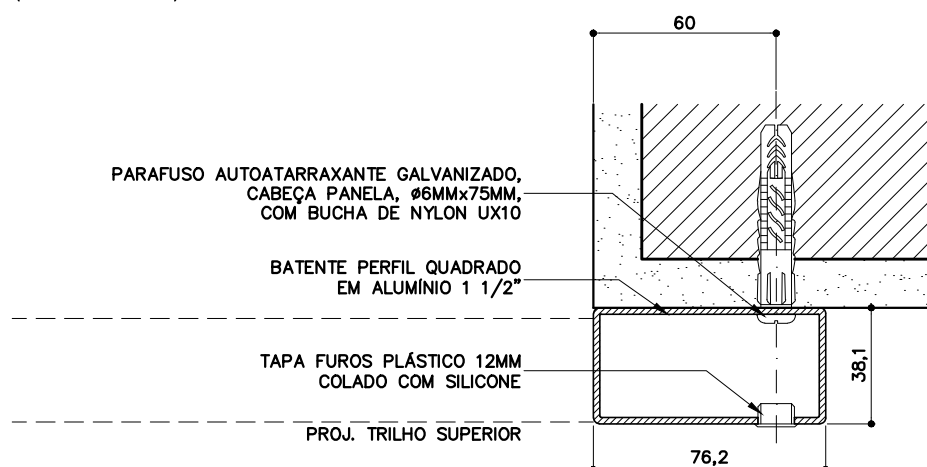

DETALHE 3

ESC. 1:2,5
(MEDIDAS EM mm)

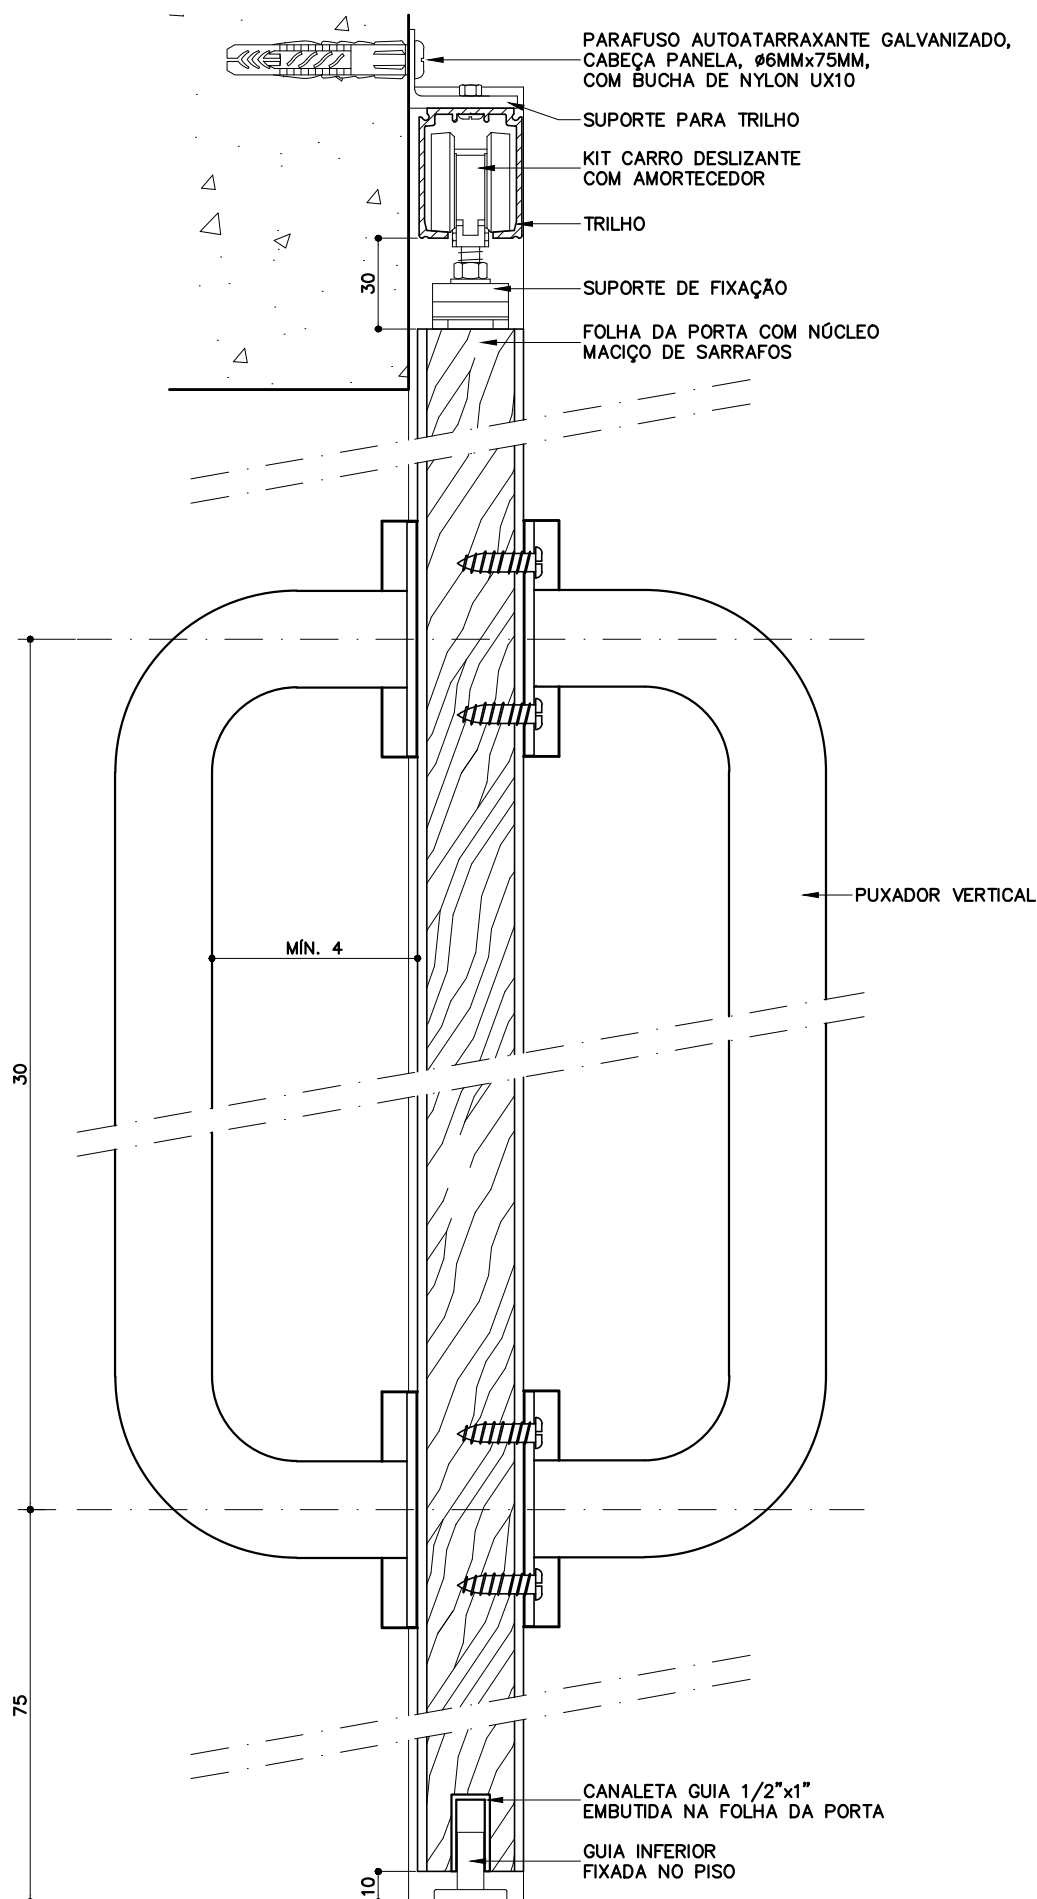

DETALHE 4

ESC. 1:2.5
(MEDIDAS EM mm)

PM-82

PM-83

PM-85

Porta de correr acessível

[Sarrafeada

Maciça p/ pintura]

PM-82[L = 111cm]

PM-83[L = 101cm]

PM-85[L = 121cm]

Revisão 5
Data 13/06/24

Página

5/7

Código de listagem

05.01.069

05.01.070

05.01.111



Atenção

Preserve a escala
Quando for imprimir, use
folhas A4 e desabilite a
função "Fit to paper"

Respeite o Meio Ambiente.
Imprima somente o ne-
cessário

PM-82 PM-83 PM-85

Porta de correr acessível

(Sarrafeada
Maciça p/ pintura)
PM-82(L = 111cm)
PM-83(L = 101cm)
PM-85(L = 121cm)

Revisão 5
Data 13/06/24

Página
6/7

Código de listagem

05.01.069
05.01.070
05.01.111



Atenção
Preserve a escala
Quando for imprimir, use
folhas A4 e desabilite a
função "Fit to paper"

Respeite o Meio Ambiente.
Imprima somente o ne-
cessário

DESCRIÇÃO

Constituintes

- Folha da porta de madeira (e=35mm), núcleo sarrafeado maciço (sólido) e capa em ambas as faces com painel de madeira compensada (e=3mm):
 - PM-82: 111x211cm;
 - PM-83: 101x211cm;
 - PM-85: 121x211cm.
- Espécies de madeira, conforme Classificação de Uso G1-C1, construção leve - esquadria, constante da ficha G1 Gestão de Madeira do Catálogo de Serviços.
- Trilho:
 - Trilho de alumínio com pintura eletrostática em tinta em pó; largura total: 31 a 34mm, altura total: 33 a 43mm;
 - Suportes para trilho, fixados com parafusos autoatarraxantes, galvanizados, cabeça panela, fenda philips, Ø 6mm e comprimento 75mm.
- Batente:
 - Tubo quadrado de alumínio 1 1/2" (e= 1,58mm) fixado com parafusos autoatarraxantes, galvanizados, cabeça panela, fenda philips, Ø 6mm e comprimento 75mm;
 - Tapa furos plástico 12mm colados com silicone.

Acessórios

- Fechadura para porta de correr, tipo sanitário, ou tipo externa (conforme aplicação), de aço, distância de broca 55mm, com trinco tipo "bico de papagaio", roseta com acabamento cromado.
- Kit deslizante com amortecimento, para portas com até 80kg:
 - 2 carros deslizantes;
 - 2 amortecedores;
 - 2 suportes de fixação;
 - 1 guia inferior.
- Canaleta guia: perfil "U" em alumínio 1/2"x1".
- Puxadores verticais, conforme Ficha S17.02 do Catálogo de Serviços.
- Placa de sinalização conforme fichas SI-01 ou SI-04 do Catálogo de Componentes (pago em outro serviço); exceto quando a porta for instalada no lado interno do ambiente - ver aplicação.

Acabamentos

- Folha da porta:
 - Pintura esmalte sintético *standard* ou esmalte a base de água na cor especificada em projeto.
- Batente e trilho:
 - Pintura eletrostática em tinta em pó, acabamento liso e brilhante, pré-pintado.

Protótipo comercial

- Folha da porta:
 - Fabricantes cadastrados no CADMADEIRA.
- Puxadores verticais:
 - Ver Ficha S17.02 do Catálogo de Serviços.
- Fechadura com roseta, trinco "bico de papagaio":
 - Tipo sanitário (somente em sanitários):
 - » AROUCA (código 6545);
 - » LA FONTE (código 4021 S).
 - Tipo externa (somente para hall de elevador):
 - » AROUCA (código 6945 LC);
 - » LA FONTE (código 222 N S).
- Trilho 3m:
 - ROMETAL - RO 82 Top (cód.: RM-003);
 - HAFELE - Slido D-Line11 80P (cód.: 940.43.931).

- Suporte para trilho:
 - ROMETAL (cód.: ART.370);
 - HAFELE (cód.: 940.42.061).
- Kit deslizante com amortecimento:
 - ROMETAL - RO 82 Top (cód.: 1157);
 - HAFELE - Slido D-Line11 80P (cód.: 940.83.008).
- Perfil "U" em alumínio 1/2"x1":
 - MUNDIAL ALUMÍNIO (ref.: PU344);
 - CANTOMETAL (ref.: U 1/2x1).
- Batente:
 - ALPEX (ref.: PERFIL TUBULAR RET. 3 X 1.1/2 X 1/16);
 - IMPÉRIO DOS METAIS;
 - SHOCK METAIS.

APLICAÇÃO

- Em sanitários e vestiários acessíveis (fechadura interna) ou halls de elevador (fechadura externa), de uso preferencial ou restrito a pessoas com deficiência física ou com mobilidade reduzida; conforme indicação em projeto.

Observações:

- Indicar placa de sinalização na porta (SI-01 ou SI-04), exceto quando a porta for instalada no lado interno do ambiente. Neste caso indicar placa de sinalização na parede (SI-02);
- Indicar placa de sinalização na parede (SI-07);
- Ver também **Manual do Sistema de Sinalização para Edificações Escolares**.

EXECUÇÃO

- Cortar o trilho e o batente de acordo com as respectivas medidas indicadas no projeto e eliminar eventuais arestas ou rebarbas.
- Os trilhos devem ser instalados de acordo com as instruções do fabricante com o alinhamento e nível perfeitos para não comprometer o deslizamento da folha da porta.

FICHAS DE REFERÊNCIA

Catálogo de Componentes

Ficha	SI-01	Placa 20x20cm (porta)
Ficha	SI-02	Placa 20x20cm (parede)
Ficha	SI-04	Placa 70x20cm (porta)
Ficha	SI-07	Placa 50x6cm (parede)

Catálogo de Serviços

Ficha	G1	Gestão de Madeira
Ficha	S14	Pintura
Ficha	S14.09	Tinta esmalte sintético standard
Ficha	S14.19	Fundos para madeira
Ficha	S14.21	Tinta esmalte à base de água
Ficha	S17.01	Ferragens para porta
Ficha	S17.02	Puxadores para porta acessível

RECEBIMENTO

- O serviço pode ser recebido, se atendidas todas as condições de especificação, projeto, fornecimento e execução.
- A aceitação do lote se fará mediante a comprovação documental da origem da madeira, exigindo-se:
 - Notas fiscais;
 - Declaração de emprego apenas de produtos e subprodutos de madeira de origem exótica ou de origem nativa da flora brasileira adquirida de pessoas jurídicas cadastradas no CADMADEIRA;
 - Comprovante de cadastramento do fornecedor perante o CADMADEIRA (a situação cadastral do fornecedor deverá ser conferida eletronicamente).
- Aferir as especificações de todos os itens.
- Folha da porta:

- Espécie botânica:
 - » Conferir a espécie da madeira utilizada, de acordo com a Classificação de Uso constante da ficha G1 Gestão de Madeira, do Catálogo de Serviços;
 - » A Fiscalização poderá, a seu critério, requerer a identificação da espécie botânica da madeira e os resultados de ensaios físico-mecânicos. As amostras, retiradas aleatoriamente do mesmo lote, deverão ser avaliadas em laboratório.
- Verificar a inexistência de fungos, apodrecimentos ou furos de insetos;
- Verificar, auditivamente, com leves batidas em vários pontos da superfície da folha da porta, a especificação do núcleo sarrafeado maciço (sólido);
- Rejeitar peças empenadas, desniveladas, fora de prumo ou de esquadro;
- Batente, trilho e suportes de fixação:
 - Aferir as especificações e protótipo comercial;
 - Verificar a correta instalação e funcionamento;
 - O acabamento deve estar livre de rebarbas, arestas ou quaisquer imperfeições que possam se tornar cortantes.
- Acessórios:
 - Aferir as especificações e protótipo comercial;
 - Verificar a correta instalação e funcionamento;
 - Puxadores verticais: verificar altura e posicionamento de fixação;
- Verificar a ausência de falhas na pintura ou quaisquer defeitos decorrentes do manuseio.
- O funcionamento da porta deverá ser verificado após a completa secagem da pintura e subsequente lubrificação, não podendo haver jogo causado por folgas, nem dificuldade no seu deslizamento, que deverá ser suave.
- Verificar, no limite máximo de abertura;
 - O espaço entre o puxador interno e a alvenaria deve ter 4cm, no mínimo;
 - O vão luz deve ter, no mínimo:
 - » 80cm para PM-83;
 - » 90cm para PM-82;
 - » 100cm para PM-85.
- Testar o amortecedor de impacto lançando a porta em ambas as direções.

SERVIÇOS INCLUÍDOS NOS PREÇOS

- Folha da porta.
- Batente, trilho e suportes de fixação.
- Acessórios (ferragens, inclusive puxadores).

Observação:

- Os seguintes itens serão pagos em outros serviços:
 - » Pintura de acabamento;
 - » Placas de sinalização.

CRITÉRIOS DE MEDIÇÃO

- un. — por unidade instalada.

LEGISLAÇÃO

- Decreto Estadual nº 53.047, de 02 de junho de 2008 - cria o CADMADEIRA e estabelece procedimentos na aquisição de produtos de subprodutos de madeira de origem nativa pelo Governo do Estado de São Paulo.

NORMAS

- NBR 9050: 2020 - Acessibilidade a edificações, mobiliário, espaços e equipamentos urbanos.

Observação:

- As edições indicadas estavam em vigor no momento desta publicação. Como toda norma está sujeita a revisão, recomenda-se verificar a existência de edições mais recentes das normas citadas.

Componentes

PM-82 PM-83 PM-85

Porta de correr acessível

[Sarrafeada

Maciça p/ pintura]

PM-82[L = 111cm]

PM-83[L = 101cm]

PM-85[L = 121cm]

Revisão 5
Data 13/06/24

Página

7/7

Código de listagem

05.01.069

05.01.070

05.01.111



Atenção

Preserve a escala

Quando for imprimir, use folhas A4 e desabilite a função "Fit to paper"

Respeite o Meio Ambiente.

Imprima somente o necessário