



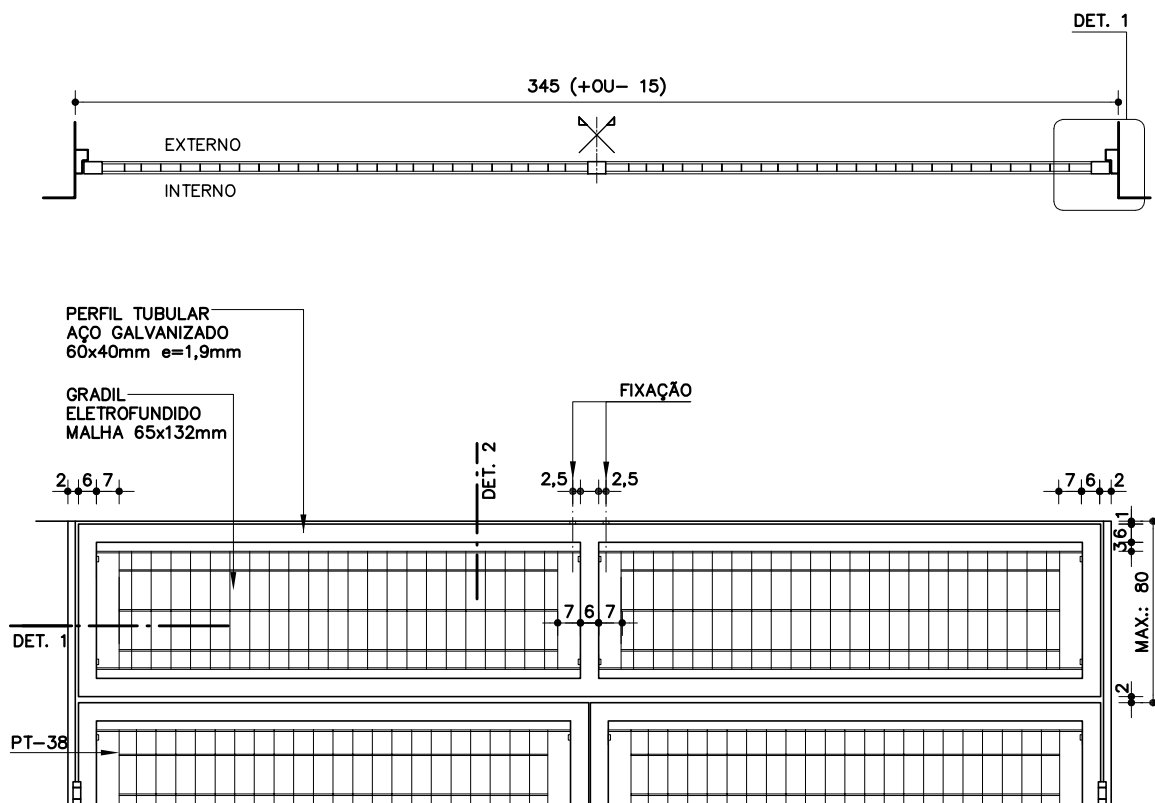


VISTA INTERNA PT-40

(PARA PT-38)
ESC. 1:25

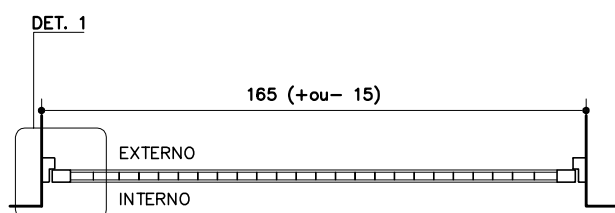

PLANTA PT-40

(PARA PT-39)
ESC. 1:25

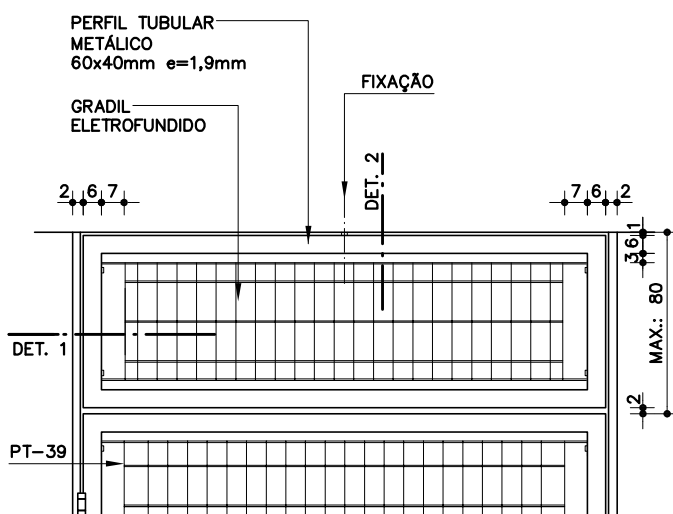

VISTA INTERNA PT-40

(PARA PT-39)
ESC. 1:25

PT-40

Bandeira em gradil eletrofundido

(uso interno)

$h = \text{máx. } 80 \text{ cm}$

Revisão	1
Data	20/09/10

Página

 $\frac{1}{4}$ **Código de listagem**

0602062



Atenção

Preserve a escala
Quando for imprimir, use
folhas A4 e desabilite a
função "Fit to paper"

Respeite o Meio Ambiente.
Imprima somente o necessário

PT-40

Bandeira em gradil eletrofundido

(uso interno)
h=máx. 80cm

Revisão 1
Data 20/09/10


Página
2/4


Código de listagem

0602062

Atenção
Preserve a escala
Quando for imprimir, use
folhas A4 e desabilite a
função "Fit to paper"


Respeite o Meio Ambiente.
Imprima somente o ne-
cessário

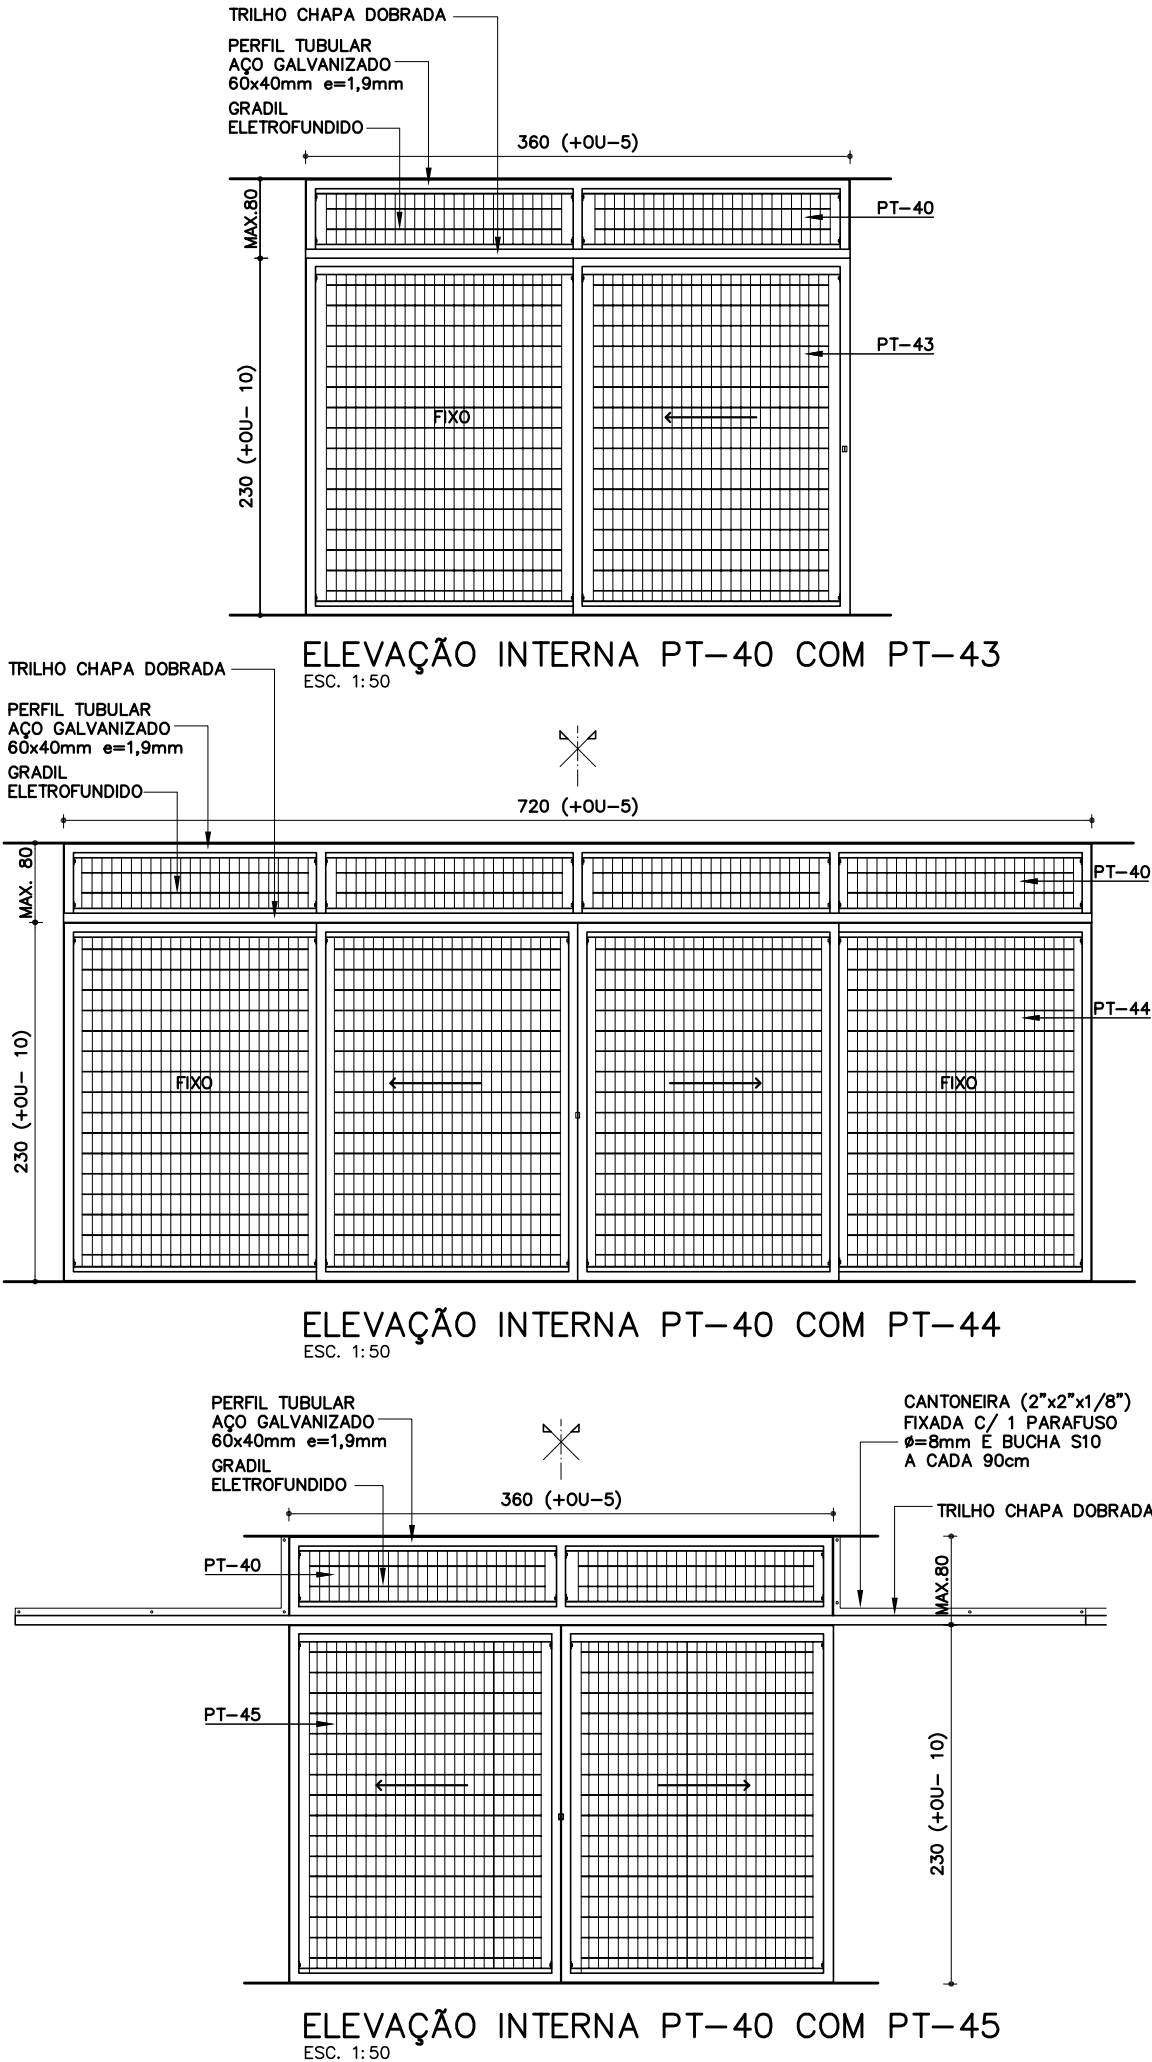

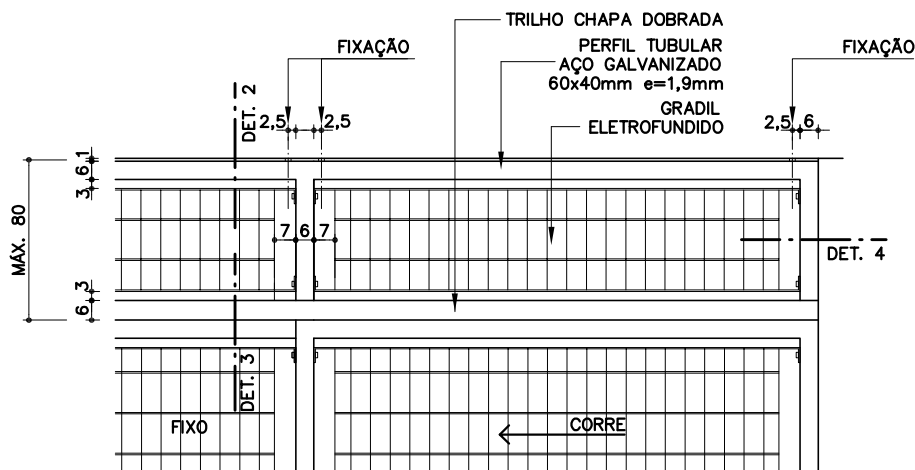


APLICAÇÃO PARCIAL PT-40

(PARA PT-43, PT-44 OU PT-45)
ESC. 1: 25

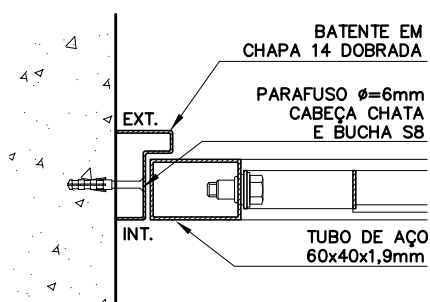


DETALHE 1

(PARA PT-38 E PT-39)

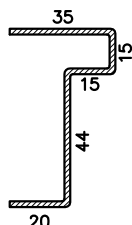


DETALHE DO BATENTE

(PARA PT-38 E PT-39)
ESC. 1: 2,5

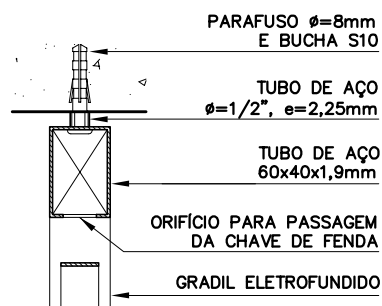


DETALHE 2

ESC. 1: 5

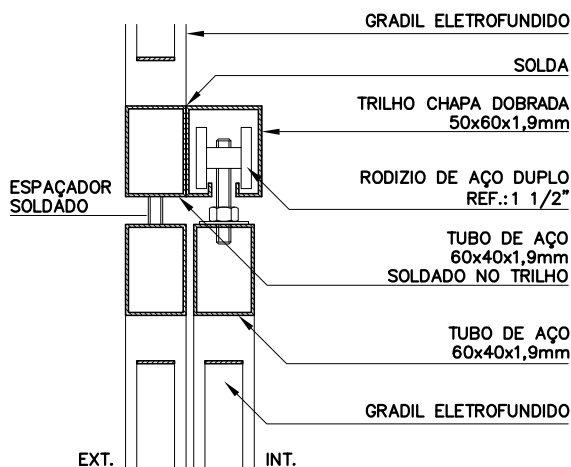

DETALHE 3

(PARA PT-43, PT-44 E PT-45)
ESC. 1: 5

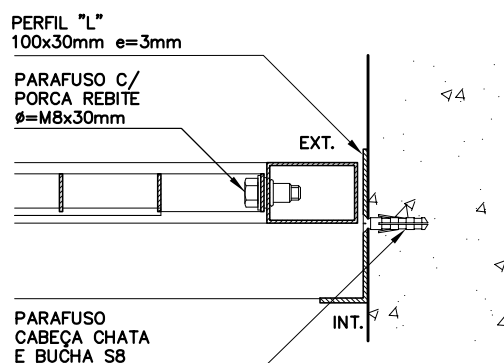

DETALHE 4

(PARA PT-43, PT-44 E PT-45)
ESC. 1: 5

PT-40

Bandeira em gradil eletrofundido

(uso interno)
h=máx. 80cm

Revisão 1
Data 20/09/10

Página

3/4

Código de listagem

0602062



Atenção

Preserve a escala
Quando for imprimir, use
folhas A4 e desabilite a
função "Fit to paper"

Respeite o Meio Ambiente.
Imprima somente o ne-
cessário

PT-40

Bandeira em gradil eletrofundido

(uso interno)

h=máx. 80cm

Revisão 1
Data 20/09/10Página
4/4

Código de listagem

0602062



Atenção

Preserve a escala
Quando for imprimir, use
folhas A4 e desabilite a
função "Fit to paper"

Respeite o Meio Ambiente.
Imprima somente o ne-
cessário

DESCRIÇÃO

Constituintes

- Bandeira:
 - Quadros em tubo retangular de aço galvanizado a fogo, de 60x40x1,9mm;
 - Gradil completo confeccionado em perfis de aço carbono soldados pelo processo de eletrofusão e tratados com galvanização a fogo, com acabamento em pintura eletrostática à base de poliéster em pó (na cor especificada em projeto), composto de painel em malha retangular (65x132mm) formada por barras chatas portantes (25x2mm) e fio de ligação redondo ($\varnothing=4,8\text{mm}$) com moldura em barra chata de 25x4,76mm;
 - Batente em chapa 14 dobrada, de aço galvanizado (para PT-38 e PT-39);
 - Batente em chapa dobrada, de aço galvanizado, 100x30mm, e=3mm (PT-43, PT-44 e PT-45).

Acessórios

- Parafusos galvanizados $\varnothing=6\text{mm}$, cabeça chata, com buchas de nylon S8.
- Parafusos galvanizados $\varnothing=8\text{mm}$, cabeça panela, com buchas de nylon S10.
- Conjunto de fixação do gradil composto de porca rebite (RIVKLE M8) e parafuso cabeça sextavada $\varnothing=M8 \times 30\text{mm}$ com arruela, em aço galvanizado (4 conjuntos por painel).

Acabamentos

- Pintura esmalte sintético sobre fundo para galvanizados, exceto gradil que deverá ser fornecido com pintura eletrostática à base de poliéster em pó.

Protótipo comercial

- Gradil completo:
 - METALGRADE ("Artis" - cores: branco, cinza, preto, azul ou verde)
- Parafusos galvanizados e buchas de nylon:
 - FISCHER
- Galvanização a frio:
 - Ver ficha S14.17 do Catálogo de Serviços
- Porca rebite:
 - RIVKLE (clássico cabeça plana)

APLICAÇÃO

- Em áreas internas, conjugado com portão PT-38 ou PT-39.
- **Nota:** A cor da pintura deverá ser especificada em projeto.

EXECUÇÃO

- Bandeira:
 - Bater os pontos de solda e eliminar todas as rebarbas nas emendas e cortes dos tubos, barras e chapas;
 - Todos os locais onde houver pontos de solda e/ou corte, devem estar isentos de poeira, gordura, graxa, sabão, ferrugem ou qualquer contaminante (recomenda-se limpeza mecânica com lixa de aço ou jato abrasivo grau 2) para receber galvanização a frio (tratamento anticorrosivo composto de zinco);
 - As soldas dos tubos devem ser contínuas em toda extensão da área de contato;
 - Antes da aplicação do fundo para galvanizados, toda superfície metálica deve estar completamente limpa, seca e desengraxada;
 - O gradil deve ser instalado observando-se os espaçamentos superior e inferior conforme o desenho, não deve haver folgas entre os gradis e os quadros.

FICHAS DE REFERÊNCIA

Catálogo de Componentes

Ficha	PT-38	Portão em gradil eletrofundido (345x230cm)
Ficha	PT-39	Portão em gradil eletrofundido (165x230cm)
Ficha	PT-43	Portão de correr em gradil eletrofundido (360x230cm)
Ficha	PT-44	Portão de correr em gradil eletrofundido (720x230cm)
Ficha	PT-45	Portão de correr em gradil eletrofundido (372x230cm)

Catálogo de Serviços

Ficha	S14	Pintura
Ficha	S14.09	Tinta esmalte sintético
Ficha	S14.17	Galvanização
Ficha	S14.18	Fundos para metais

RECEBIMENTO

- O serviço pode ser recebido se atendidas todas as condições de projeto, fornecimento e execução.
- Tubos, barras, perfis e chapas devem ter, necessariamente, as bitolas indicadas.
- Não serão aceitos portões com rebarbas, empenados, desnivelados, fora de prumo ou de esquadro, ou que apresentem quaisquer defeitos decorrentes do manuseio, transporte ou montagem.
- Verificar se as soldas nos tubos estão contínuas em toda a extensão da superfície de contato. Exigir certificado de galvanização a fogo, emitido pela empresa galvanizadora, para todos os constituintes metálicos ou nota fiscal discriminada do fornecedor.
- Verificar o tratamento dos pontos de solda e corte com galvanização a frio.
- Verificar a aderência e a uniformidade da camada de pintura, atentando para que não apresentem falhas, bolhas, irregularidades ou quaisquer defeitos decorrentes da fabricação e do manuseio.
- Gradil:
 - Verificar as especificações; exigir certificado de garantia contra oxidação (mínimo de 5 anos);
 - Verificar o prumo, o nível, o alinhamento e a fixação dos painéis aos quadros. Não serão aceitas peças empenadas, desniveladas, fora de prumo ou de esquadro;
 - Verificar a aderência e a uniformidade da camada da pintura, atentando para que não apresentem falhas, bolhas, irregularidade ou quaisquer defeitos decorrentes da fabricação e do manuseio.

SERVIÇOS INCLUÍDOS NOS PREÇOS

- Bandeira completa executada e instalada.
- Galvanização a frio, fundo para galvanizados e pintura.

CRITÉRIOS DE MEDIÇÃO

- m^2 — pela área da bandeira instalada.