
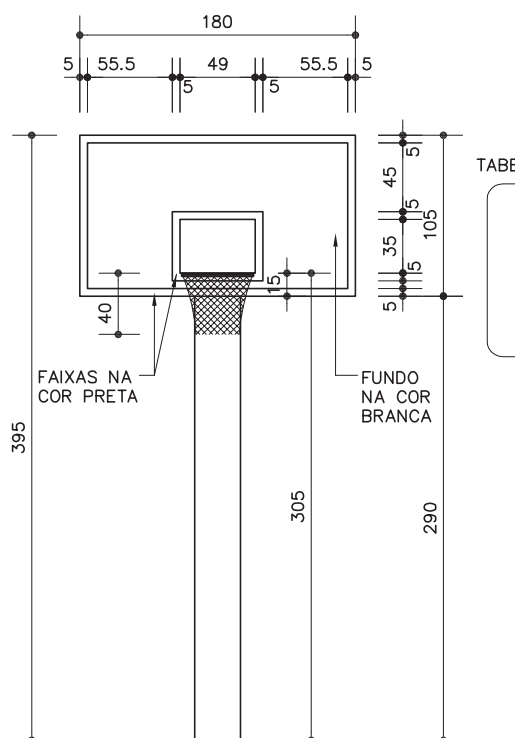



PLANTA

ESC. 1:50

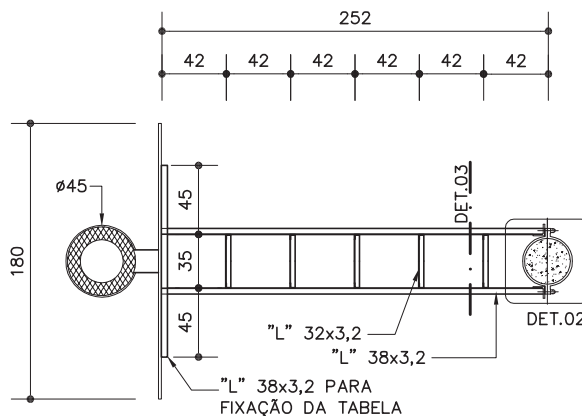


VISTA FRONTAL

ESC. 1:50

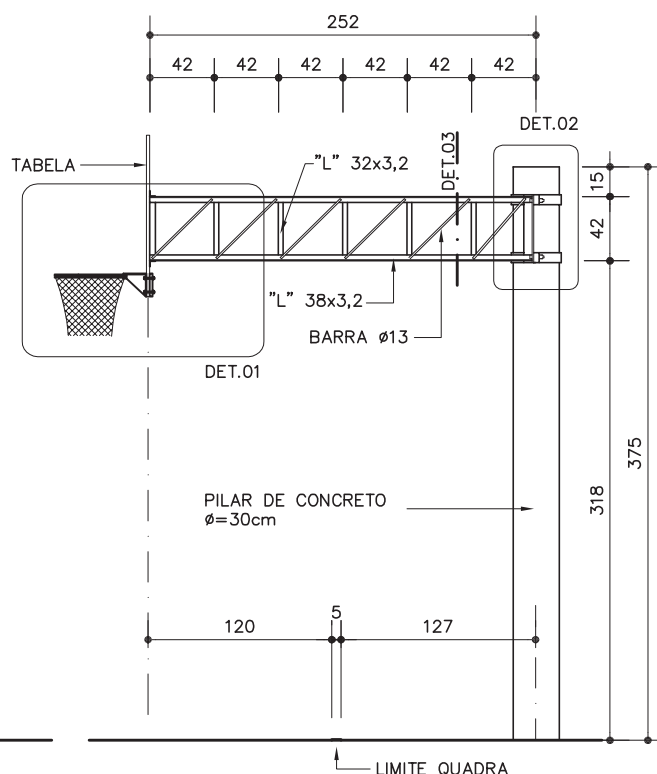


ELEVAÇÃO

ESC. 1:50

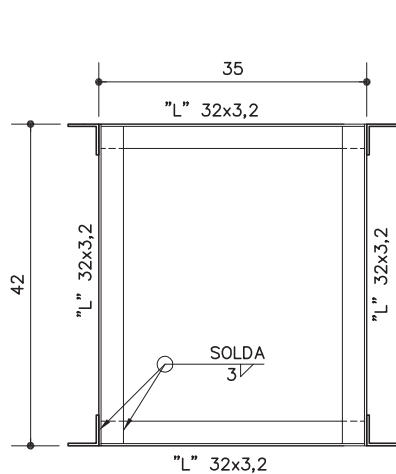

DETALHE 3

ESC. 1:10

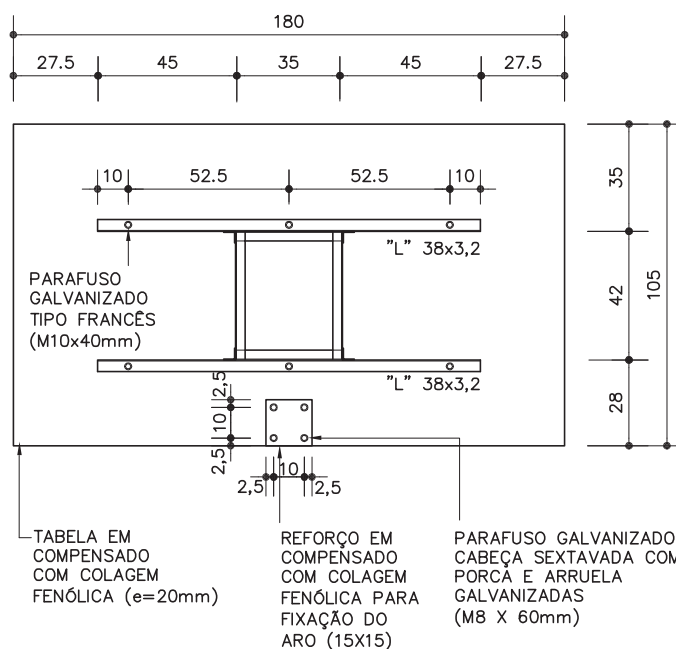

VISTA POSTERIOR DA TABELA

ESC. 1:25

QE-37
QE-38

Tabela de basquete

(Fundação de broca de concreto)

QE-37 descoberta
QE-38 coberta

Revisão	1
Data	22/09/17

Página

 $\frac{1}{4}$ **Código de listagem**

1604025

0603115



Atenção

Preserve a escala
Quando for imprimir, use folhas A4 e desabilite a função "Fit to paper"

Respeite o Meio Ambiente.
Imprima somente o necessário

QE-37 QE-38

Tabela de basquete

[Fundação de broca de concreto]

QE-37 descoberta

QE-38 coberta

Revisão 1
Data 22/09/17

Página
3/4

Código de listagem


1604025
0603115



Atenção


Preserve a escala
Quando for imprimir, use
folhas A4 e desabilite a
função "Fit to paper"

Respeite o Meio Ambiente.
Imprima somente o ne-
cessário

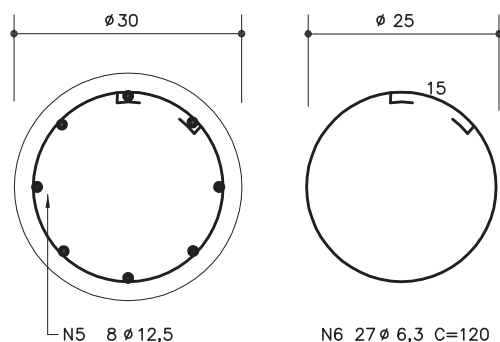

PILAR

ESC. 1:10

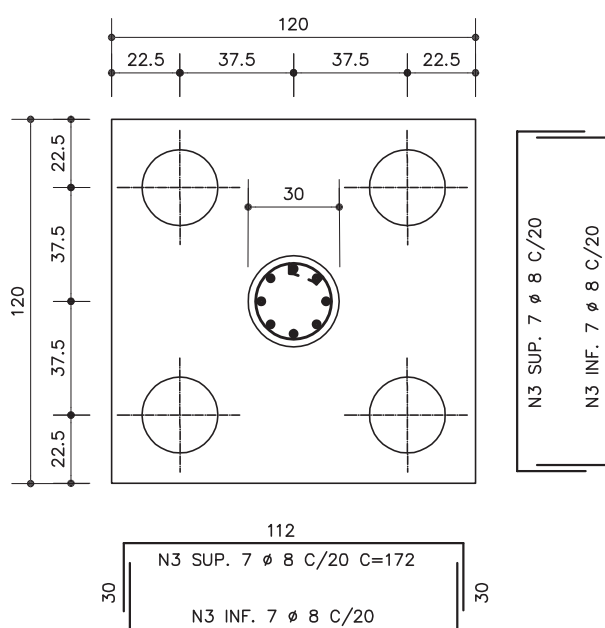


BLOCO DE FUNDAÇÃO E PILAR

ESC. 1:25

OBS:

COBRIMENTOS DAS ARMADURAS:
- BLOCO DE FUNDAÇÃO = 4cm
- PILAR = 2,5cm

CONCRETO: fck 25 MPa
AÇO: CA-50

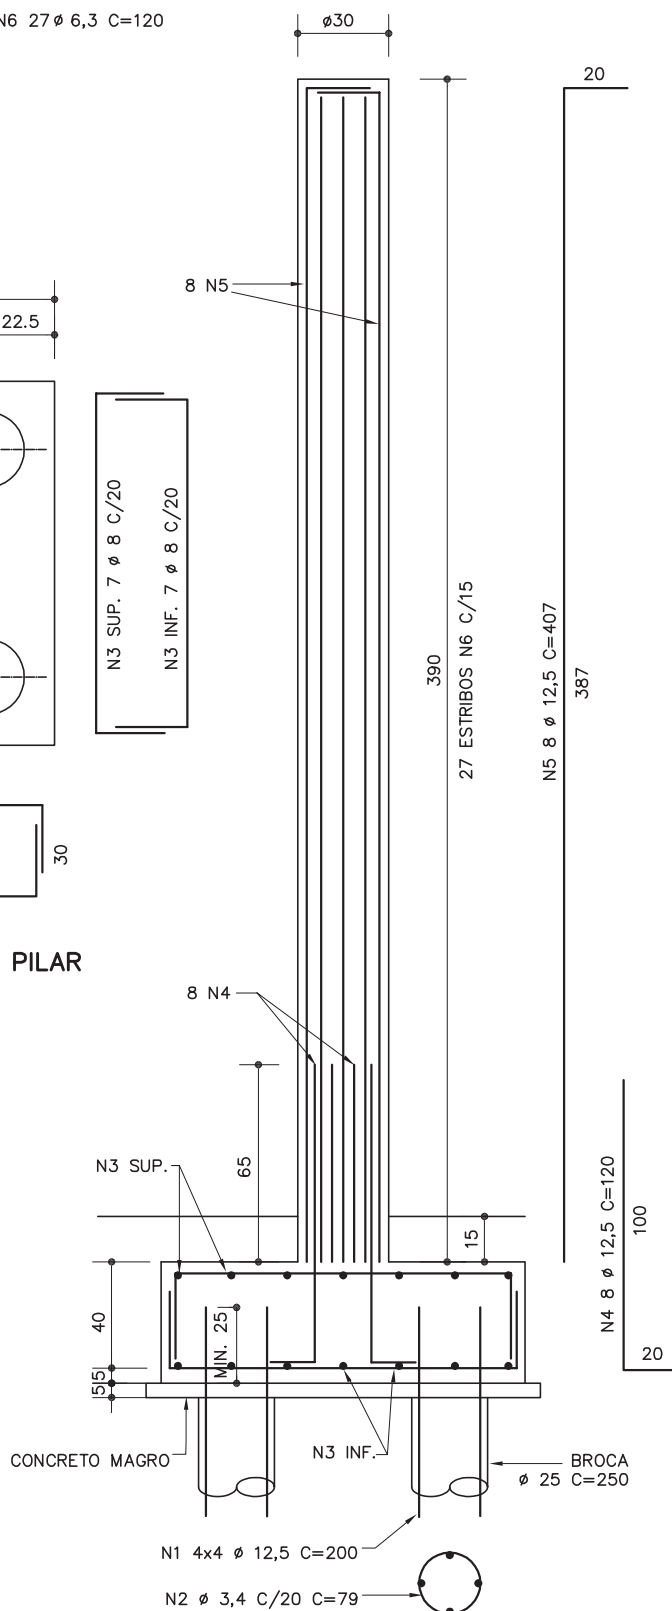

QE-37
QE-38

Tabela de basquete

(Fundação de broca de concreto)
QE-37 descoberta
QE-38 coberta

Revisão 1
Data 22/09/17

Página
4/4

Código de listagem

1604025
0603115


Atenção
Preserve a escala
Quando for imprimir, use
folhas A4 e desabilite a
função "Fit to paper"

Respeite o Meio Ambiente.
Imprima somente o ne-
cessário

DESCRIÇÃO
Constituintes

- Fundação:
 - 4 brocas de diâmetro 25cm e comprimento 2,50m;
 - Bloco de fundação de 1,20 x 1,20 x 0,45m;
 - Armação em aço CA-50 (bitolas indicadas no desenho).
- Pilar:
 - Concreto usinado, fck=25 MPa, utilizando cimento por-
tland de alto forno;
 - Armação em aço CA-50 (bitolas indicadas no desenho);
 - Fôrma tubular de papelão.
- Treliça:
 - Cantoneiras de abas iguais "L" em aço ASTM A-36: 1
1/2"x1/8" (38x3,2mm); 1 1/4"x1/8" (32x3,2mm) e 2
1/2"x3/8" (64x9,5mm);
 - Barra redonda em aço SAE 1020 de Ø=1/2" (13mm).
- Tabela/Cesto:
 - Tabela em chapa de compensado com colagem fenólica,
e=20mm e requadro com perfil metálico galvanizado "U"
ou "L";
 - Aro com diâmetro interno de 450mm em barra redonda
galvanizada de 16mm<Ø<20mm;
 - Rede em malha de nylon presa ao aro em 12 pontos, com-
primento entre 400 a 450mm;
 - Suporte em chapa de aço galvanizado, e=3/16".

Acessórios

- Fixação da treliça à coluna: braçadeiras em aço ASTM
A-36 de 64x13mm, parafusos ASTM A325 - Ø=1/2", ambos
galvanizados.
- Fixação da tabela à treliça: 6 parafusos tipo "francês"
(M10x40mm), porcas e arruelas galvanizados.

Acabamentos

- Treliça: galvanização a fogo e pintura esmalte sintético
sobre fundo para galvanizados.

Protótipo comercial

- Tabela de basquete:
 - DELFOS SISPORT (1029 - Padrão FDE)
 - PARDINI SPORTS (6760 - Padrão FDE)
 - POWER SPORTS (2090)
- Galvanização a fogo:
 - B.BOSCH
 - FOGAL
 - JOSITA
 - RIWAGAL
 - MARVITEC

APLICAÇÃO

- Em quadra de esportes com fundação direta.

EXECUÇÃO

- Concreto:
 - O bloco de fundação deve ser executado sobre um lastro
de concreto simples com espessura de 5cm;
 - No pilar, utilizar fôrma tubular de papelão;
 - A armadura deve ser colocada completamente limpa e
mantida afastada da fôrma por meio de espaçadores
plásticos industrializados, com dimensões que atendam
os cobrimentos nominais de 4cm para fundações e 2,5cm
para o pilar.
- Treliça:
 - Os componentes deverão ser montados com soldas con-
forme AWS em todo contorno dos perfis (solda contínua)
com mínimo de 3mm de perna, utilizando eletrodos
E70XX;

- Após montagem, a treliça deverá ser galvanizada a fogo;
- Toda a superfície metálica deve estar completamente
limpa, seca e desengraxada para receber fundo para galva-
nizado antes da pintura com esmalte sintético.

FICHAS DE REFERÊNCIA
Catálogo de Componentes

Ficha	QE-12 e QE-32	Quadra de esportes, piso de concreto armado, fundação direta
Ficha	QE-34	Quadra de esportes, piso com fibra de polipropileno corrugada, fundação direta

Catálogo de Serviços

Ficha	S3.01	Broca de concreto
Ficha	S4.01	Armadura
Ficha	S4.03	Concreto dosado em central
Ficha	S4.05	Fôrmas e cimbramento em madeira
Ficha	S14.17	Galvanização

RECEBIMENTO

- Pilar de concreto:
 - Verificar a locação, prumo e o alinhamento do pilar em
relação ao limite demarcatório da quadra;
 - Verificar, no concreto do pilar, a uniformidade na coloração,
textura homogênea e superfície sem ondulações, orifícios
ou pedras visíveis;
 - O serviço não pode ser recebido, em hipótese nenhuma,
se ocorrer afloramento da armadura na superfície do
concreto.
- Treliça:
 - Exigir o certificado de galvanização a fogo, emitido pela
empresa galvanizadora;
 - Verificar, visualmente, a aderência e a uniformidade da
camada de galvanização, através da ausência de bolhas e
irregularidades na espessura do revestimento;
 - Verificar a correta utilização de parafusos, porcas e arrue-
las galvanizados;
 - Verificar o acabamento da pintura, atentando para que não
apresente falhas ou quaisquer defeitos decorrentes do
manuseio.
- Tabela/Cesto:
 - Verificar marca e modelo da tabela;
 - Verificar o prumo da tabela e seu alinhamento em relação
ao limite demarcatório da quadra;
 - A superfície da tabela deverá apresentar-se regular, sem
ondulações, rebarbas, rebaixos, falhas, orifícios, etc.

SERVIÇOS INCLUÍDOS NO PREÇO

- Escavação, apiloamento e reaterro.
- Lastro de concreto simples.
- Fundação e pilar de concreto.
- Treliça galvanizada e pintada.
- Tabela completa, inclusive cesto.
- Acessórios de fixação, galvanizados.

CRITÉRIOS DE MEDIÇÃO

- un. — por unidade executada.