



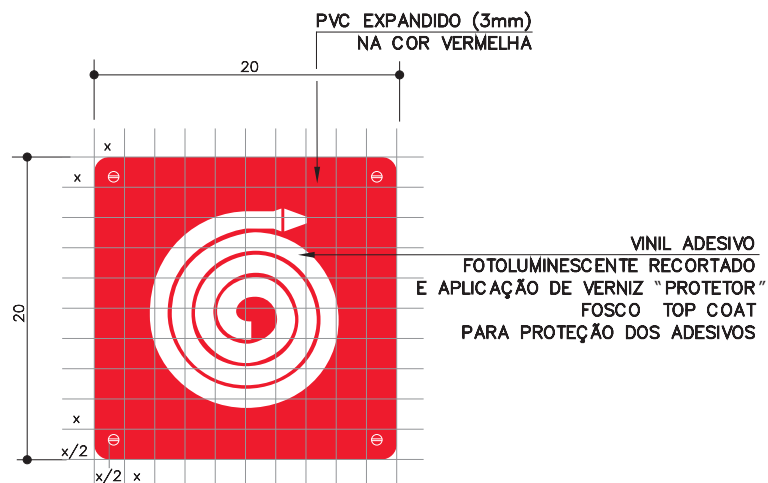

EXEMPLO

ESC.: 1:5

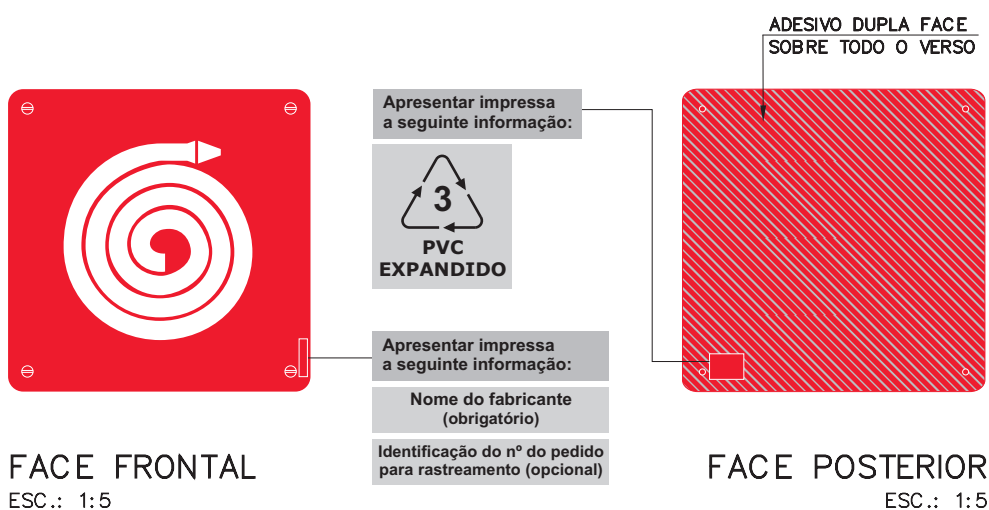


FACE FRONTAL

ESC.: 1:5


FACE POSTERIOR

ESC.: 1:5

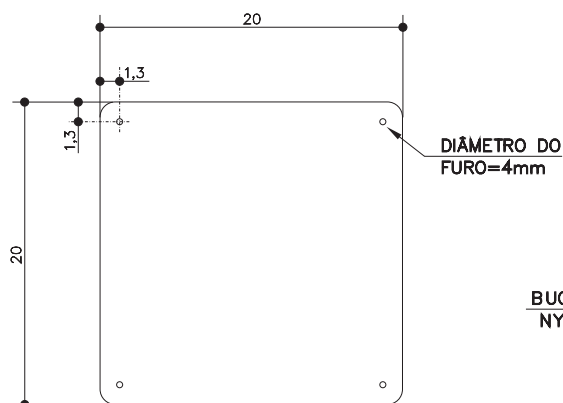

DETALHE DA FURAÇÃO

ESC.: 1:5

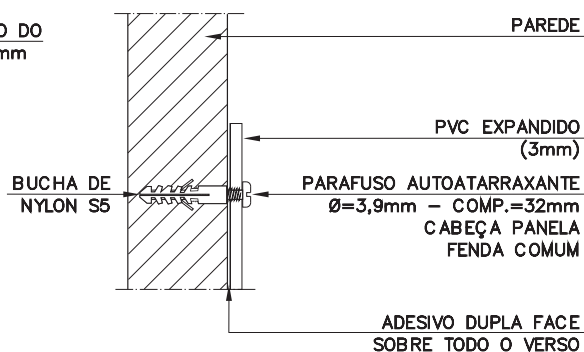

DETALHE DA FIXAÇÃO

ESC.: 1:2

SI-03

Placa 20 x
20cm
acabamento
fotolumines-
cente
[parede]

Revisão 1
Data 29/03/19

Página
1/3

Código de listagem

1618072



Atenção

Preserve a escala
Quando for imprimir, use
folhas A4 e desabilite a
função "Fit to paper"

Respeite o Meio Ambiente.
Imprima somente o ne-
cessário

FDE FUNDAÇÃO PARA O
DESENVOLVIMENTO
DA EDUCAÇÃO

medidas em cm

SI-03

**Placa 20 x 20cm
acabamento
fotoluminescente**
[parede]

Revisão	1
Data	29/03/19

Página
2/3

Código de listagem


1618072



Atenção

Preserve a escala
Quando for imprimir, use
folhas A4 e desabilite a
função "Fit to paper"

Respeite o Meio Ambiente.
Imprima somente o necessário

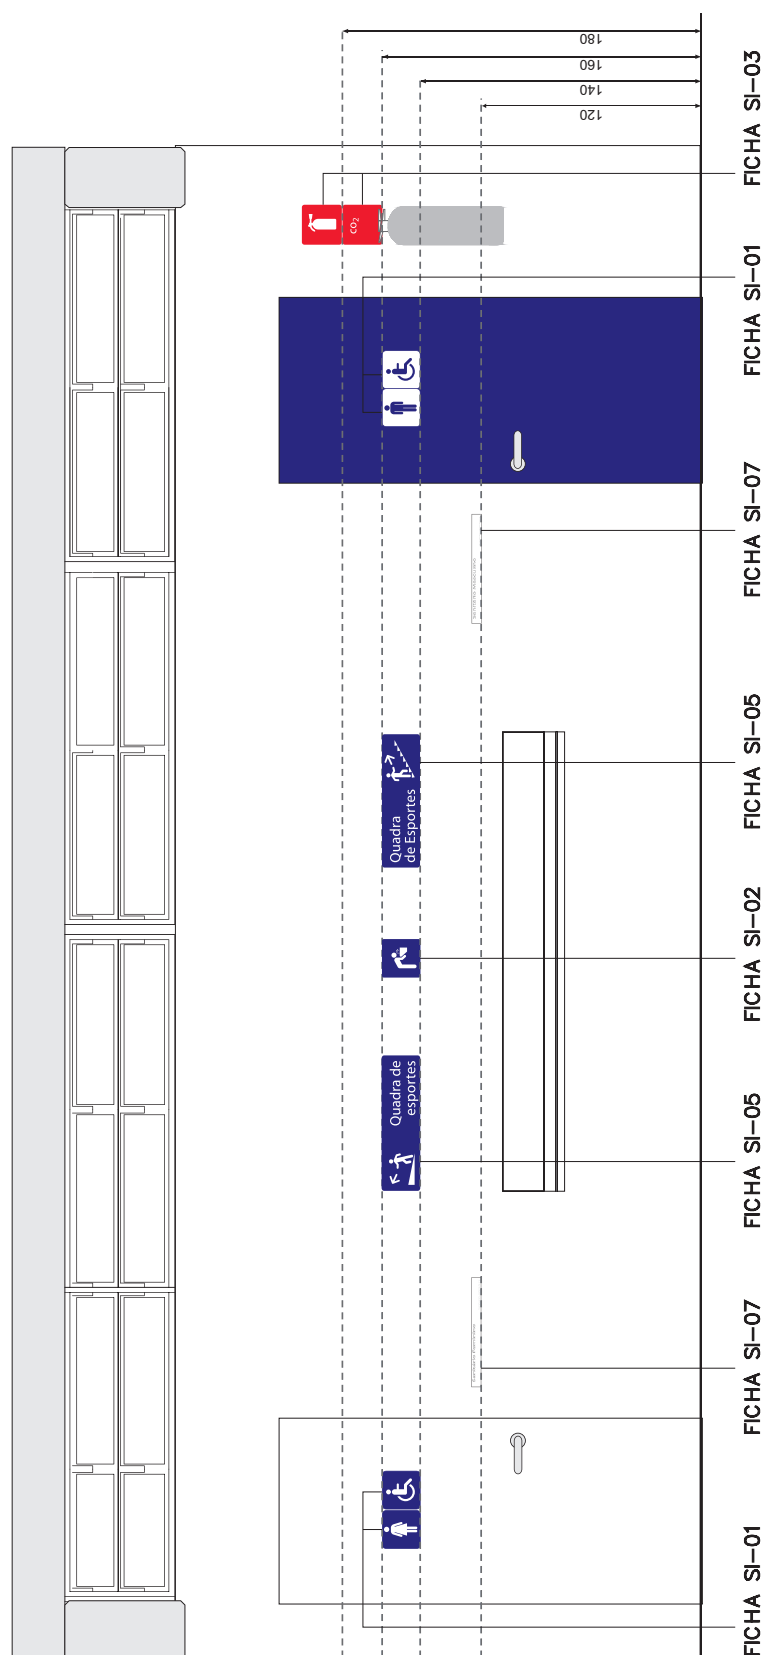

EXEMPLO DE APLICAÇÃO
CIRCULAÇÕES JUNTO AOS SANITÁRIOS E BEBEDOUROS
SEM ESCALA

medidas em cm

DESCRIÇÃO

Constituintes

- Base em PVC expandido com espessura de 3mm, na cor VERMELHA. Dimensões acabadas 20cm (largura) x 20cm (altura). Cantos arredondados conforme projeto.
- Texto e pictograma em vinil adesivo fotoluminescente, recortados por plotter de recorte, aplicados na face frontal. Fontes para textos: família Myriad.
- Aplicação de verniz protetor fosco "Top Coat" para proteção dos adesivos fotoluminescentes.
- Deve ser impresso na face frontal o nome do fabricante (obrigatório) e a identificação do número do pedido para rastreamento (opcional); na face posterior deve ser impresso o símbolo internacional de reciclagem, apresentando o número identificador do polímero.
- Adesivo dupla face aplicado sobre todo o verso.
- 4 parafusos autoatarraxantes de aço, zincados, cabeça panela, fenda comum, diâmetro de 3,9mm x 32mm de comprimento.
- 4 buchas de Nylon tipo S5.

Referência de cor

- Vermelho:
 - ref. CMYK - C: 0 M:100 Y:90 K:0

Protótipo comercial

- Adesivo dupla face:
 - 3M SCOTCH YR-9625
- Parafusos:
 - CISER
- Buchas de nylon:
 - FISCHER

Prestadores de serviço homologados

- SIGNOSINAL

APLICAÇÃO

- Em paredes de ambientes internos, conforme indicação em projeto.

Obs.1: Os projetos de sinalização deverão ser elaborados em consonância com as orientações do 'Manual do Sistema de Sinalização para Edificações Escolares' e em conformidade com os critérios da norma NBR 9050.

Obs.2: Cada projeto de sinalização deverá ser acompanhado da respectiva 'Planilha de Quantificação e Especificação' (SI-PQ).

EXECUÇÃO

- A execução das placas deve ser realizada em conformidade com o solicitado na 'Planilha de Quantificação e Especificação' (SI-PQ).
- Para a impressão, devem ser utilizadas as artes correspondentes aos projetos gráficos de cada placa.
- Recorte e furação através de equipamento de corte tipo "Router".

Obs.: Os arquivos digitais referentes às artes das placas devem ser solicitados pelo fabricante à Supervisão de Especificação Técnica da Edificação da Gerência de Inovação e Tecnologia para a Edificação.

INSTALAÇÃO

- A instalação das placas deve ser realizada em conformidade com o projeto de sinalização e com as orientações constantes do 'Manual do Sistema de Sinalização para Edificações Escolares'.
- Altura de instalação: a borda inferior da placa deve estar a 160cm do piso.

- Posicionamento: conforme indicação em projeto.

Obs.: Quando houver placa de texto explicativo (E4, E6, E7, E8, E9 e E10), esta deve ser instalada abaixo da placa de sinalização de equipamento, mantendo o mesmo alinhamento (a borda inferior deve estar aproximadamente a 180cm do piso).

- Fixação e colagem:

- confirmar texto e pictograma e local de fixação de cada placa;
- preparar e limpar previamente a superfície que receberá a placa;
- fixar a base na parede com a fita dupla face e com os parafusos (posicionamento de acordo com a furação pré-executada na base).

FICHAS DE REFERÊNCIA

Catálogo de Componentes

Ficha	SI-01	Placa 20 x 20cm (porta)
Ficha	SI-02	Placa 20 x 20cm (parede)
Ficha	SI-04	Placa 70 x 20cm (porta)
Ficha	SI-05	Placa 70 x 20cm (parede)
Ficha	SI-06	Placa 70 x 20cm (parede) - acabamento fotoluminescente (parede)
Ficha	SI-07	Placa 50 x 6cm - texto em relevo e transcrição em Braille (parede)
Ficha	SI-08	Placa 3 x 3cm - metálica em Braille (corrimão)
Ficha	SI-09	Placa 50 x 50cm (parede externa)
Ficha	SI-10	Placa 50 x 70cm (parede externa)
Ficha	SI-11	Sinalização horizontal para vaga acessível
Ficha	SI-PQ	Planilha de quantificação e especificação

RECEBIMENTO

- Confirmar texto e pictograma e local de fixação das placas com o projeto de sinalização.
- Verificar fixação e corte.
- Verificar altura, posicionamento, alinhamento e nivelamento.
- Verificar inexistência de rebarbas.

SERVIÇOS INCLUÍDOS NO PREÇO

- Fornecimento das placas.
- Furação.
- Adesivo dupla face.
- Parafusos e buchas.
- Instalação.

CRITÉRIOS DE MEDIÇÃO

- un. — por unidade instalada.

NORMAS

- NBR 9050:2004 - Acessibilidade a edificações, mobiliário, espaços e equipamentos urbanos.
- **Obs:** As edições indicadas estavam em vigor no momento desta publicação. Como toda norma está sujeita à revisão recomenda-se verificar a existência de edições mais recentes das normas citadas.

Componentes

SI-03

**Placa 20 x 20cm
acabamento
fotoluminescente
(parede)**

Revisão 1
Data 29/03/19

Página
3/3

Código de listagem
1618072



Atenção
Preserve a escala
Quando for imprimir, use
folhas A4 e desabilite a
função "Fit to paper"

Respeite o Meio Ambiente.
Imprima somente o necessário

FDE FUNDAÇÃO PARA O
DESENVOLVIMENTO
DA EDUCAÇÃO