


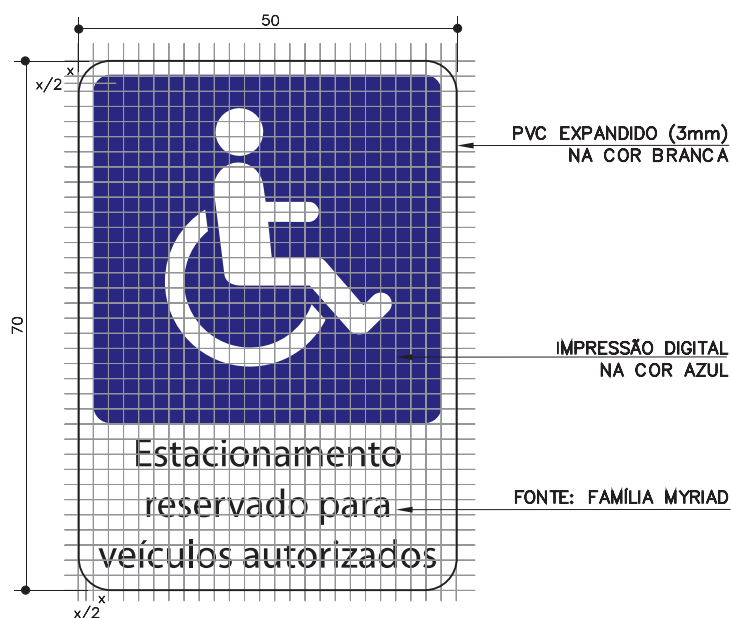


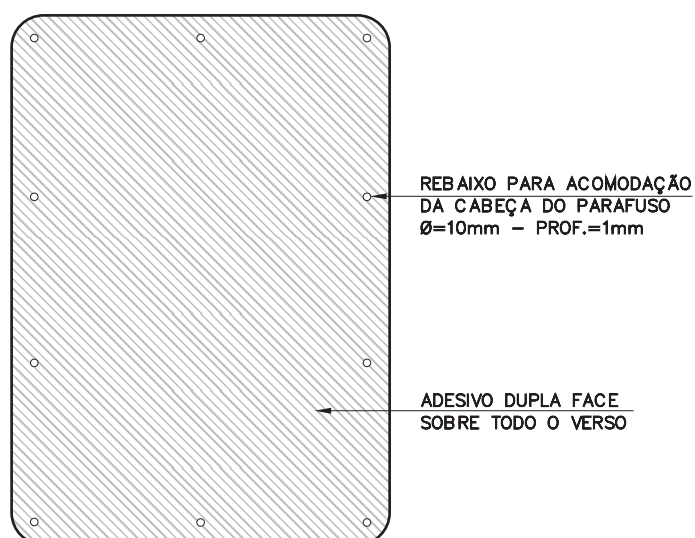

**SUPERFÍCIE – FACE FRONTAL**  
ESC.: 1:10

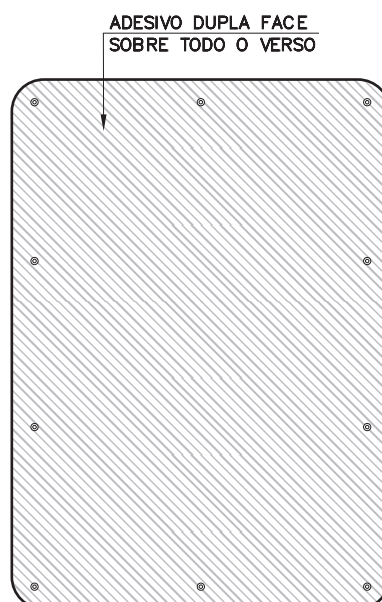

**SUPERFÍCIE – FACE POSTERIOR**  
DETALHE DO REBAIXO PARA ACOMODAÇÃO DA CABEÇA DO PARAFUSO  
ESC.: 1:10

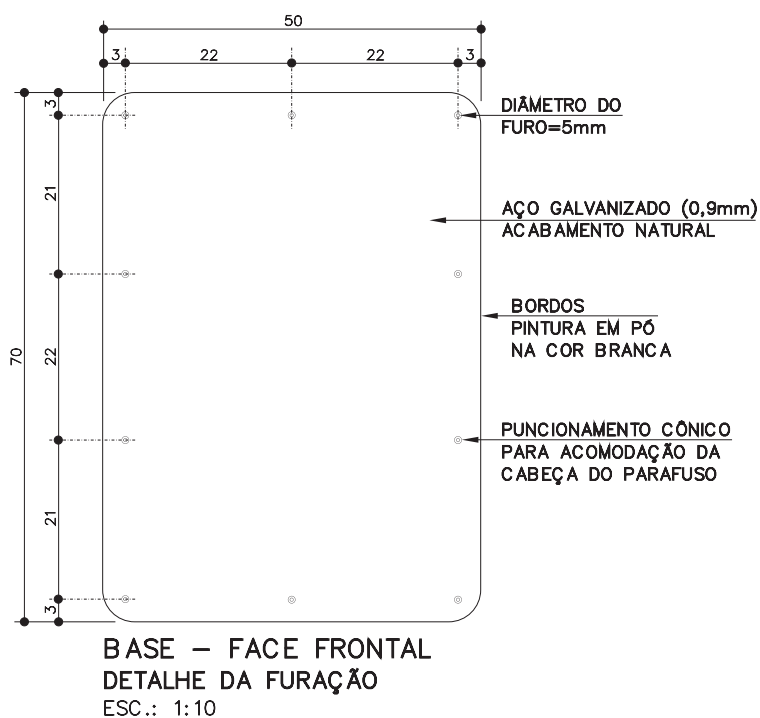

**BASE – FACE POSTERIOR**  
ESC.: 1:10

medidas em cm

## SI-10

**Placa 50 x 70cm**  
[parede externa]

Revisão 1  
Data 29/03/19

Página

1/4

**Código de listagem**

1618079



### Atenção

Preserve a escala  
Quando for imprimir, use  
folhas A4 e desabilite a  
função "Fit to paper"

Respeite o Meio Ambiente.  
Imprima somente o ne-  
cessário

SI-10

Placa 50 x 70cm  
(parede externa)




SUPERFÍCIE  
FACE FRONTAL  
ESC.: 1:10

Apresentar impressa a seguinte informação:




Apresentar impressa a seguinte informação:


Nome do fabricante  
(obrigatório)  
Identificação do nº do pedido  
para rastreamento (opcional)

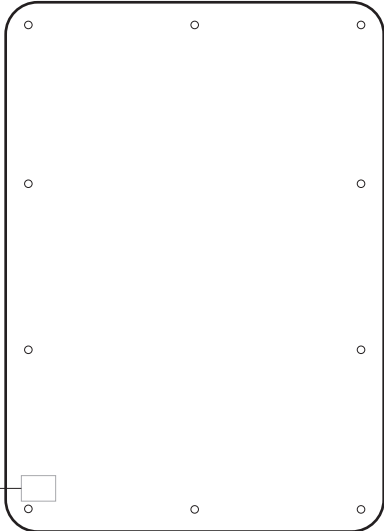


SUPERFÍCIE  
FACE POSTERIOR  
ESC.: 1:10

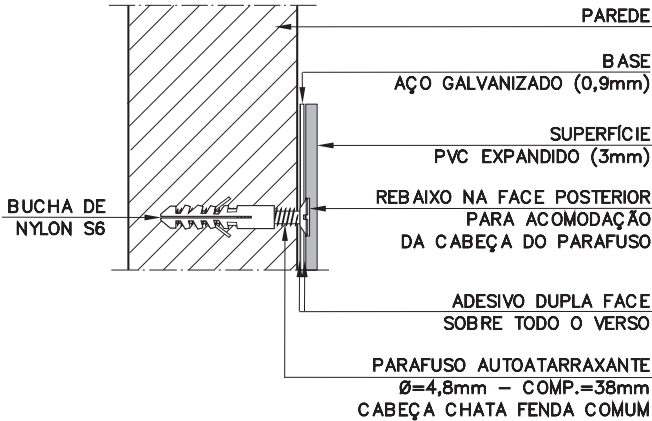

DETALHE DA FIXAÇÃO  
ESC.: 1:2

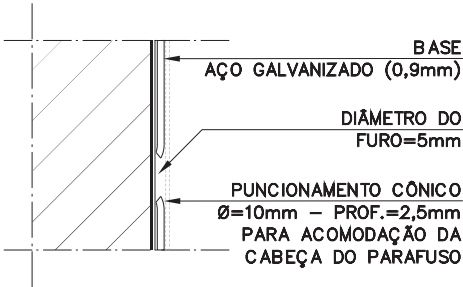

DETALHE  
FURAÇÃO NA BASE  
ESC.: 1:1

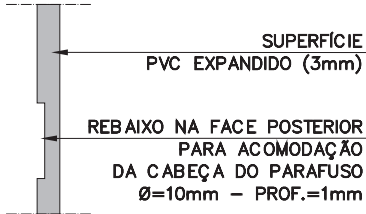

DETALHE  
FURAÇÃO NA SUPERFÍCIE  
ESC.: 1:1

Revisão 1  
Data 29/03/19

Página  
2/4

Código de listagem

1618079

**Atenção**  
Preserve a escala  
Quando for imprimir, use  
folhas A4 e desabilite a  
função "Fit to paper"

**Respeite o Meio Ambiente.**  
Imprima somente o ne-  
cessário

**FDE** FUNDAÇÃO PARA O  
DESENVOLVIMENTO  
DA EDUCAÇÃO

medidas em cm

SI-10

Placa 50 x 70cm  
(parede externa)

Revisão 1  
Data 29/03/19


Página  
3/4

Código de listagem  
1618079



**Atenção**  
Preserve a escala  
Quando for imprimir, use  
folhas A4 e desabilite a  
função "Fit to paper"

**Respeite o Meio Ambiente.**  
Imprima somente o ne-  
cessário

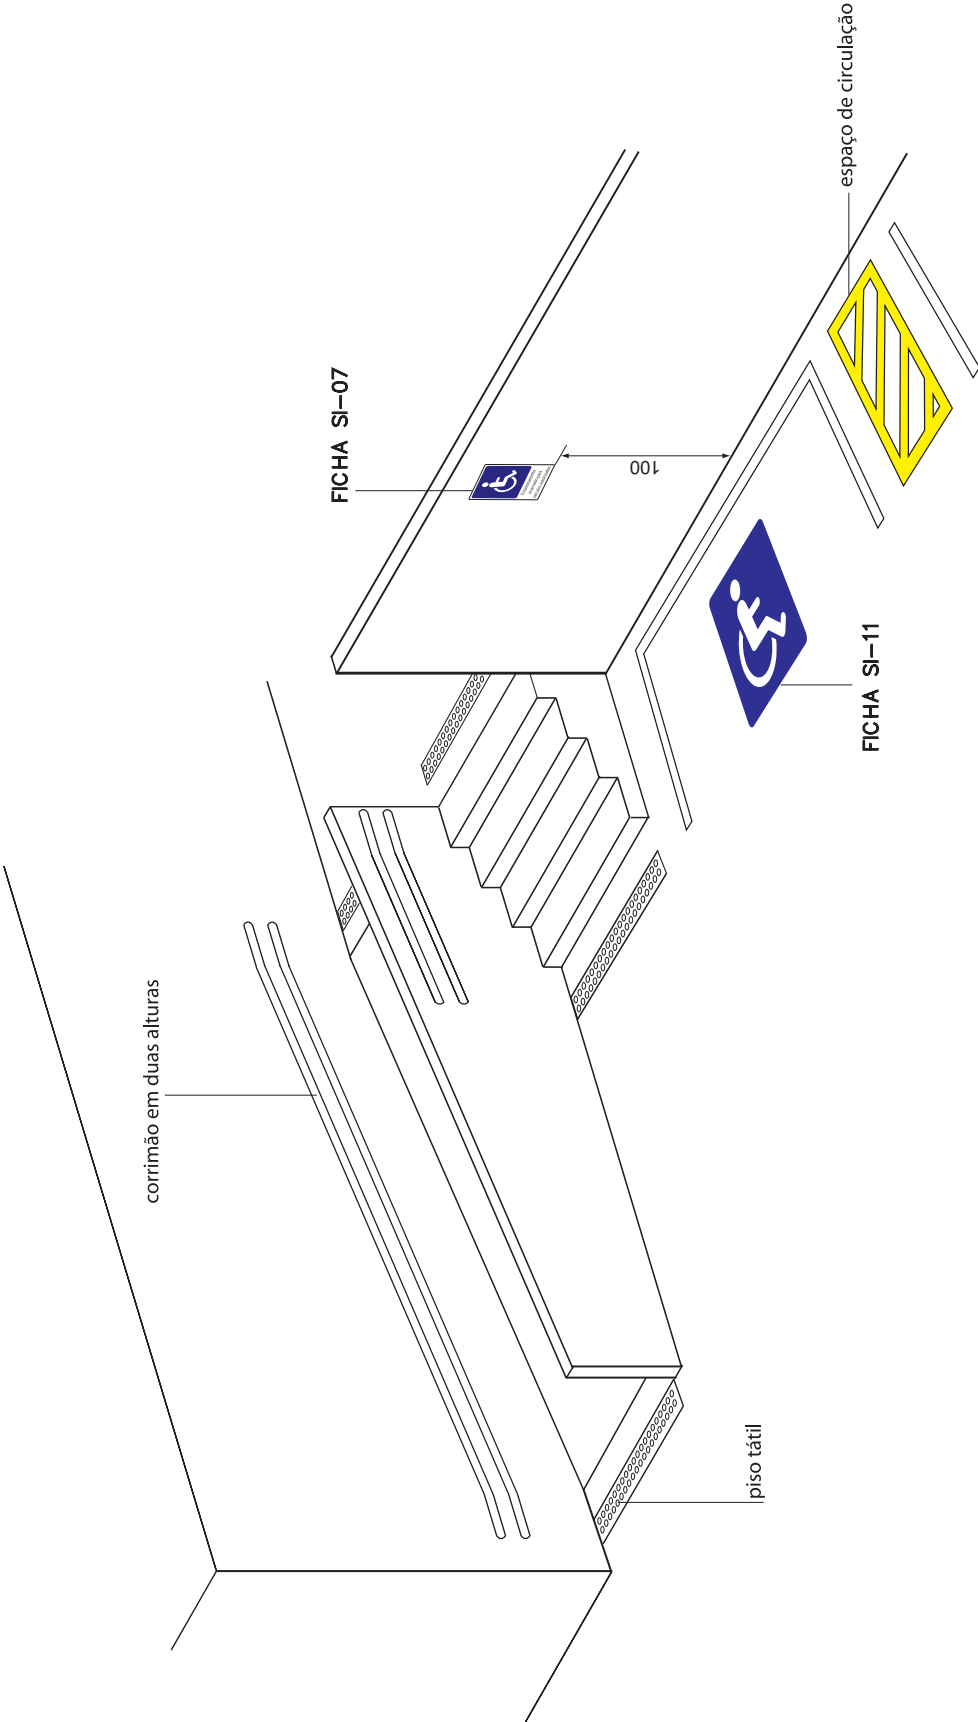

EXEMPLO DE APLICAÇÃO  
SINALIZAÇÃO DE ACESSIBILIDADE EM ÁREAS EXTERNAS  
SEM ESCALA

## SI-10

## Placa 50 x 70cm

(parede externa)

Revisão 1  
Data 29/03/19

Página  
4/4

## Código de listagem

1618079



**Atenção**  
Preserve a escala  
Quando for imprimir, use  
folhas A4 e desabilite a  
função "Fit to paper"

**Respeite o Meio Ambiente.**  
Imprima somente o ne-  
cessário

## DESCRIÇÃO

## Constituintes

- Base em aço galvanizado com espessura de 0,9mm, acabamento natural. Dimensões acabadas 50cm (largura) x 70cm (altura). Todos os bordos pintados com tinta em pó híbrida Epóxi/ Poliéster, eletrostática, brilhante, polimerizada em estufa, espessura mínima de 40 micrometros na cor BRANCA. Cantos arredondados conforme projeto.
- Superfície em PVC expandido com espessura de 3mm, na cor BRANCA. Dimensões acabadas 50cm (largura) x 70cm (altura). Cantos arredondados conforme projeto.
- Impressão na cor AZUL, aplicada na face frontal da superfície (PVC 3mm) através de impressão digital com proteção UV (definição mínima de 600 x 600 dpi). Fontes para textos: família Myriad.
- Face posterior da superfície (PVC 3mm) com rebaios para acomodação das cabeças dos parafusos, conforme projeto.
- Deve ser impresso na face frontal da superfície (PVC 3mm) o nome do fabricante (obrigatório) e a identificação do número do pedido para rastreamento (opcional); na face posterior deve ser impresso o símbolo internacional de reciclagem, apresentando o número identificador do polímero.
- Adesivo dupla face aplicado sobre todo o verso da base (aço 0,9mm) e da superfície (PVC 3mm).
- 10 parafusos autoataxarrantes de aço, zincados, cabeça chata, fenda comum, Ø 4,8mm x 38mm de comprimento.
- 10 buchas de Nylon tipo S6.

## Referência de cor

- Azul:  
- ref. CMYK - C: 100 M:100 Y:0 K:15

## Protótipo comercial

- Adesivo dupla face:  
- 3M SCOTCH YR-9625
- Parafusos:  
- CISER
- Buchas de nylon:  
- FISCHER

## Prestadores de serviço homologados

- SIGNOSINAL

## APLICAÇÃO

- Em paredes de ambientes externos, conforme indicação em projeto.

**Obs.1:** Os projetos de de sinalização deverão ser elaborados em consonância com as orientações do 'Manual do Sistema de Sinalização para Edificações Escolares' e em conformidade com os critérios da norma NBR 9050.

**Obs.2:** Cada projeto de sinalização deverá ser acompanhado da respectiva 'Planilha de Quantificação e Especificação' (SI-PQ).

## EXECUÇÃO

- A execução das placas deve ser realizada em conformidade com o solicitado na 'Planilha de Quantificação e Especificação' (SI-PQ).
- Para a impressão, devem ser utilizadas as artes correspondentes aos projetos gráficos de cada placa.
- Puncionamentos cônicos na base (aço galvanizado 0,9mm) para acomodação das cabeças dos parafusos (conforme desenho).
- Recorte e furação através de equipamento de corte tipo "Router".

**Obs.:** Os arquivos digitais referentes às artes das placas devem ser solicitados pelo fabricante à Supervisão de Especificação Técnica da Edificação da Gerência de Inovação e Tecnologia para a Edificação.

## INSTALAÇÃO

- A instalação das placas deve ser realizada em conformidade com o projeto de sinalização e com as orientações constantes do 'Manual do Sistema de Sinalização para Edificações Escolares'.
- Altura de instalação: a borda inferior da placa deve estar a 100cm do piso.
- Posicionamento: conforme indicação em projeto.
- Fixação e colagem:
  - confirmar texto e pictograma e local de fixação de cada placa;
  - preparar e limpar previamente a superfície que receberá a placa;
  - fixar a base (aço galvanizado 0,9mm) na parede com a fita dupla face e com os parafusos (posicionamento de acordo com a furação pré-executada na base);
  - em seguida, fixar a superfície (PVC 3mm) sobre a base (aço galvanizado 0,9mm) com a fita dupla face.

## FICHAS DE REFERÊNCIA

## Catálogo de Componentes

|       |       |                                                                    |
|-------|-------|--------------------------------------------------------------------|
| Ficha | SI-01 | Placa 20 x 20cm (porta)                                            |
| Ficha | SI-02 | Placa 20 x 20cm (parede)                                           |
| Ficha | SI-03 | Placa 20 x 20cm - acabamento fotoluminescente (parede)             |
| Ficha | SI-04 | Placa 70 x 20cm (porta)                                            |
| Ficha | SI-05 | Placa 70 x 20cm (parede)                                           |
| Ficha | SI-06 | Placa 70 x 20cm - acabamento fotoluminescente (parede)             |
| Ficha | SI-07 | Placa 50 x 6cm - texto em relevo e transcrição em Braille (parede) |
| Ficha | SI-08 | Placa 3 x 3cm - metálica em Braille (corrimão)                     |
| Ficha | SI-09 | Placa 50 x 50cm (parede externa)                                   |
| Ficha | SI-11 | Sinalização horizontal para vaga acessível                         |
| Ficha | SI-PQ | Planilha de quantificação e especificação                          |

## RECEBIMENTO

- Confirmar pictograma e local de fixação das placas com o projeto de sinalização.
- Verificar fixação e corte.
- Verificar altura, posicionamento, alinhamento e nivelamento.
- Verificar inexistência de rebarbas.

## SERVIÇOS INCLUÍDOS NO PREÇO

- Fornecimento das placas.
- Furação.
- Adesivo dupla face.
- Parafusos e buchas.
- Instalação.

## CRITÉRIOS DE MEDIÇÃO

- un. — por unidade instalada.

## NORMAS

- NBR 9050:2004 - Acessibilidade a edificações, mobiliário, espaços e equipamentos urbanos.
- **Obs:** As edições indicadas estavam em vigor no momento desta publicação. Como toda norma está sujeita à revisão recomenda-se verificar a existência de edições mais recentes das normas citadas.