

TJ-03

Torneira de
jardim

eco

Revisão 3
Data 13/08/04Página
1/2

Código de listagem


0817081



Atenção

Preserve a escala
Quando for imprimir, use
folhas A4 e desabilite a
função "Fit to paper"

Respeite o Meio Ambiente.
Imprima somente o ne-
cessário

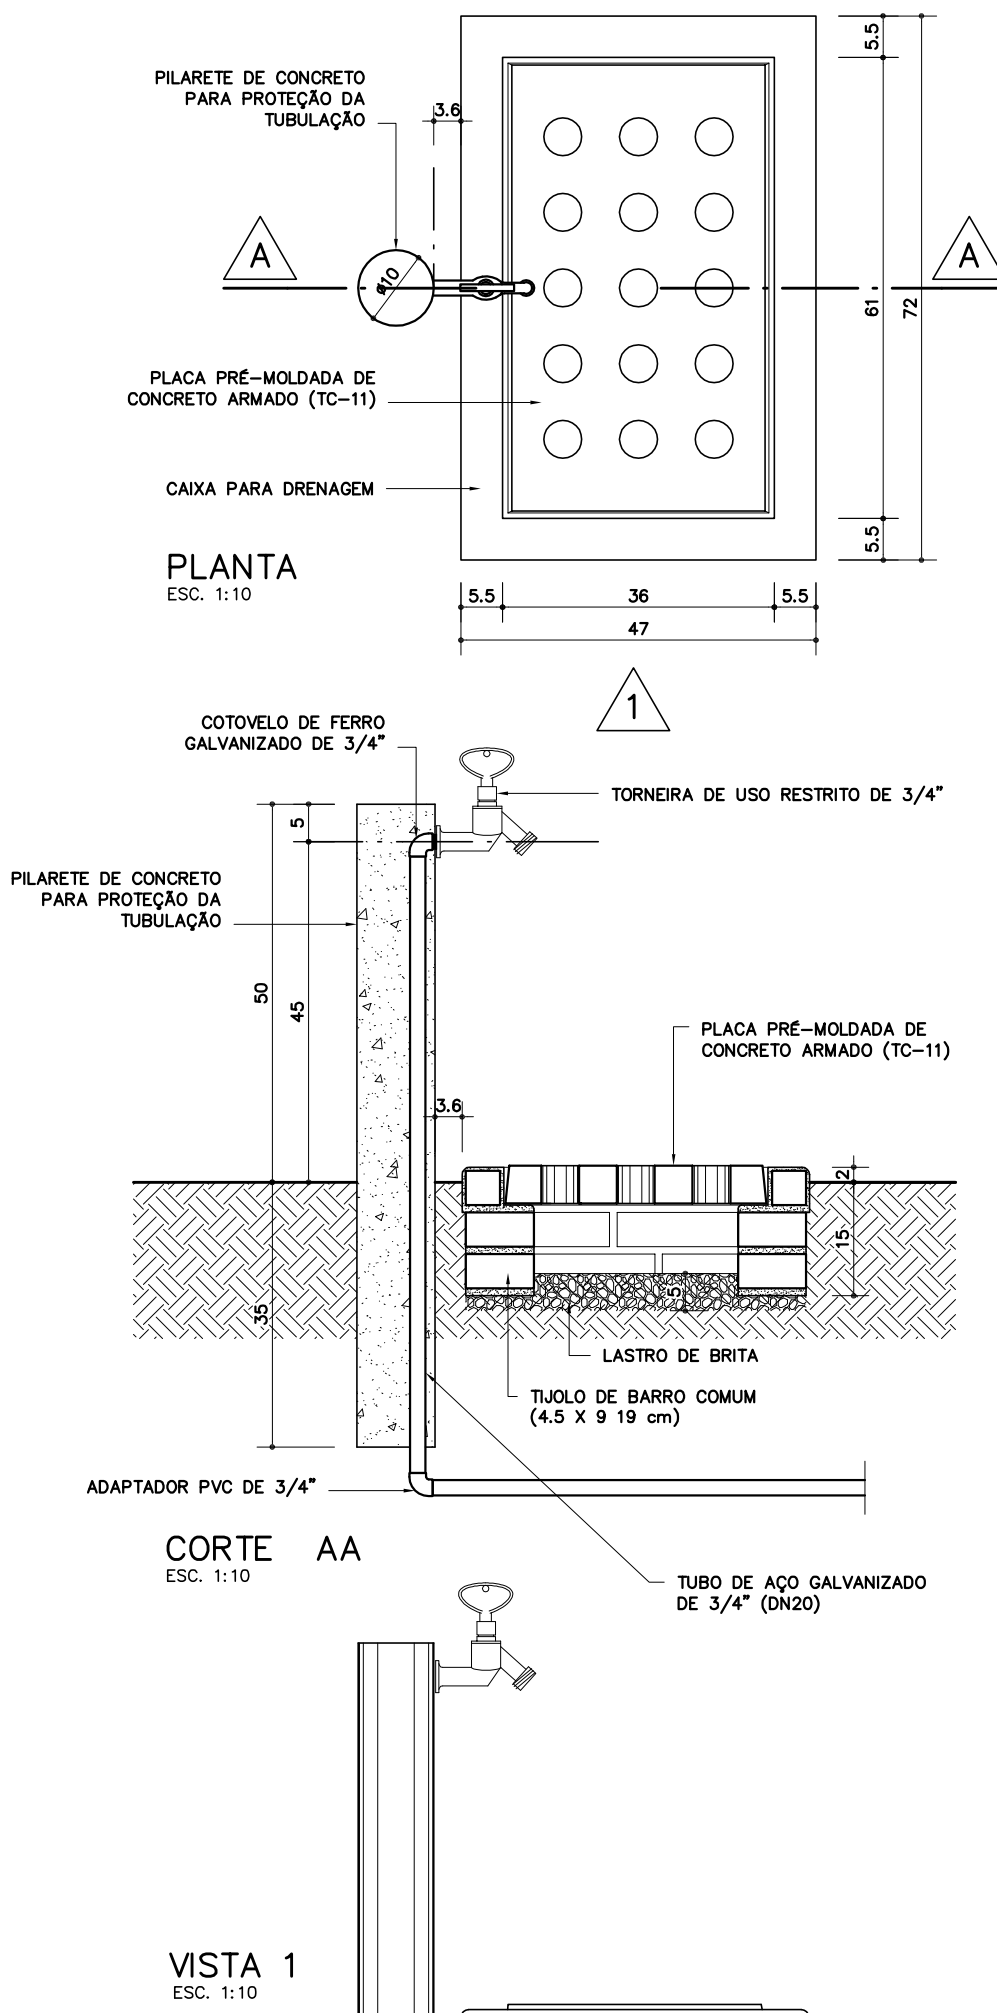

TJ-03

Torneira de jardim
eco

Revisão 3
Data 13/08/04

Página
2/2

Código de listagem

0817081



Atenção

Preserve a escala
Quando for imprimir, use
folhas A4 e desabilite a
função "Fit to paper"

Respeite o Meio Ambiente.
Imprima somente o ne-
cessário

DESCRIÇÃO

Constituintes

- Torneira de pressão de 3/4", de uso restrito (ver Fichas de Referência), eixo de entrada de água horizontal.
- Cotovelo em 90° de ferro galvanizado, DN 20mm (3/4").
- Tubo de aço galvanizado DN 20mm (3/4") revestido em concreto, conforme desenho.
- Caixa de alvenaria de tijolos de barro comum (4,5 x 9 x 19cm), com argamassa, conforme desenho.
- Placa pré-moldada de concreto armado com furos para drenagem TC-11 (ver Fichas de Referência).
- Área permeável em lastro de brita nº 2, conforme desenho.

Acessórios

- Fita veda-rosca de politetrafluoretileno, para vedação das junções até o cotovelo.
- Trava química anaeróbica, para travamento da torneira ao cotovelo.

Protótipo comercial

- Placa pré-moldada:
 - NEO REX (GC 05)
- Torneira:
 - DOCOL (20000906)
 - DECA (1156C)
- Fita veda-rosca:
 - TIGRE
 - FORTILIT
 - POLYTUBES
- Trava química:
 - LOCTITE (242)
 - COLAMAIS (CM67)

APLICAÇÃO

- Para uso externo, preferencialmente em jardins.
- **Obs.:** A chave de acionamento destacável deve ficar sob a guarda de pessoa indicada pela direção da escola.

EXECUÇÃO

- Escavação manual em terra e apiloamento do fundo.
- Preencher a área escavada com brita nº 2 nivelada, conforme desenho.
- Executar a caixa de alvenaria de tijolos de barro com argamassa traço 1:0,5:4,5, cimento, cal e areia.
- Executar o pilarete de concreto, tendo como fôrma tubo de PVC para esgoto Ø=100 mm (4"). Após a cura do concreto (24h) cortar e eliminar o molde.
- Fixar torneira travando-a com trava química, conforme orientação da ficha H6.15 (ver Fichas de Referência).

FICHAS DE REFERÊNCIA

Catálogo de Serviços

Ficha	S12.15	Pedrisco
Ficha	S14.17	Galvanização
Ficha	H2.05	Tubos de aço e conexões de ferro galvanizado
Ficha	H6.15	Torneira de uso restrito

Catálogo de Componentes

Ficha	TC-09 a TC-11	Tampa de concreto perfurada para canaleta a.p.
-------	---------------	--

RECEBIMENTO

- Aferir a conformidade com os protótipos homologados.
- Verificar nivelamento da fundo da caixa de alvenaria preenchida com brita.

- Verificar se o protetor do tubo constitui uma única peça de concreto, perfeitamente lisa, plana e nivelada, sem imperfeições na superfície ou arestas mal acabadas.
- Verificar na placa pré-moldada de concreto a ausência de defeitos visíveis, como rachaduras e lascados.
- Verificar, na torneira, a ausência de defeitos no acabamento superficial (ver Fichas de Referência), a ausência de vazamentos.
- Verificar se a torneira não apresenta trincas, entalhos ou rebarbas.
- Verificar se a torneira está na posição adequada.
- Para confirmação do uso da trava química, verificar impossibilidade de extrair a torneira manualmente (sem uso de ferramentas).
- Verificar se a chave de acionamento destacável está sob a guarda da pessoa indicada pela direção da escola.

SERVIÇOS INCLUÍDOS NOS PREÇOS

- Fornecimento do concreto, formas e execução das peças.
- Fornecimento dos tubos, junções, fita veda-rosca, torneira com trava química, bem como a instalação destas peças.
- Fornecimento e execução da caixa de alvenaria de tijolos de barro.
- Fornecimento da brita e execução do recobrimento correspondente.

CRITÉRIOS DE MEDIÇÃO

- un. — por unidade instalada.

NORMAS

- NBR 10281 - Torneira de pressão - Requisitos e métodos de ensaio.
- Decreto Estadual 45.805 - Institui medidas de redução de consumo e racionalização do uso de água no âmbito do Estado de São Paulo.
- Decreto Estadual 48.138 - Programa estadual de uso racional de água potável.